

LISTADO DE PLANOS FASE DE CERTIFICADO FINAL DE OBRA:

**REFORMA INTERIOR PARA CENTRO DE REHABILITACIÓN.
Avda. Valdearganda, 2-Local. Arganda del Rey (Madrid), CP: 28500**

nº orden	Nº PLANO	NOMBRE	fecha
1	01	SITUACIÓN	27/11/2023
2	02	EMPLAZAMIENTO	27/11/2023
3	03	PLANTA BAJA: ESTADO ACTUAL	27/11/2023
4	04	ALZADOS: ESTADO ACTUAL	27/11/2023
5	05	SECCIÓN LONGITUDINAL: ESTADO ACTUAL	27/11/2023
6	06	PLANTA BAJA: DISTRIBUCIÓN, ESTADO REFORMADO	27/11/2023
7	07	PLANTA BAJA: EQUIPAMIENTO	27/11/2023
8	08	PLANTA BAJA: COTAS	27/11/2023
9	09	PLANTA BAJA: COTAS SANITARIOS	27/11/2023
10	10	ALZADO PRINCIPAL: ESTADO REFORMADO	27/11/2023
11	11	ALZADO POSTERIOR: ESTADO REFORMADO	27/11/2023
12	12	DETALLE DE RAMPA Y BARANDILLAS	27/11/2023
13	13	SECCIÓN LONGITUDINAL POR PASILLO: ESTADO REFORMADO	27/11/2023
14	14	SECCIÓN LONGITUDINAL POR ASEOS: ESTADO REFORMADO	27/11/2023
15	15	SECCIÓN LONGITUDINAL POR SALAS DE TRATAMIENTOS: ESTADO REFORMADO	27/11/2023
16	16	SECCIÓN TRANSVERSAL POR PASILLO: ESTADO REFORMADO	27/11/2023
17	17	SECCIONES TRANSVERSALES POR SALAS DE TRATAMIENTOS: ESTADO REFORMADO	27/11/2023
18	18	PLANTA BAJA: SUELOS	27/11/2023
19	19	PLANTA BAJA: TECHOS	27/11/2023
20	20	CARPINTERÍA: PLANTA	27/11/2023
21	21	CARPINTERÍA: MAMPARAS	27/11/2023
22	22	CARPINTERÍA: PUERTAS	27/11/2023
23	23	TABIQUERÍA: PLANTA	27/11/2023
24	24	DESPIECE DE SUELOS VINÍLICOS	27/11/2023
25	25	ACABADO DE PAREDES	27/11/2023
26	I.01	FONTANERÍA	27/11/2023
27	I.02	SANEAMIENTO	27/11/2023
28	I.03	PLANTA: ESQUEMA DE PRINCIPIO 1. CLIMATIZACIÓN Y VENTILACIÓN	27/11/2023
29	I.04	SECCIÓN: ESQUEMA DE PRINCIPIO 2. CLIMATIZACIÓN Y VENTILACIÓN	27/11/2023
30	I.05	PLANTA: CLIMATIZACIÓN Y VENTILACIÓN	27/11/2023
31	I.06	PROTECCIÓN CONTRA INCENDIOS - OCUPACIÓN Y EVACUACIÓN	27/11/2023
32	I.07	PROTECCIÓN CONTRA INCENDIOS - INSTALACIONES	27/11/2023
33	I.08	ILUMINACIÓN	27/11/2023
34	I.09	ELECTRICIDAD-FUERZA	27/11/2023
35	I.10	ELECTRICIDAD: ESQUEMA UNIFILAR	27/11/2023
36	I.11	VOZ / DATOS	27/11/2023



PEGASUS

REFORMA DE LOCAL PARA CENTRO DE REHABILITACIÓN EN AVDA. DE VALDEARGANDA, 2, ARGANDA DEL REY, MADRID (CP: 28500)

Arquitecto: Pablo Mosquera de Arancibia Con el patrocinio de:

colegiado COAM, nº: 11.444



eduetrade

FASE: DIRECCIÓN DE OBRA-CERTIFICADO FINAL DE OBRA

PLANO DE SITUACIÓN

fecha: 27/11/2023

01

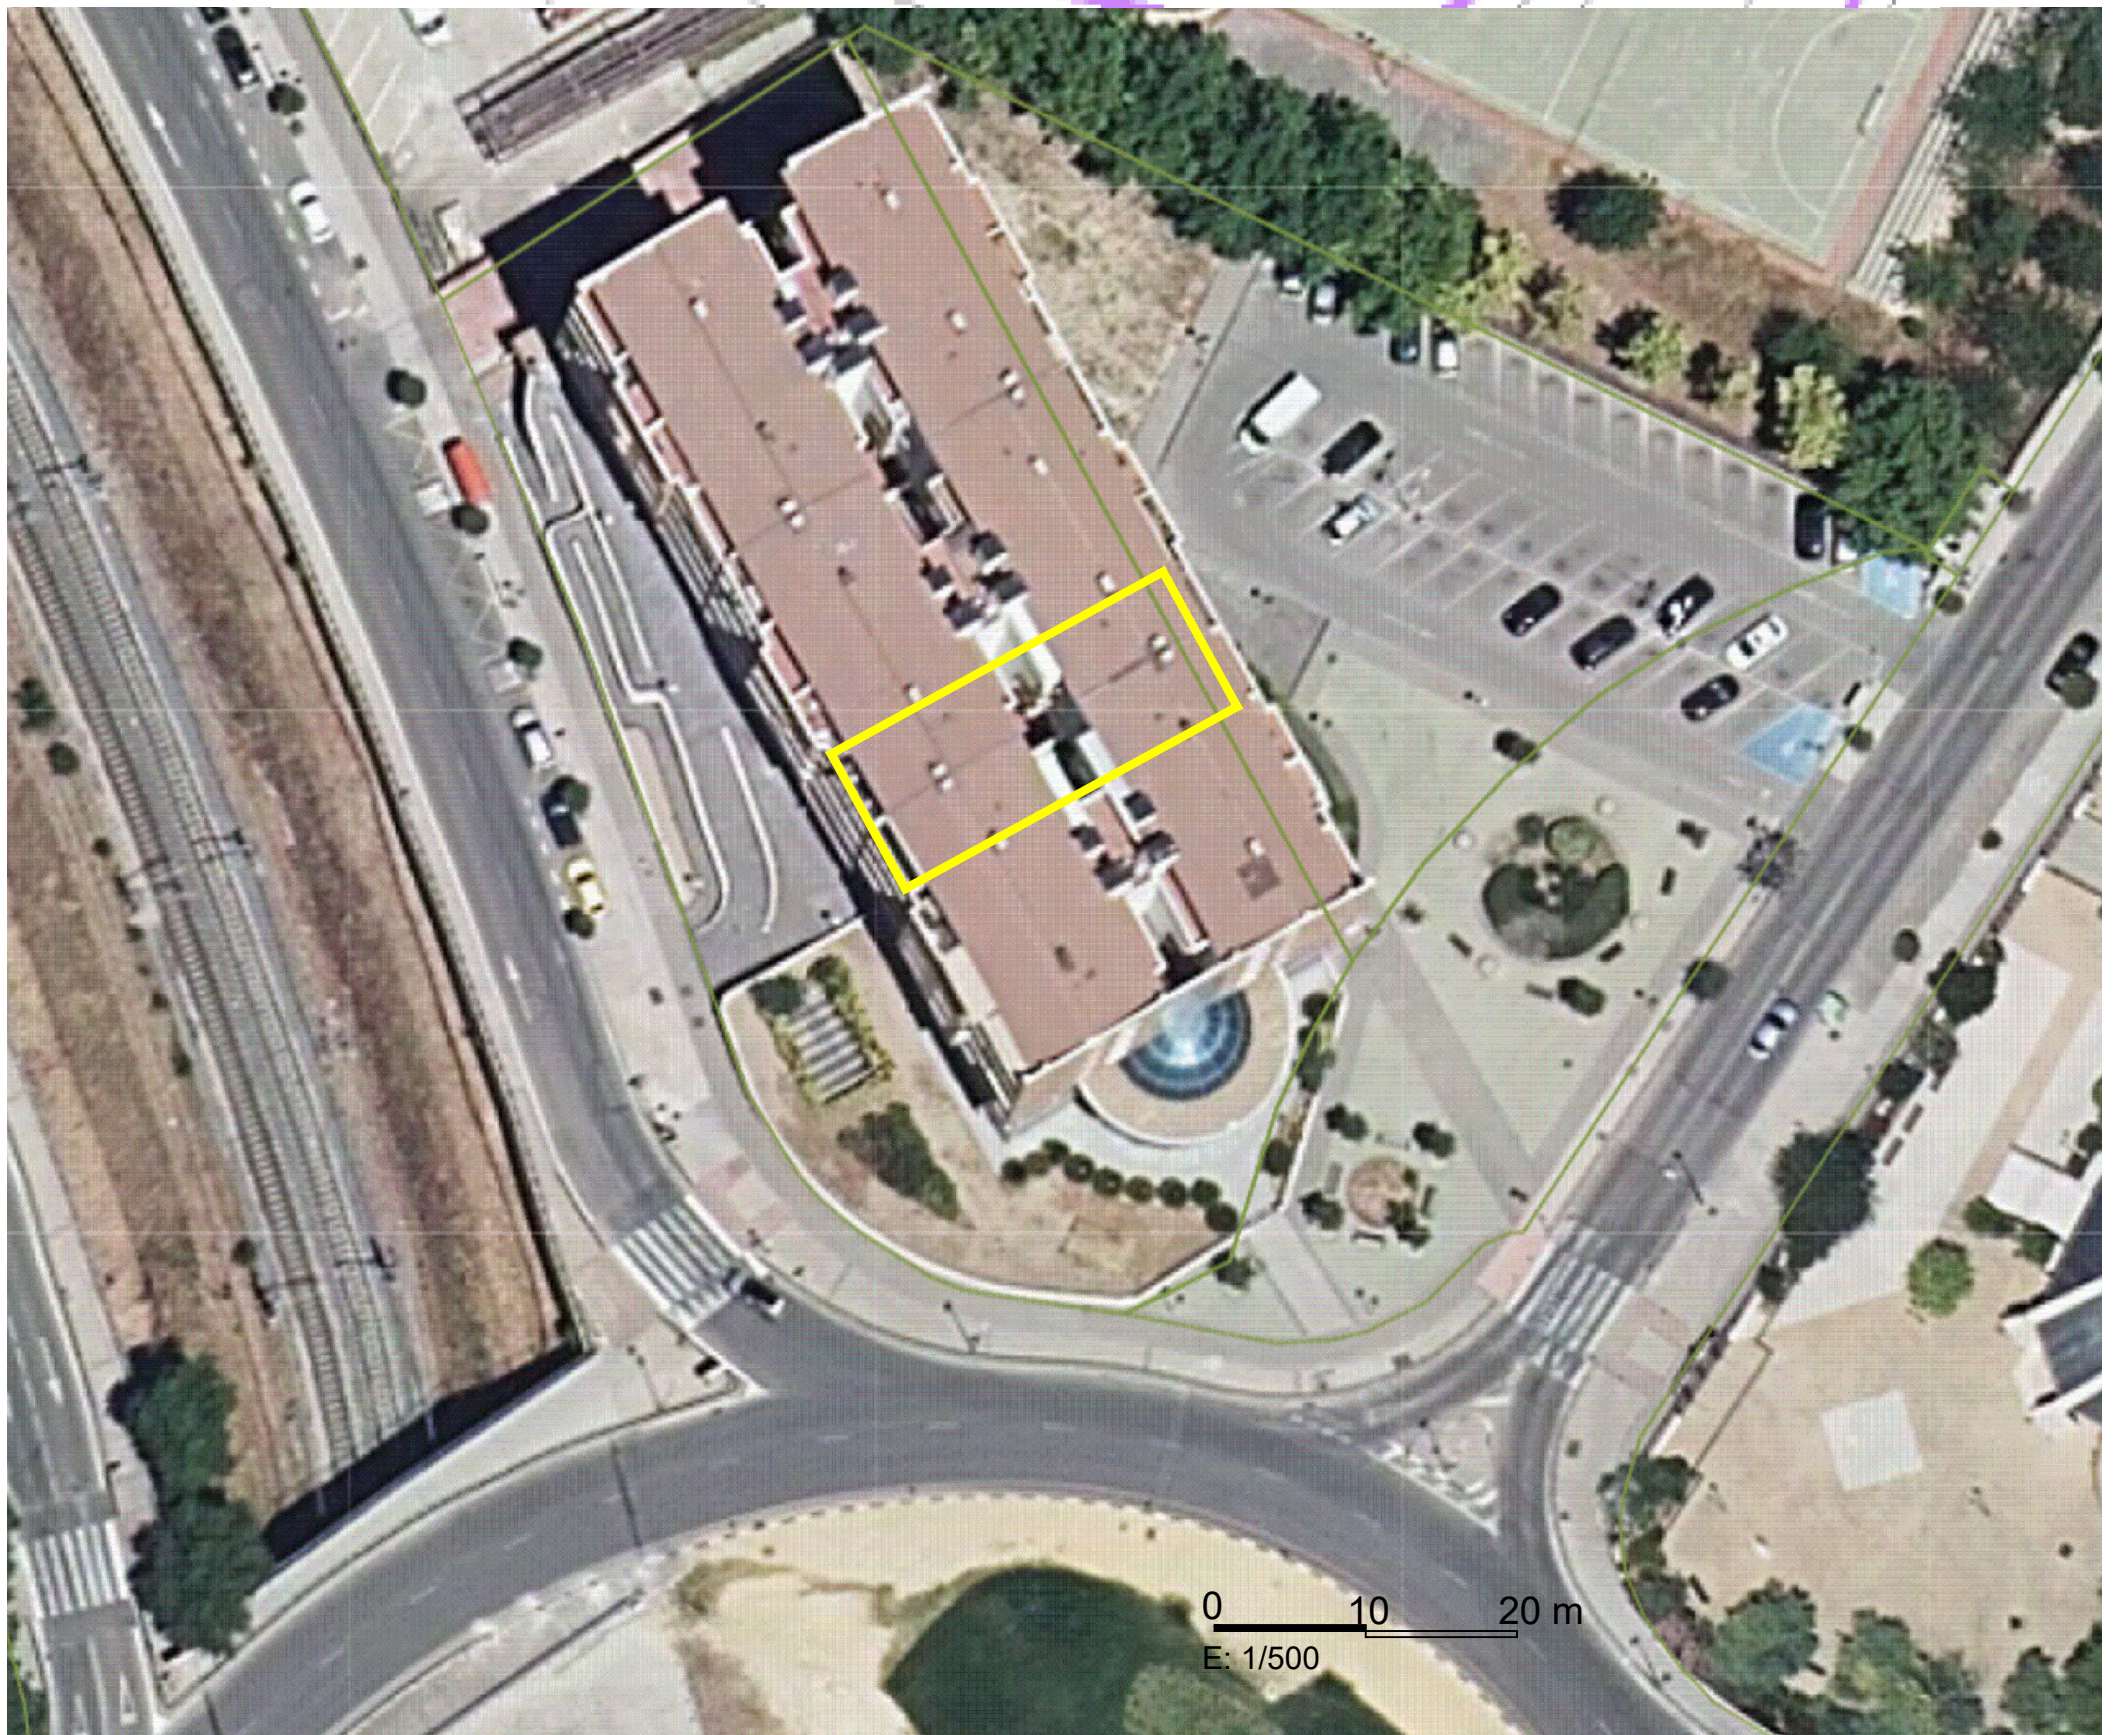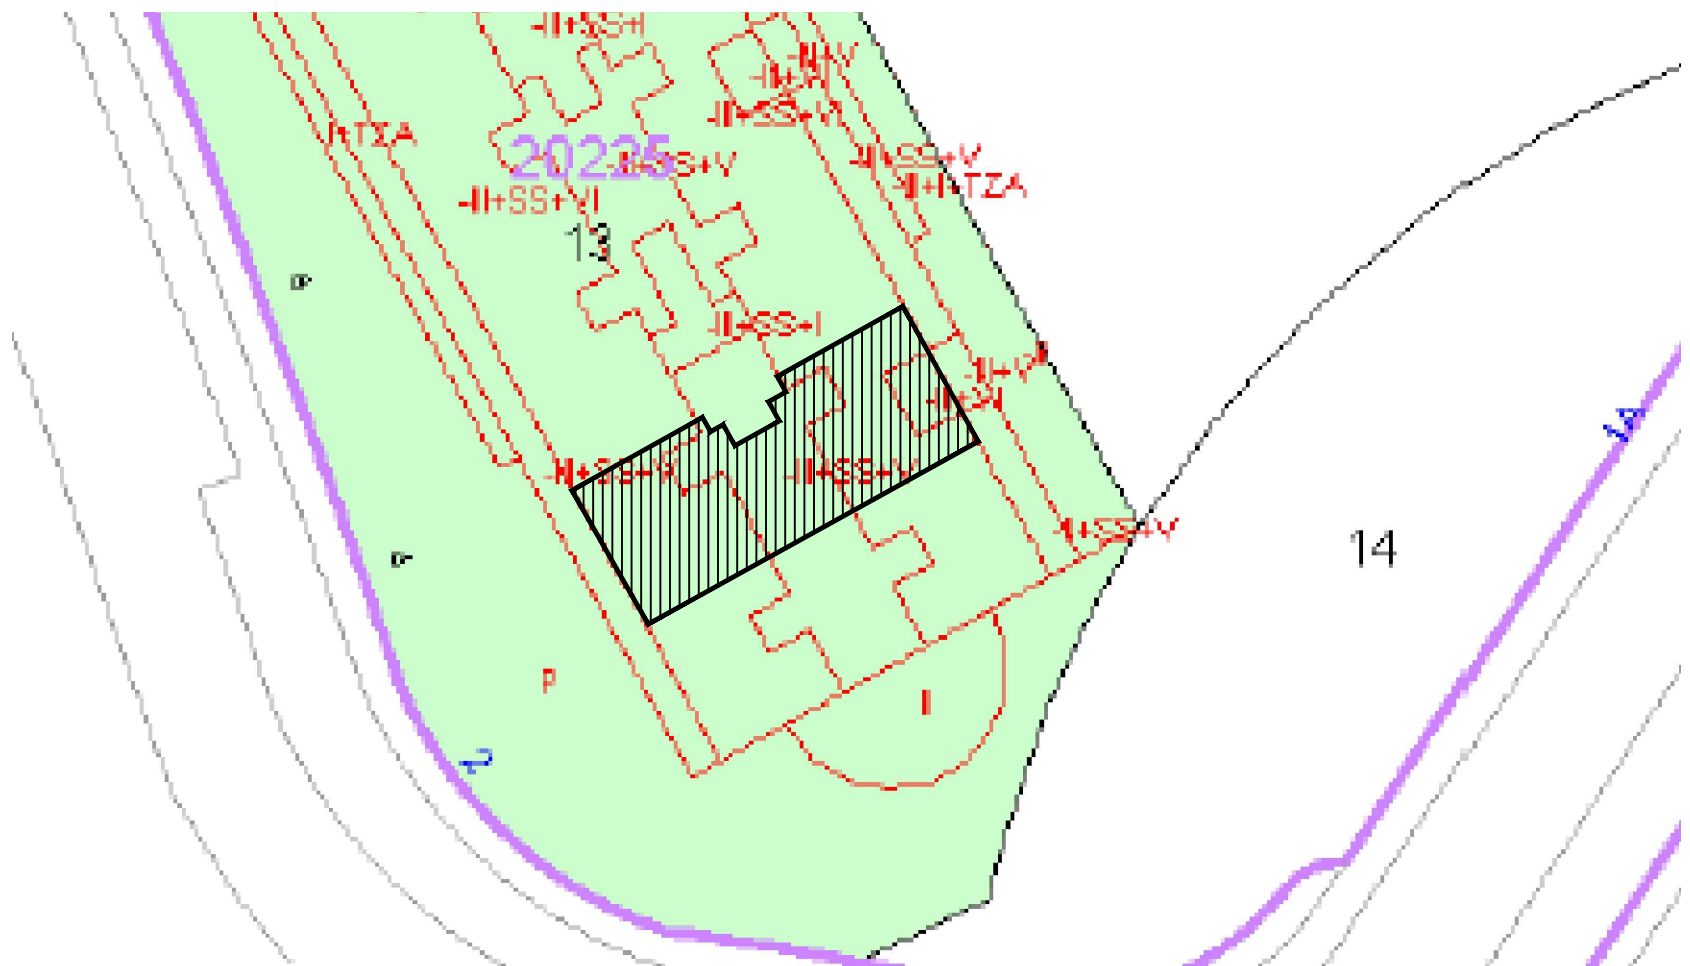

PEGASUS

REFORMA DE LOCAL PARA CENTRO DE REHABILITACIÓN EN AVDA. DE VALDEARGANDA, 2, ARGANDA DEL REY, MADRID (CP: 28500)

Arquitecto: Pablo Mosquera de Arancibia Con el patrocinio de:


edutrade

fecha: 27/11/2023

FASE: DIRECCIÓN DE OBRA-CERTIFICADO FINAL DE OBRA

PLANO DE EMPLAZAMIENTO


02

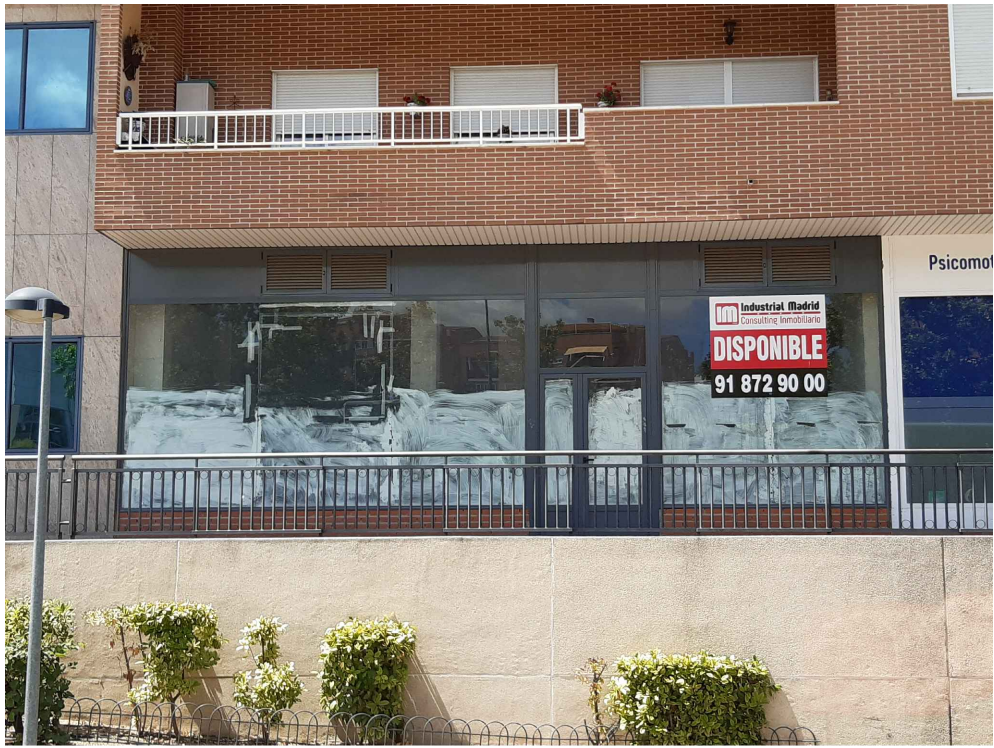


FACHADA POSTERIOR



FACHADA PRINCIPAL

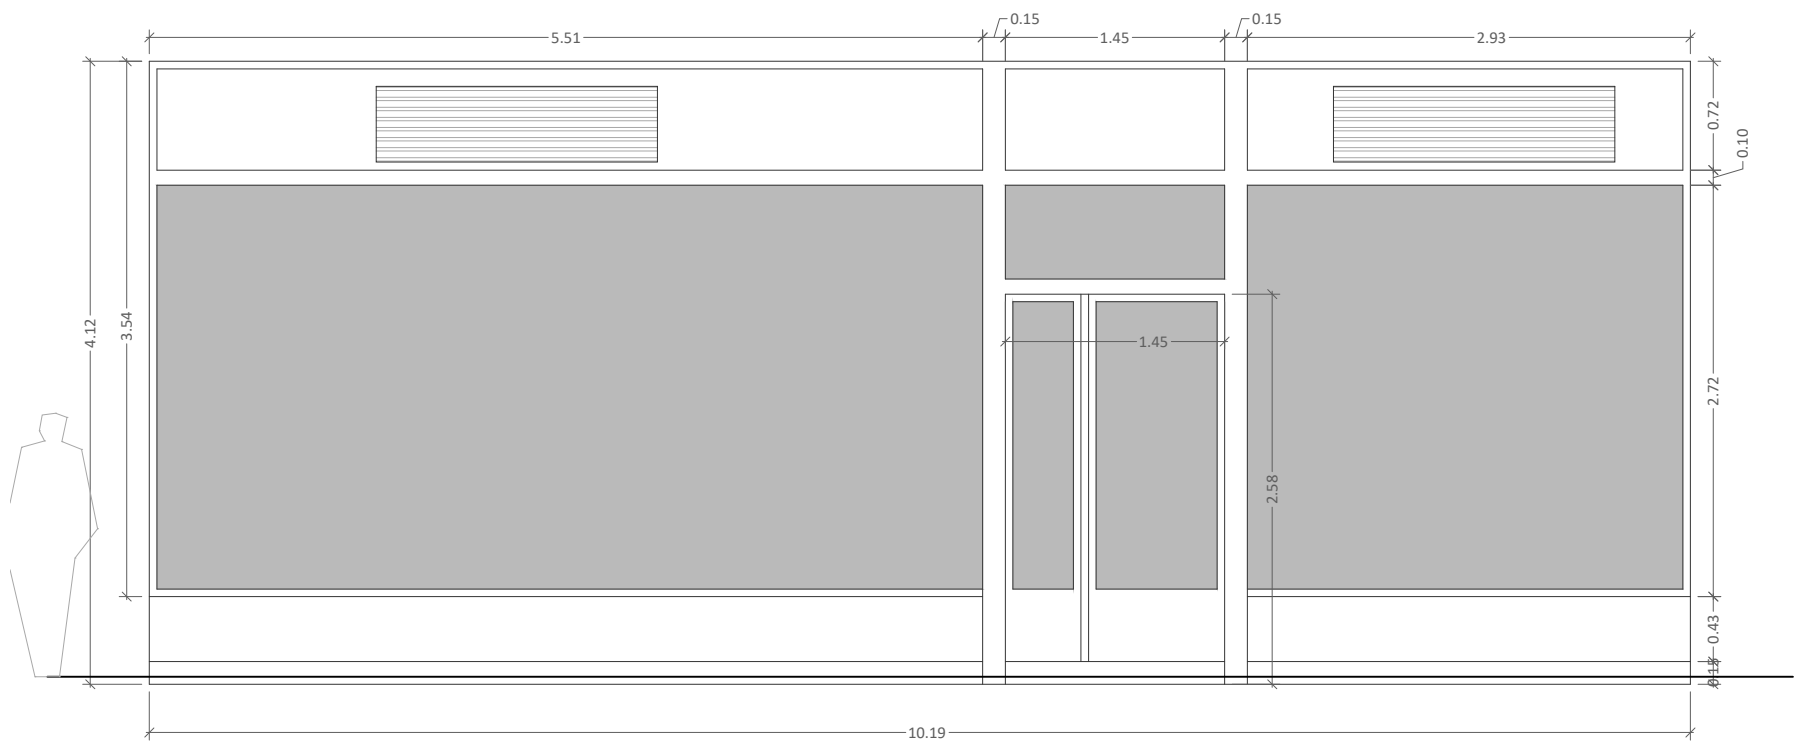

FACHADA TRASERA (Este)

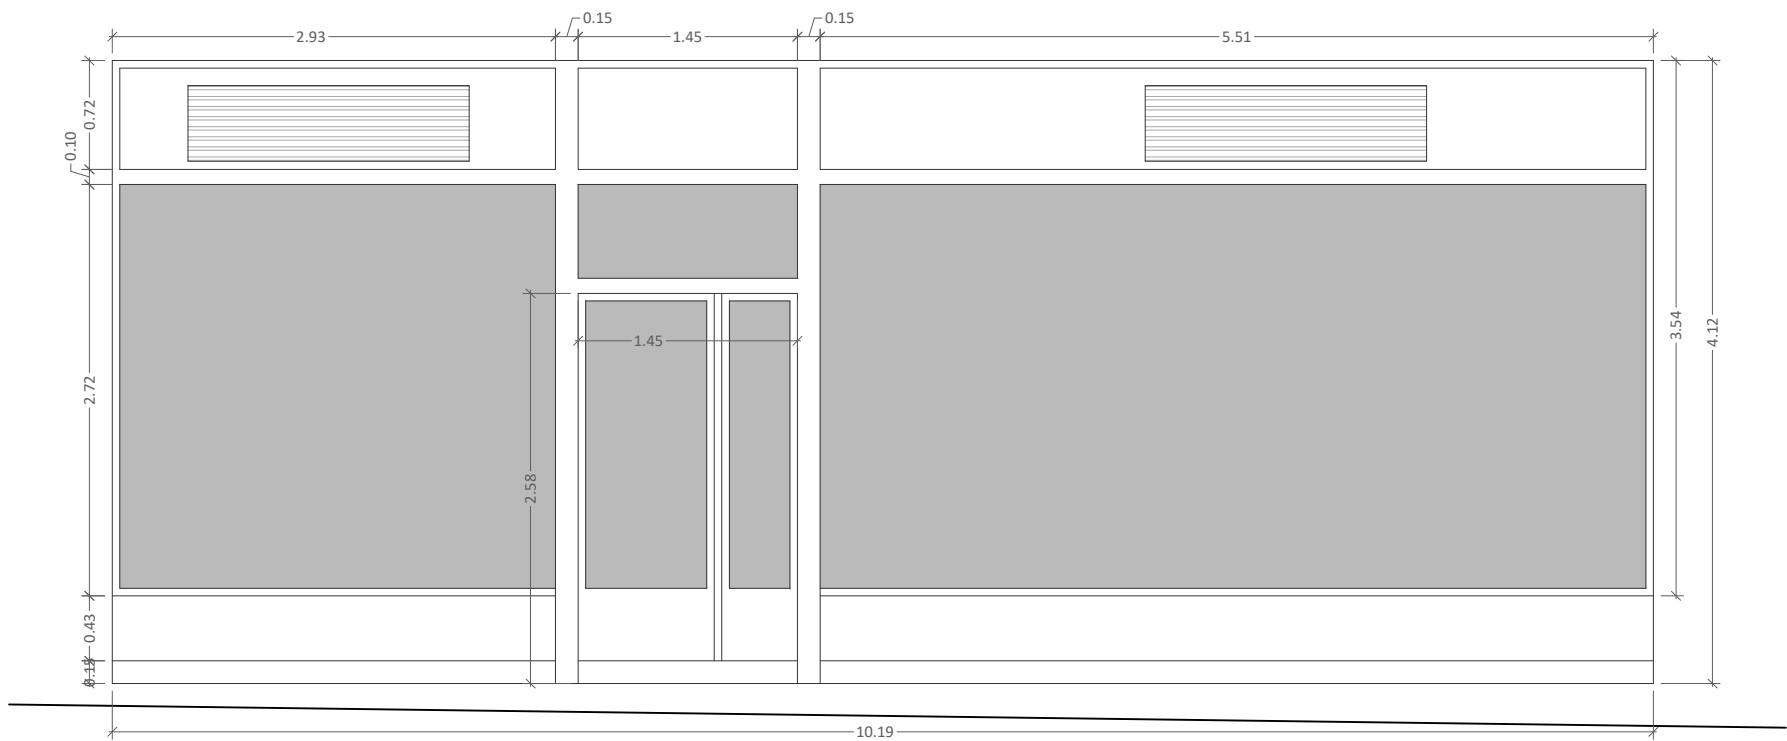

FACHADA PRINCIPAL (Oeste)





PEGASUS

REFORMA DE LOCAL PARA CENTRO DE REHABILITACIÓN EN AVDA. DE VALDEARGANDA, 2, ARGANDA DEL REY, MADRID (CP: 28500)
Arquitecto: Pablo Mosquera de Arancibia Con el patrocinio de: **eduetrade** fecha: 27/11/2023
colegiado COAM, nº: 11.444

FASE: DIRECCIÓN DE OBRA-CERTIFICADO FINAL DE OBRA

ALZADOS: ESTADO ACTUAL

04

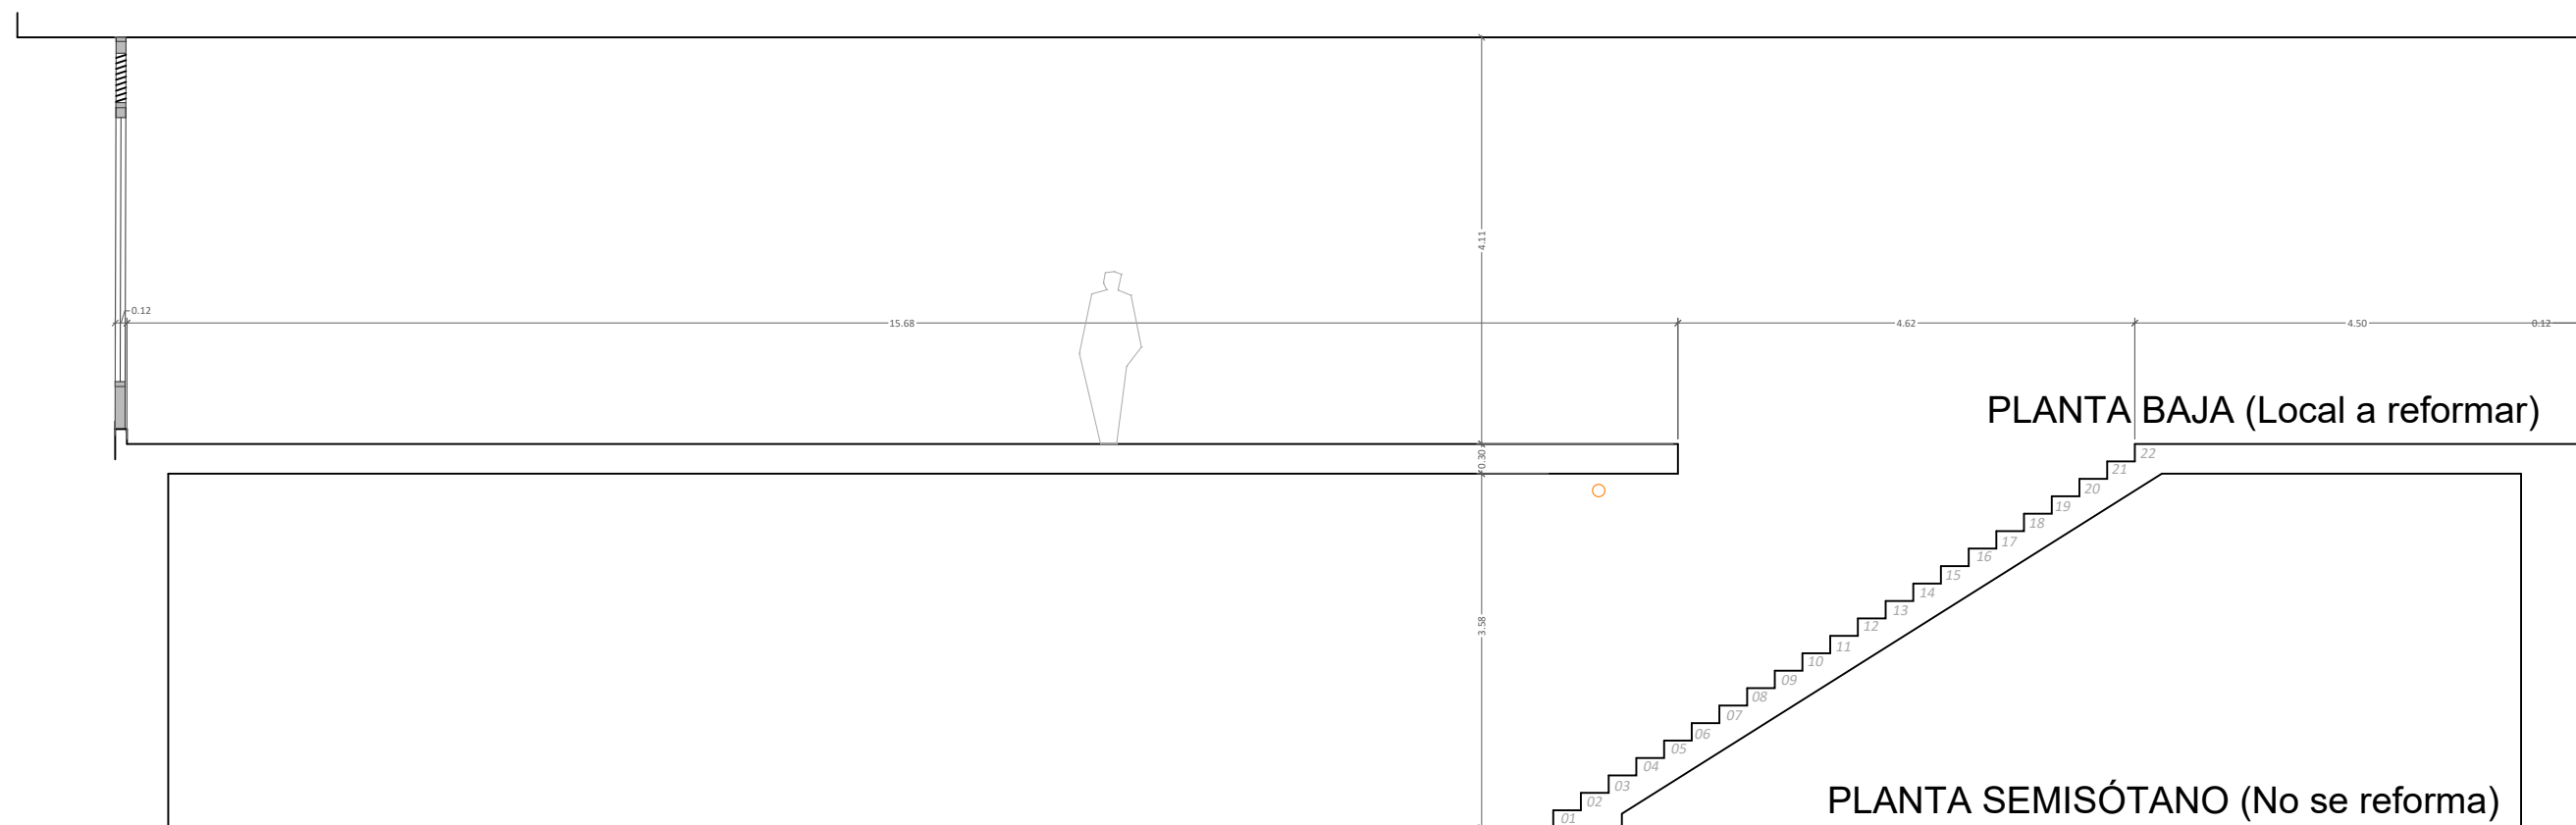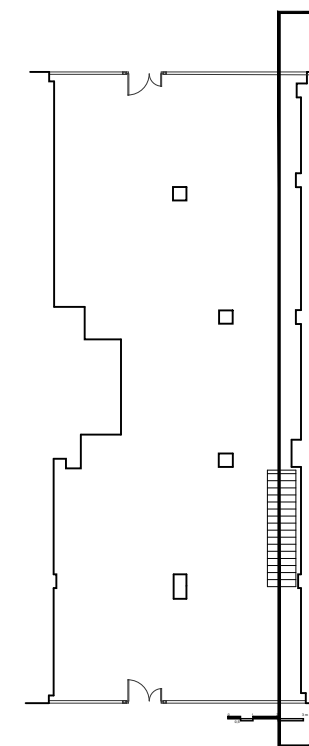

E: 1/75



PEGASUS

REFORMA DE LOCAL PARA CENTRO DE REHABILITACIÓN EN AVDA. DE VALDEARGANDA, 2, ARGANDA DEL REY, MADRID (CP: 28500)

Arquitecto: Pablo Mosquera de Arancibia

colegiado COAM, nº: 11.444


Con el patrocinio de:

educetrade

fecha: 27/11/2023

SECCIÓN LONGITUDINAL: ESTADO ACTUAL

05

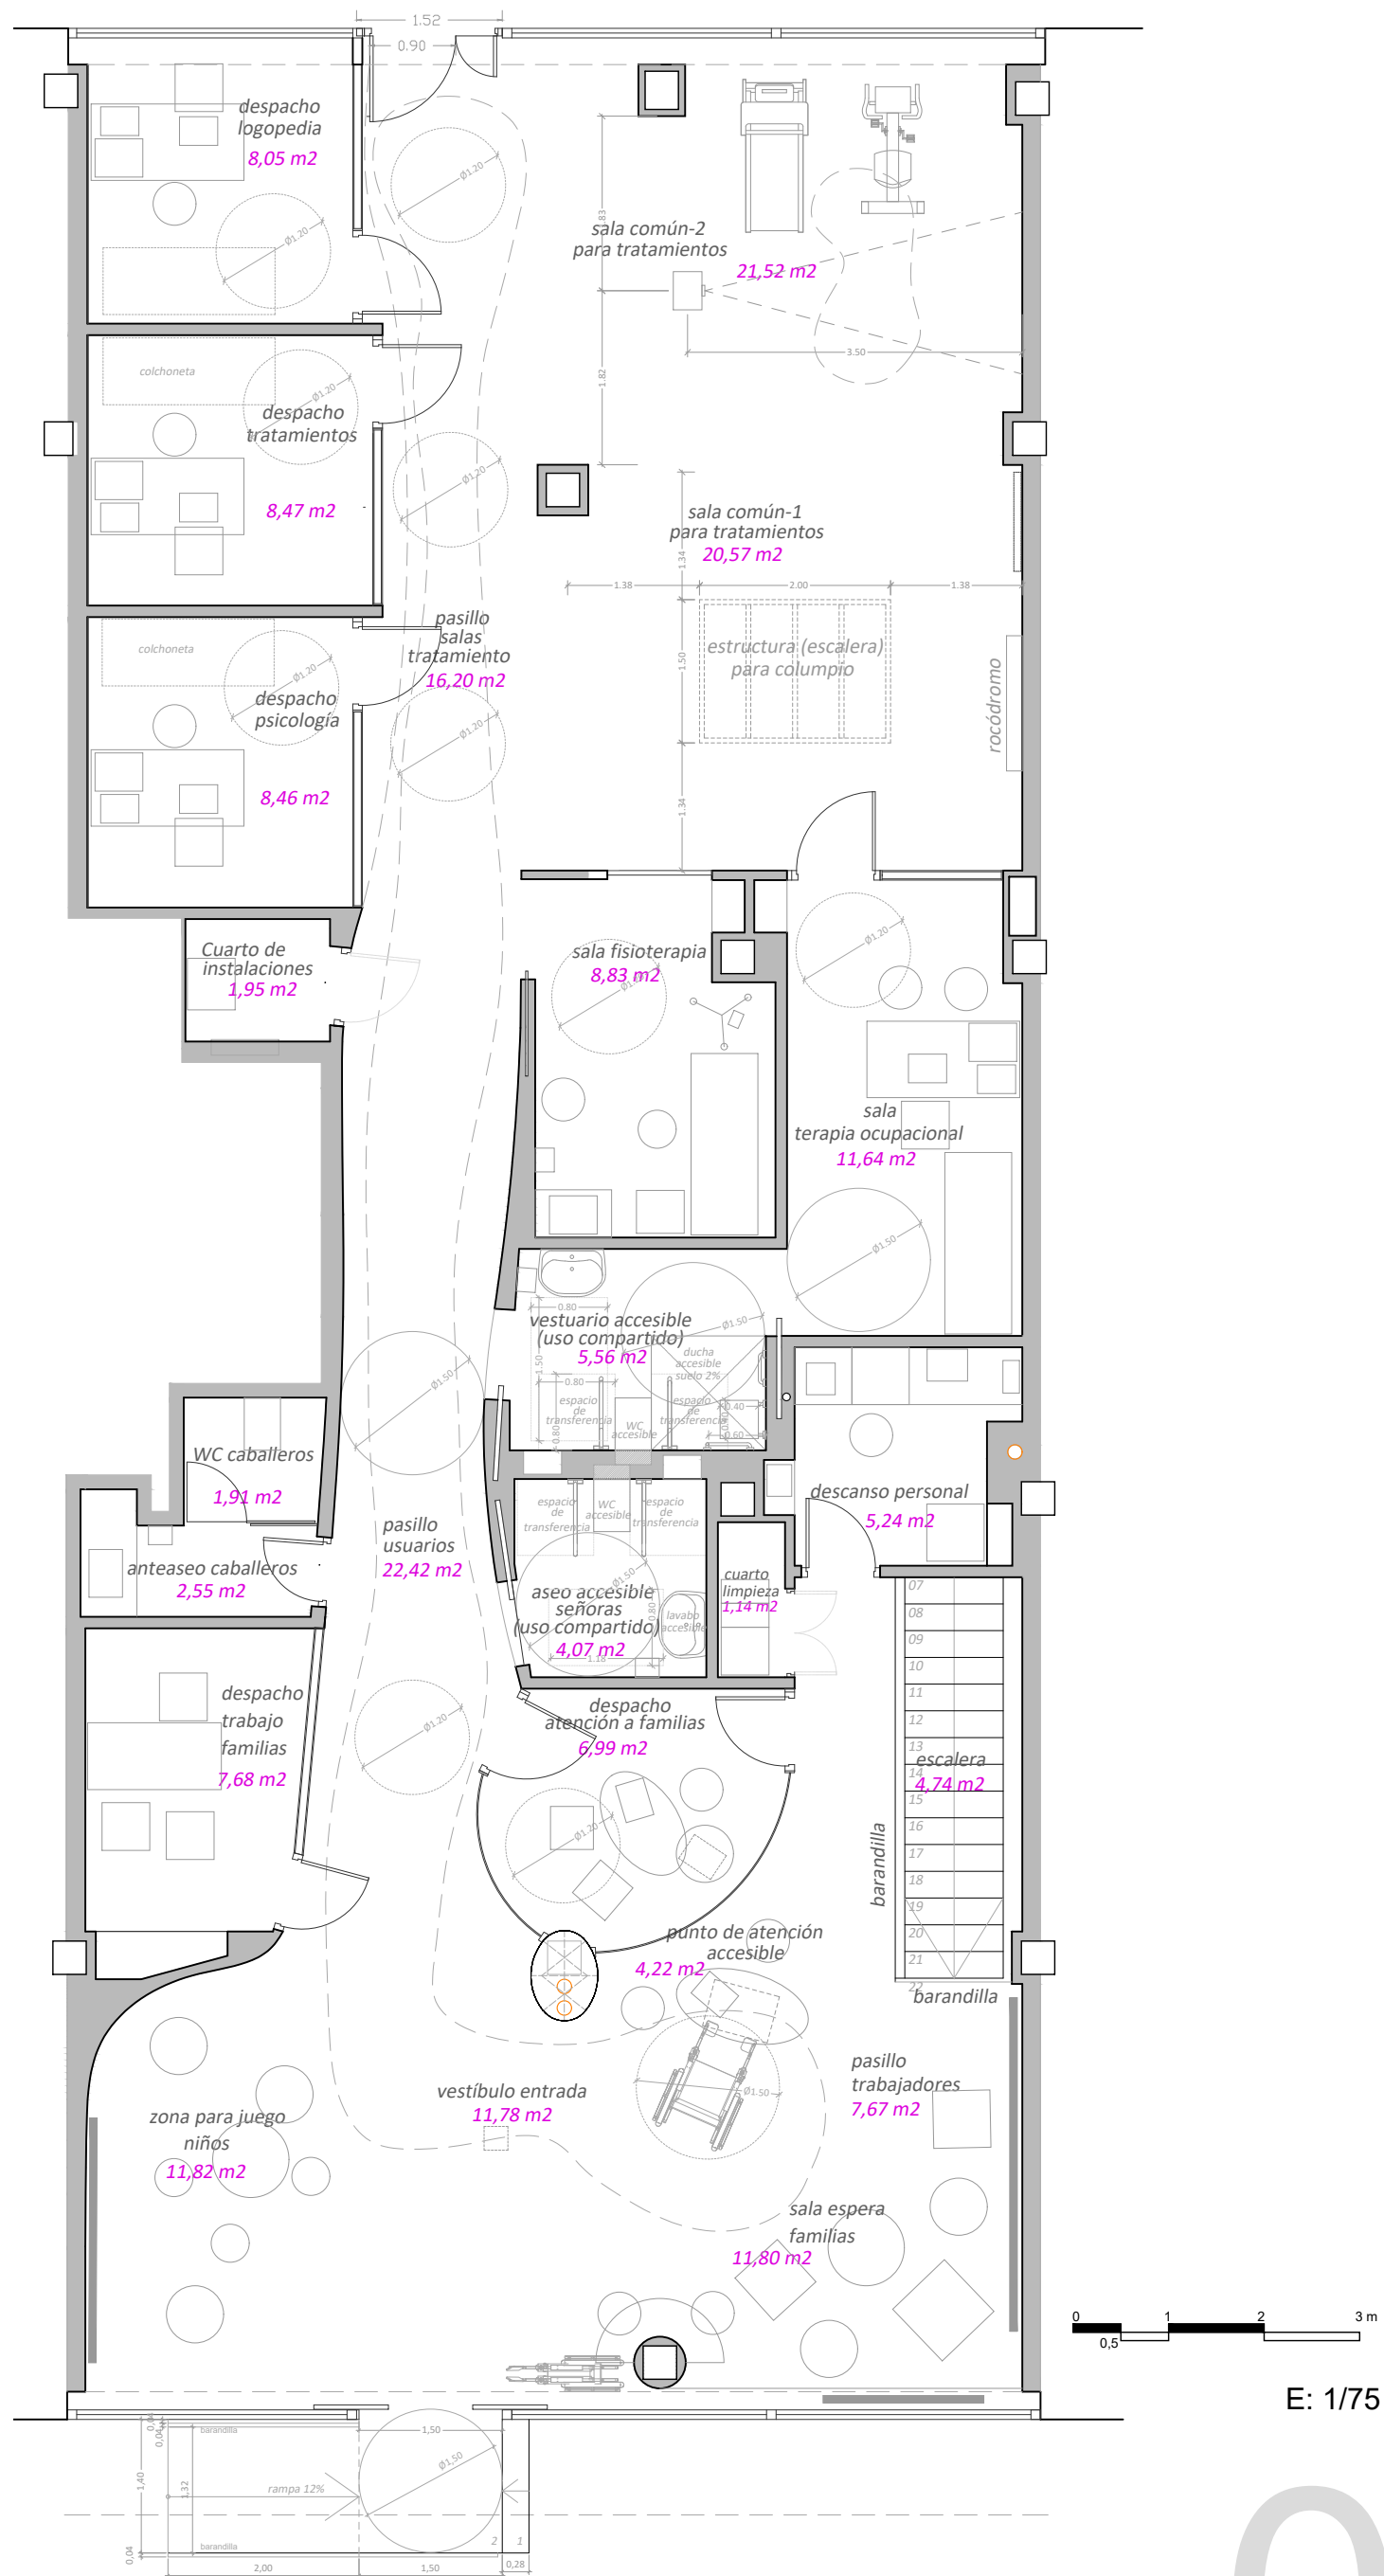

PEGASUS

REFORMA DE LOCAL PARA CENTRO DE REHABILITACIÓN EN AVDA. DE VALDEARGANDA, 2, ARGANDA DEL REY, MADRID (CP: 28500)

Arquitecto: Pablo Mosquera de Arancibia Con el patrocinio de:

edustrade


fecha: 27/11/2023

colegiado COAM, nº: 11.444

PLANTA BAJA: DISTRIBUCIÓN

FASE: DIRECCIÓN DE OBRA-CERTIFICADO FINAL DE OBRA

06

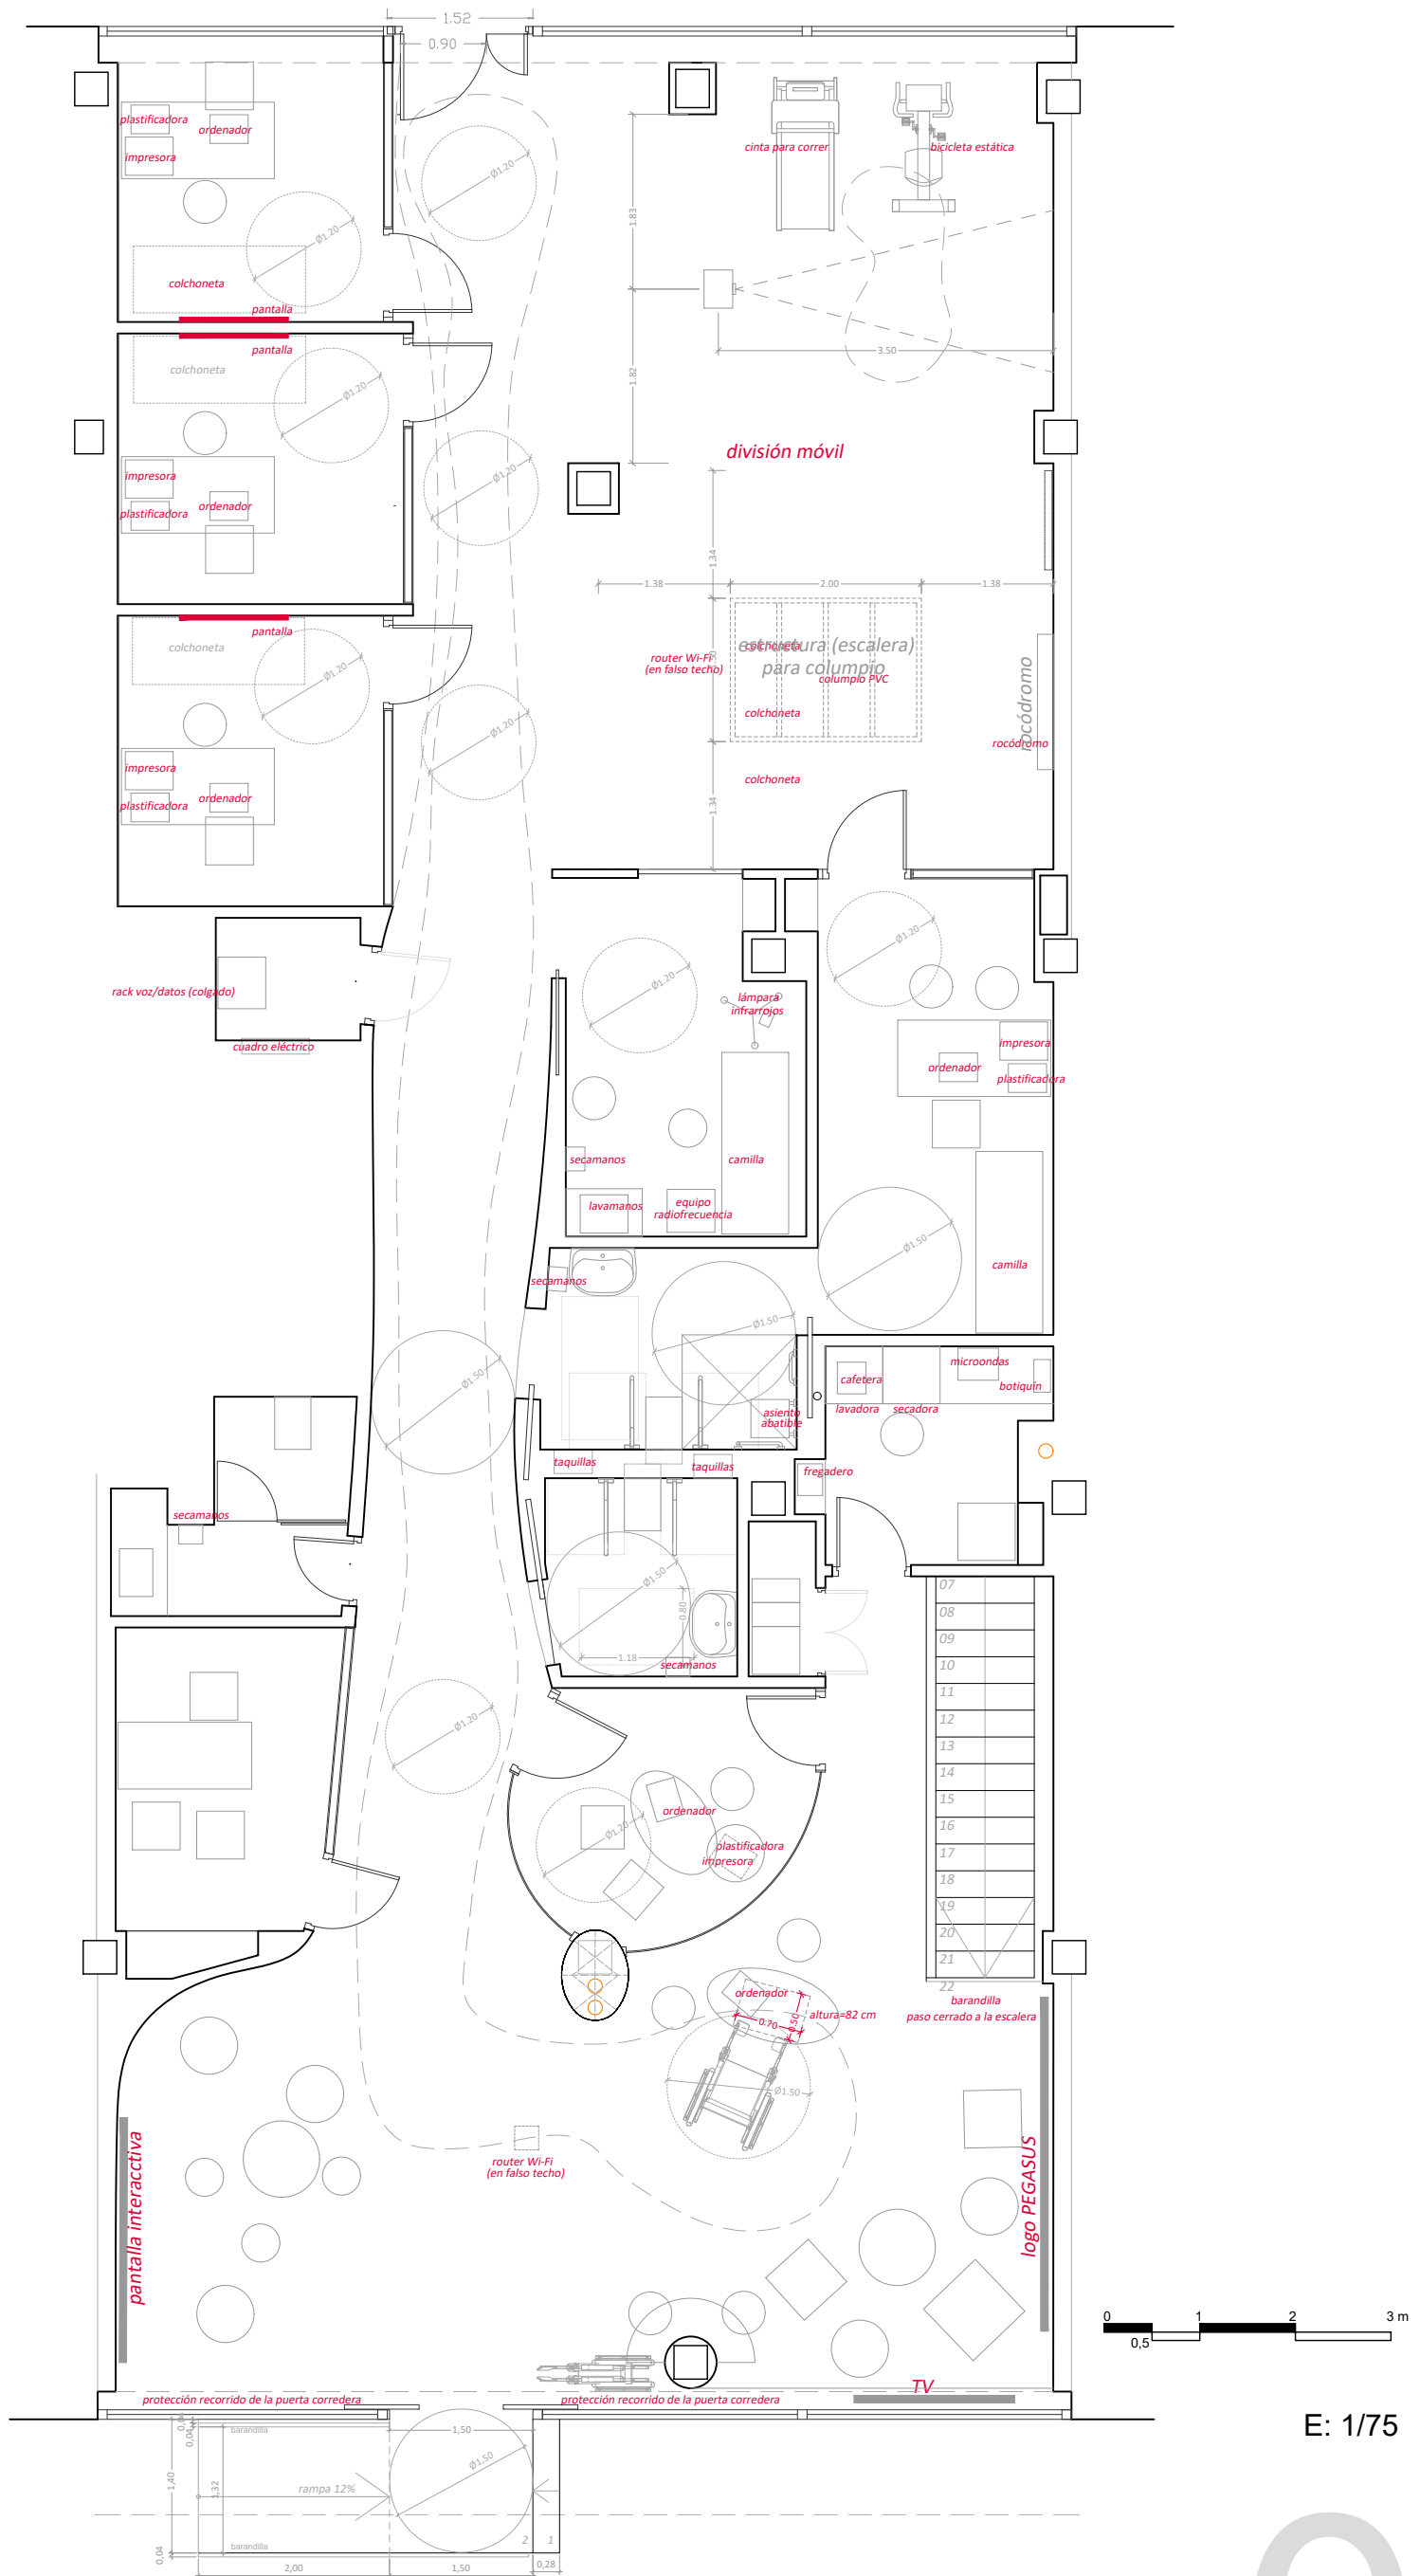

E: 1/75



PEGASUS

REFORMA DE LOCAL PARA CENTRO DE REHABILITACIÓN EN AVDA. DE VALDEARGANDA, 2, ARGANDA DEL REY, MADRID (CP: 28500)

Arquitecto: Pablo Mosquera de Arancibia Con el patrocinio de:

eduetrade


fecha: 27/11/2023

colegiado COAM, nº: 11.444

FASE: DIRECCIÓN DE OBRA-CERTIFICADO FINAL DE OBRA

PLANTA BAJA: EQUIPAMIENTO

07

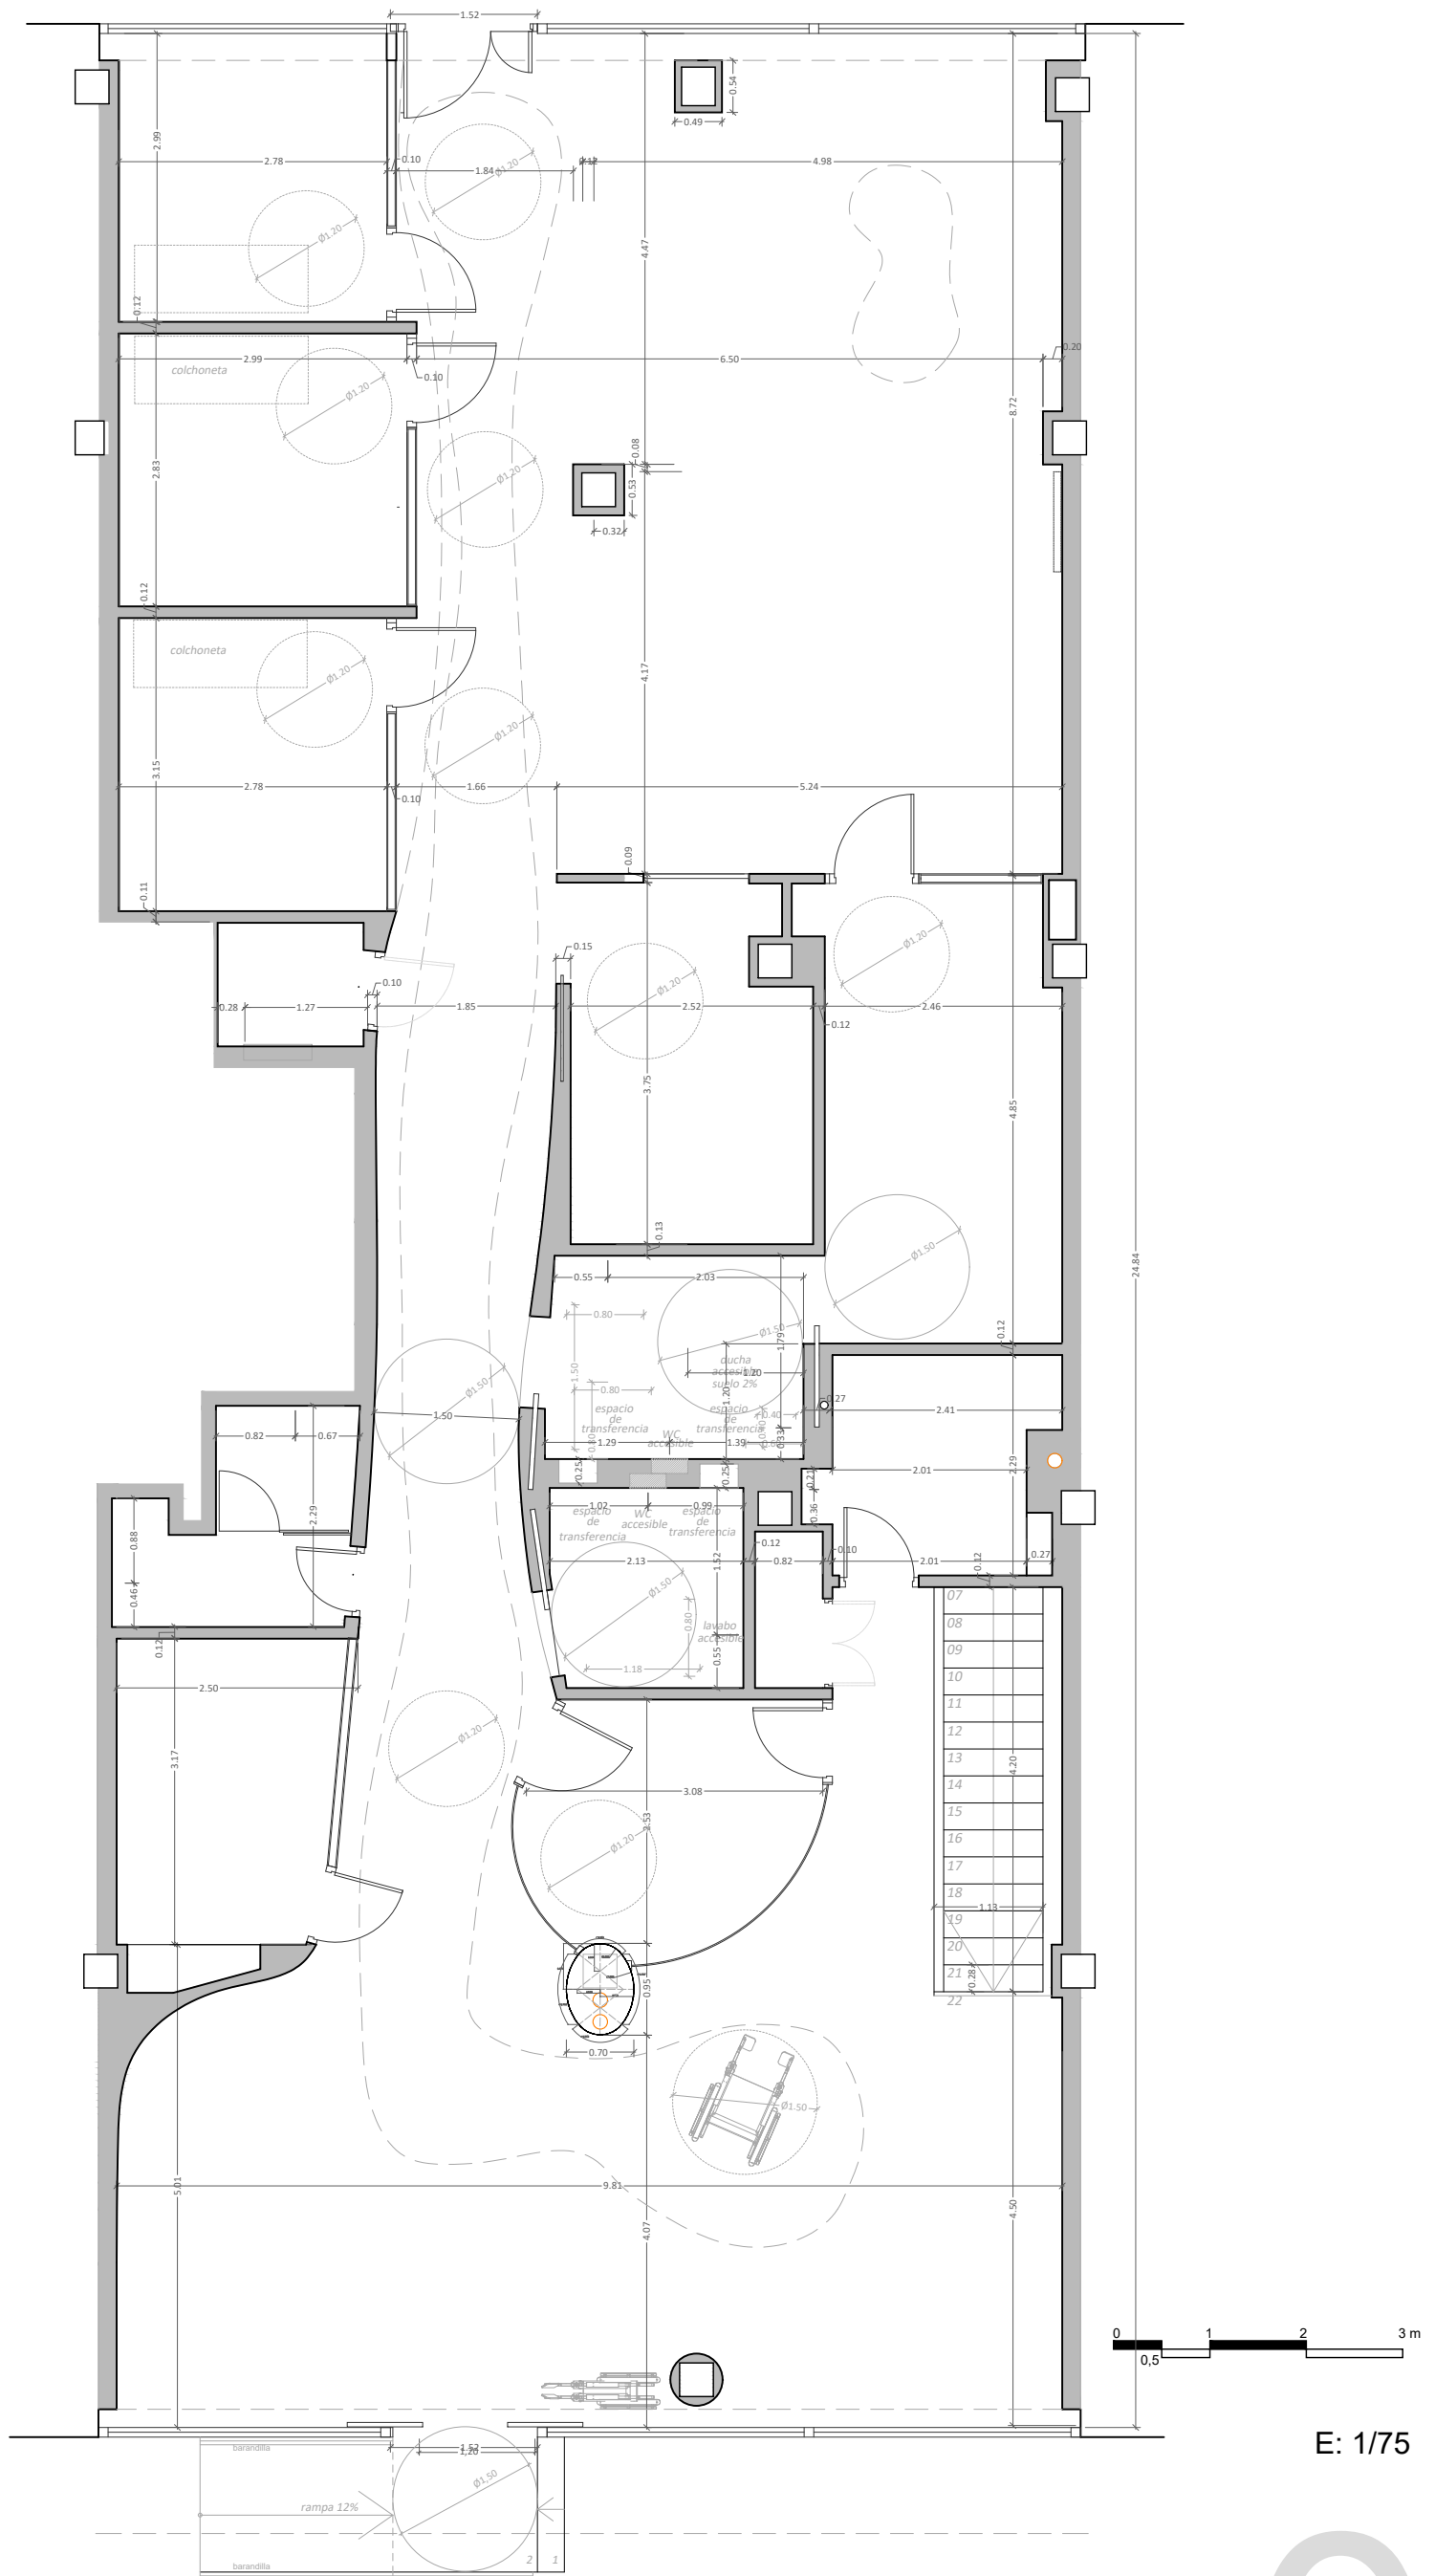

E: 1/75



PEGASUS

REFORMA DE LOCAL PARA CENTRO DE REHABILITACIÓN EN AVDA. DE VALDEARGANDA, 2, ARGANDA DEL REY, MADRID (CP: 28500)

Arquitecto: Pablo Mosquera de Arancibia Con el patrocinio de:

edutrade


fecha: 27/11/2023

colegiado COAM, nº: 11.444

PLANTA BAJA: COTAS

08

FASE: DIRECCIÓN DE OBRA-CERTIFICADO FINAL DE OBRA

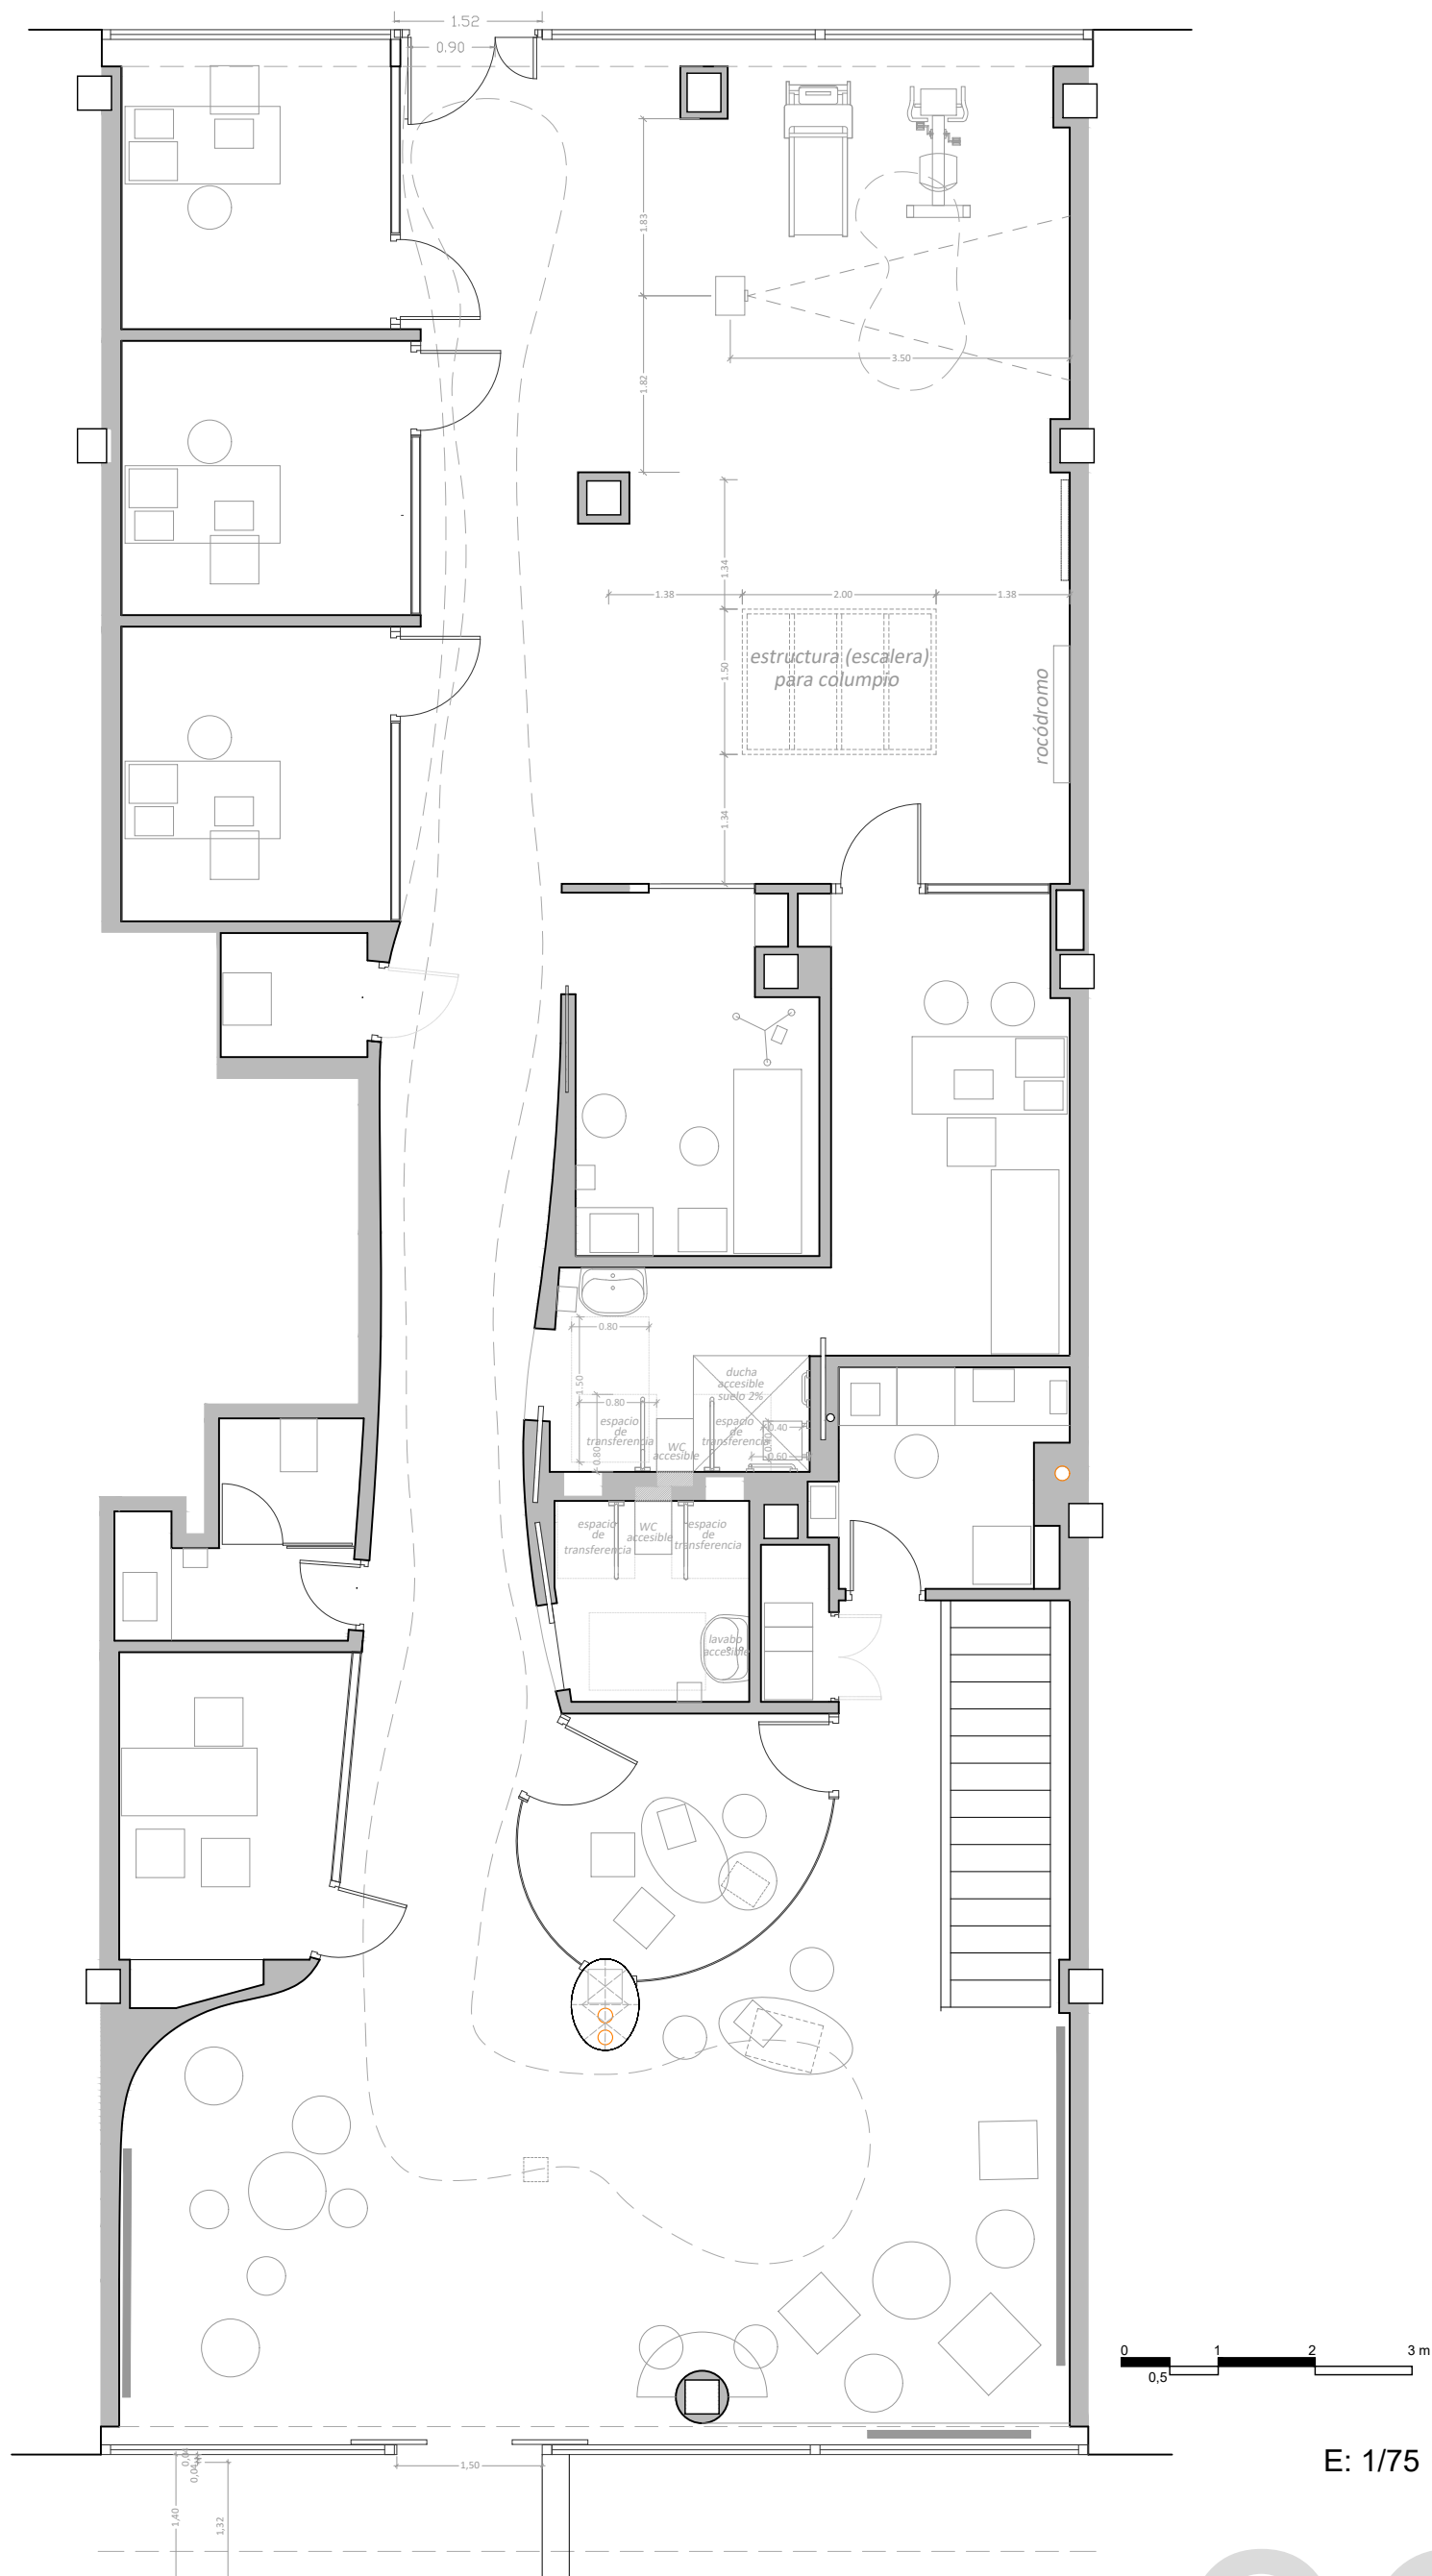

PLANTA BAJA: COTAS (acotación a ejes de sanitarios)

FASE: DIRECCIÓN DE OBRA-CERTIFICADO FINAL DE OBRA

REFORMA DE LOCAL PARA CENTRO DE REHABILITACIÓN EN AVDA. DE VALDEARGANDA, 2, ARGANDA DEL REY, MADRID (CP: 28500)


Arquitecto: Pablo Mosquera de Arancibia Con el patrocinio de: **edutrade** fecha: 27/11/2023

colegiado COAM, nº: 11.444



PEGASUS

09

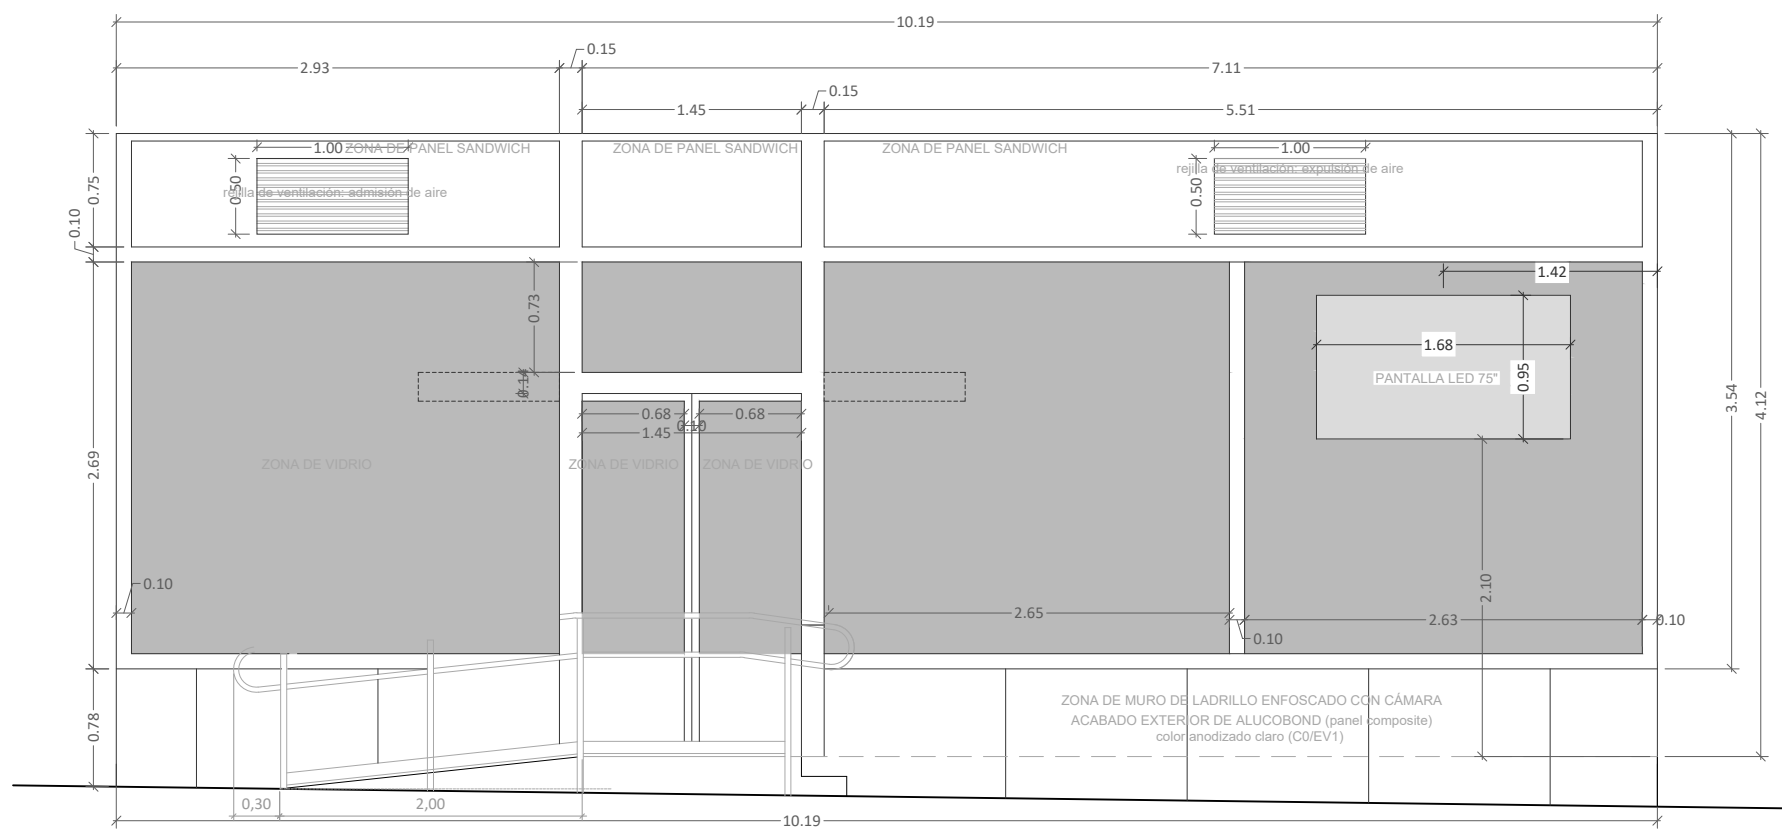

FACHADA PRINCIPAL (Oeste)



ACCESO Y FACHADA PRINCIPAL



PEGASUS

REFORMA DE LOCAL PARA CENTRO DE REHABILITACIÓN EN AVDA. DE VALDEARGANDA, 2, ARGANDA DEL REY, MADRID (CP: 28500)

Arquitecto: Pablo Mosquera de Arancibia Con el patrocinio de:

edutrade


fecha: 27/11/2023

colegiado COAM, nº: 11.444

ALZADO PRINCIPAL : ESTADO REFORMADO

FASE: DIRECCIÓN DE OBRA-CERTIFICADO FINAL DE OBRA

10

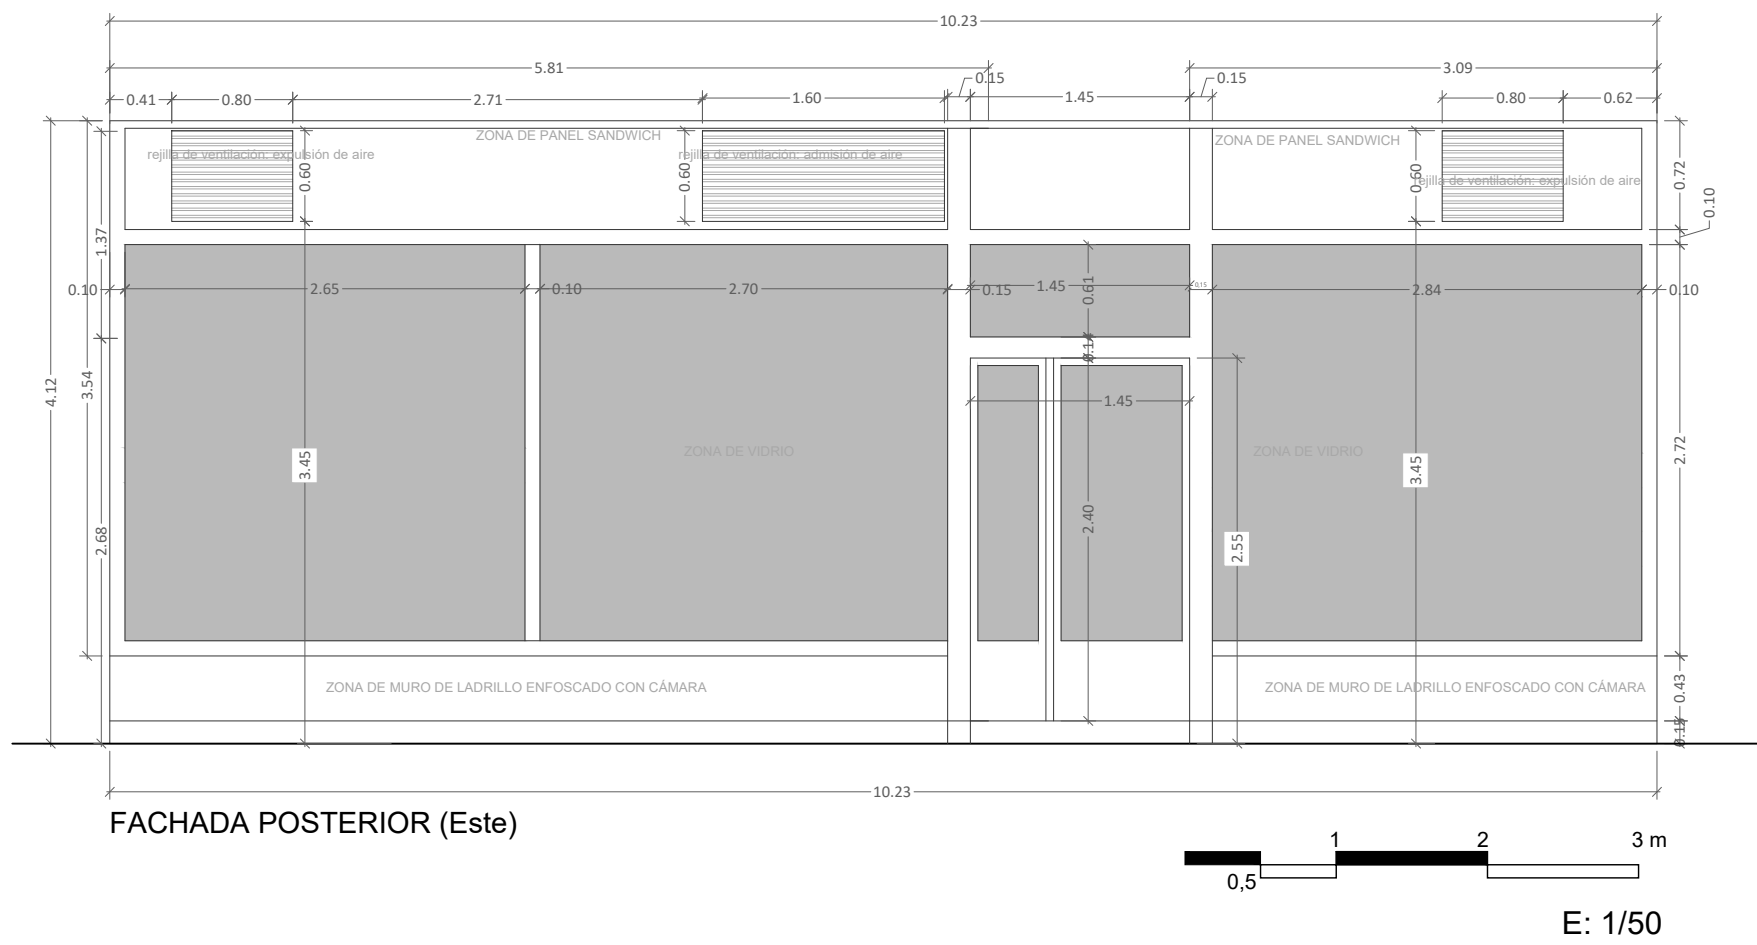

ASPECTO GENERAL Y DE DETALLE DE LA FACHADA POSTERIOR.



PEGASUS

REFORMA DE LOCAL PARA CENTRO DE REHABILITACIÓN EN AVDA. DE VALDEARGANDA, 2, ARGANDA DEL REY, MADRID (CP: 28500)

Arquitecto: Pablo Mosquera de Arancibia Con el patrocinio de:

eductrade





fecha: 27/11/2023



11

ALZADO POSTERIOR: ESTADO REFORMADO

FASE: DIRECCIÓN DE OBRA-CERTIFICADO FINAL DE OBRA

colegiado COAM, nº: 11.444

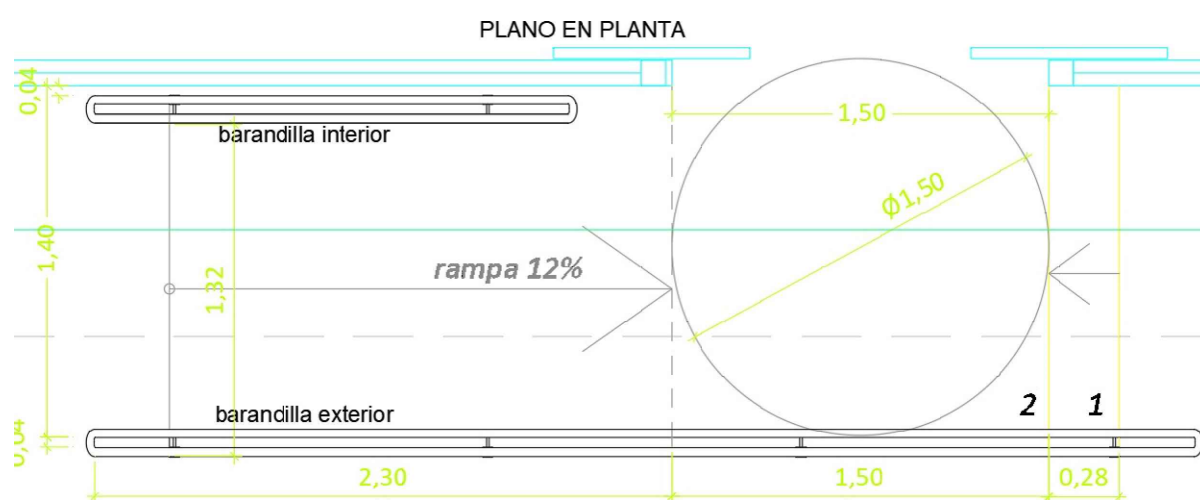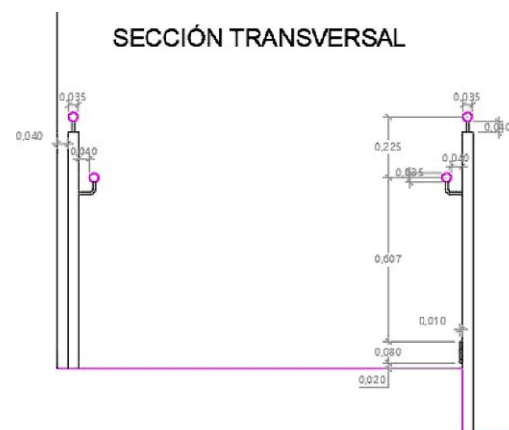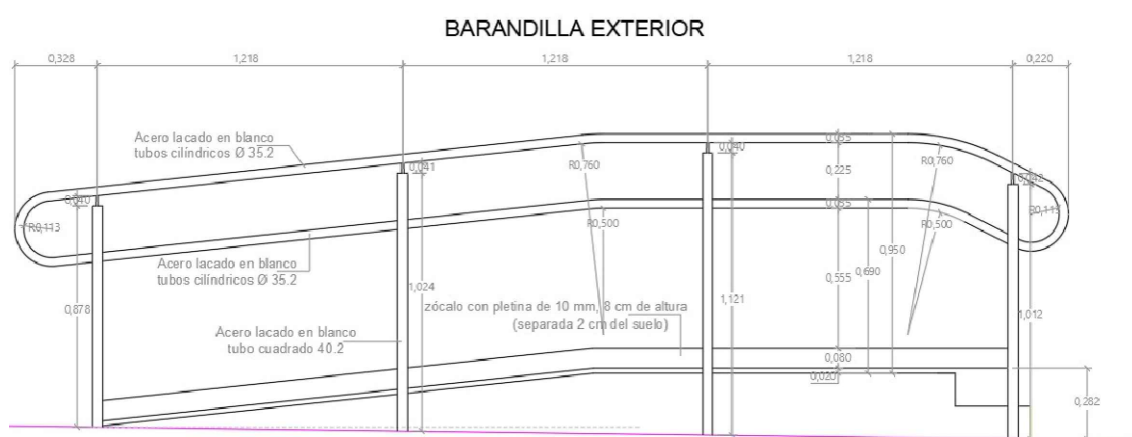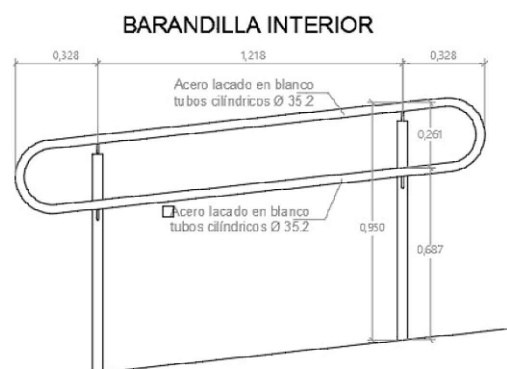

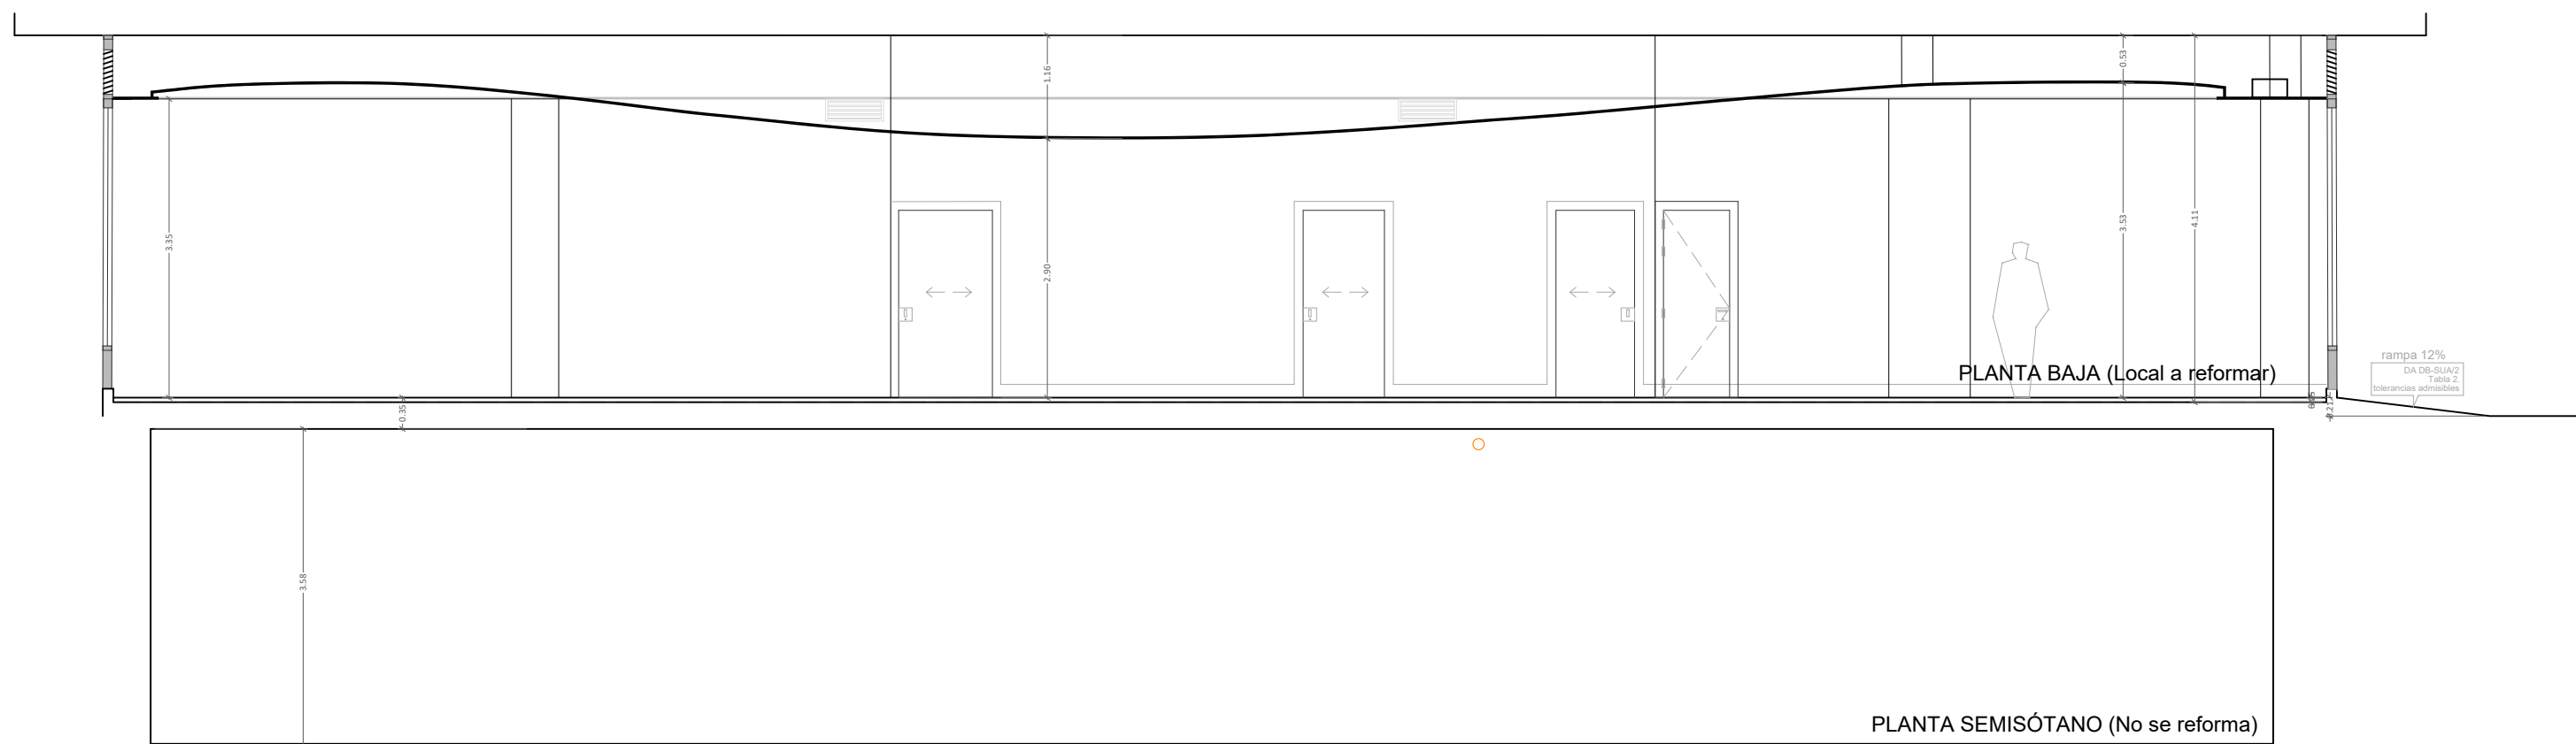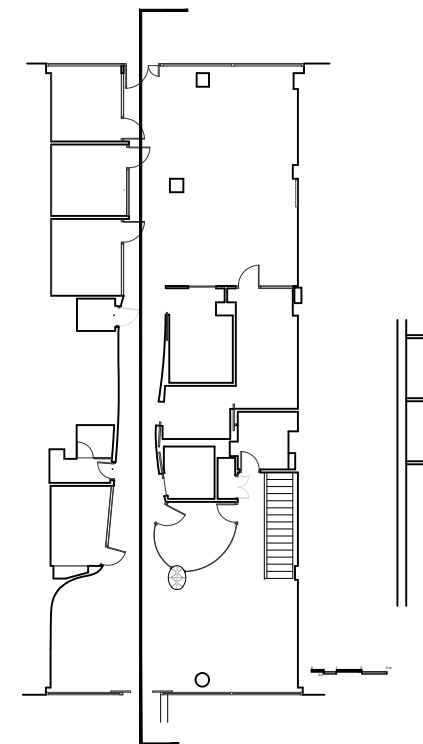

PEGASUS

REFORMA DE LOCAL PARA CENTRO DE REHABILITACIÓN EN AVDA. DE VALDEARGANDA, 2, ARGANDA DEL REY, MADRID (CP: 28500)

Arquitecto: Pablo Mosquera de Arancibia Con el patrocinio de:

colegiado COAM, nº: 11.444

educetrade


fecha: 27/11/2023

SECCIÓN LONGITUDINAL POR PASILLO: ESTADO REFORMADO

FASE: DIRECCIÓN DE OBRA-CERTIFICADO FINAL DE OBRA

E: 1/75

13

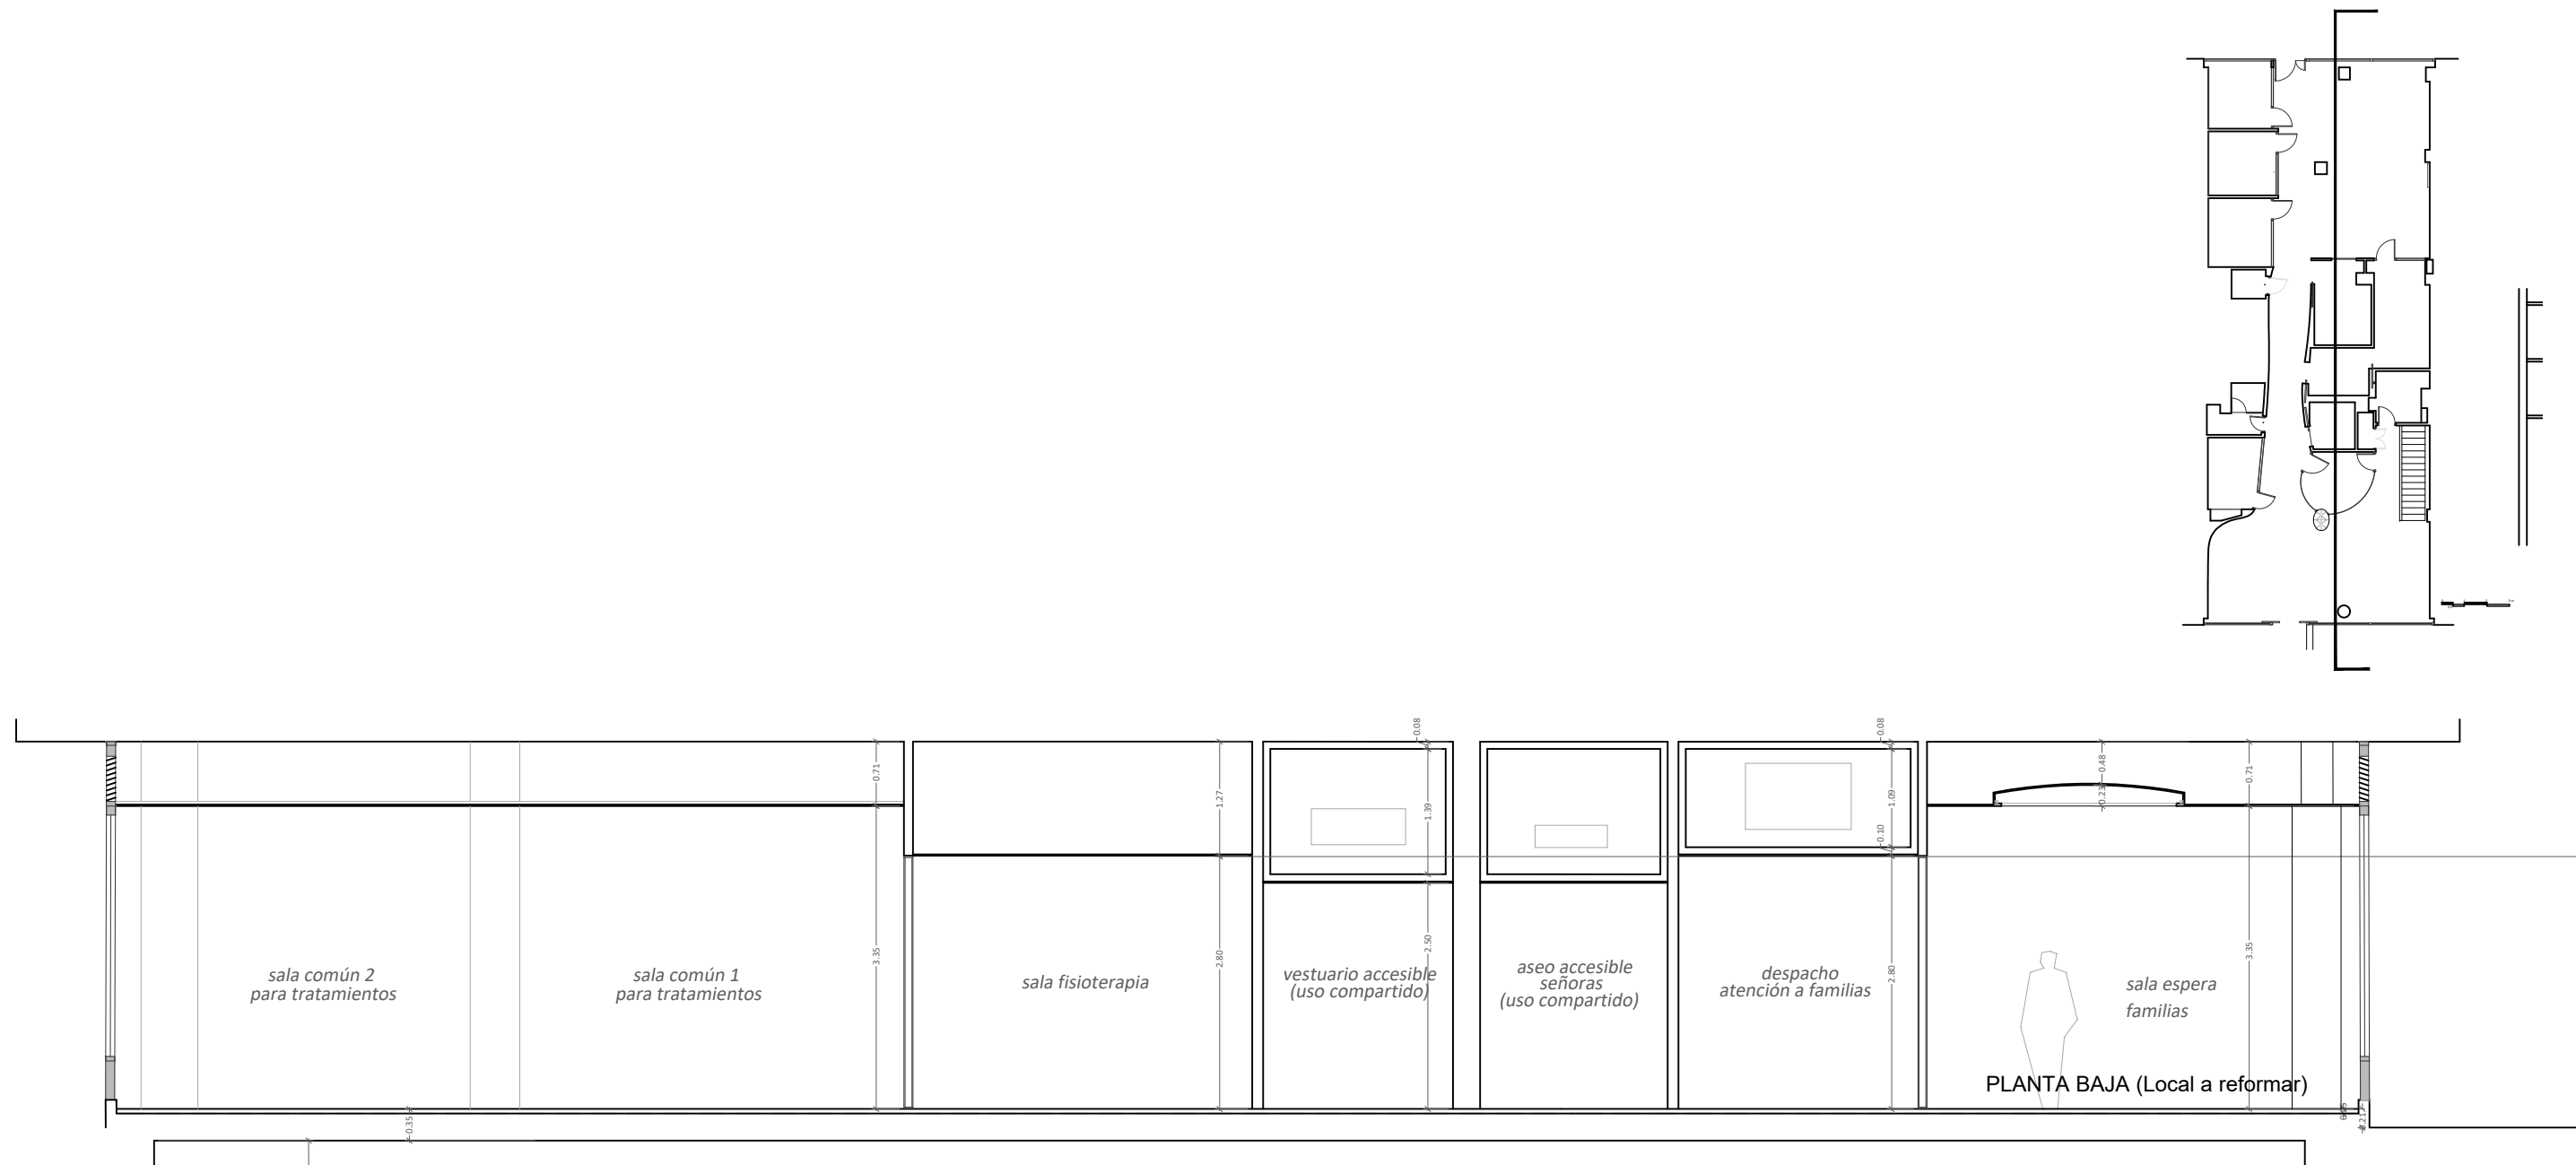

E: 1/75



PEGASUS

REFORMA DE LOCAL PARA CENTRO DE REHABILITACIÓN EN AVDA. DE VALDEARGANDA, 2, ARGANDA DEL REY, MADRID (CP: 28500)

Arquitecto: Pablo Mosquera de Arancibia Con el patrocinio de:

colegiado COAM, nº: 11.444



SECCIÓN LONGITUDINAL POR ASEOS: ESTADO REFORMADO

FASE: DIRECCIÓN DE OBRA-CERTIFICADO FINAL DE OBRA

eductrade

fecha: 27/11/2023

14

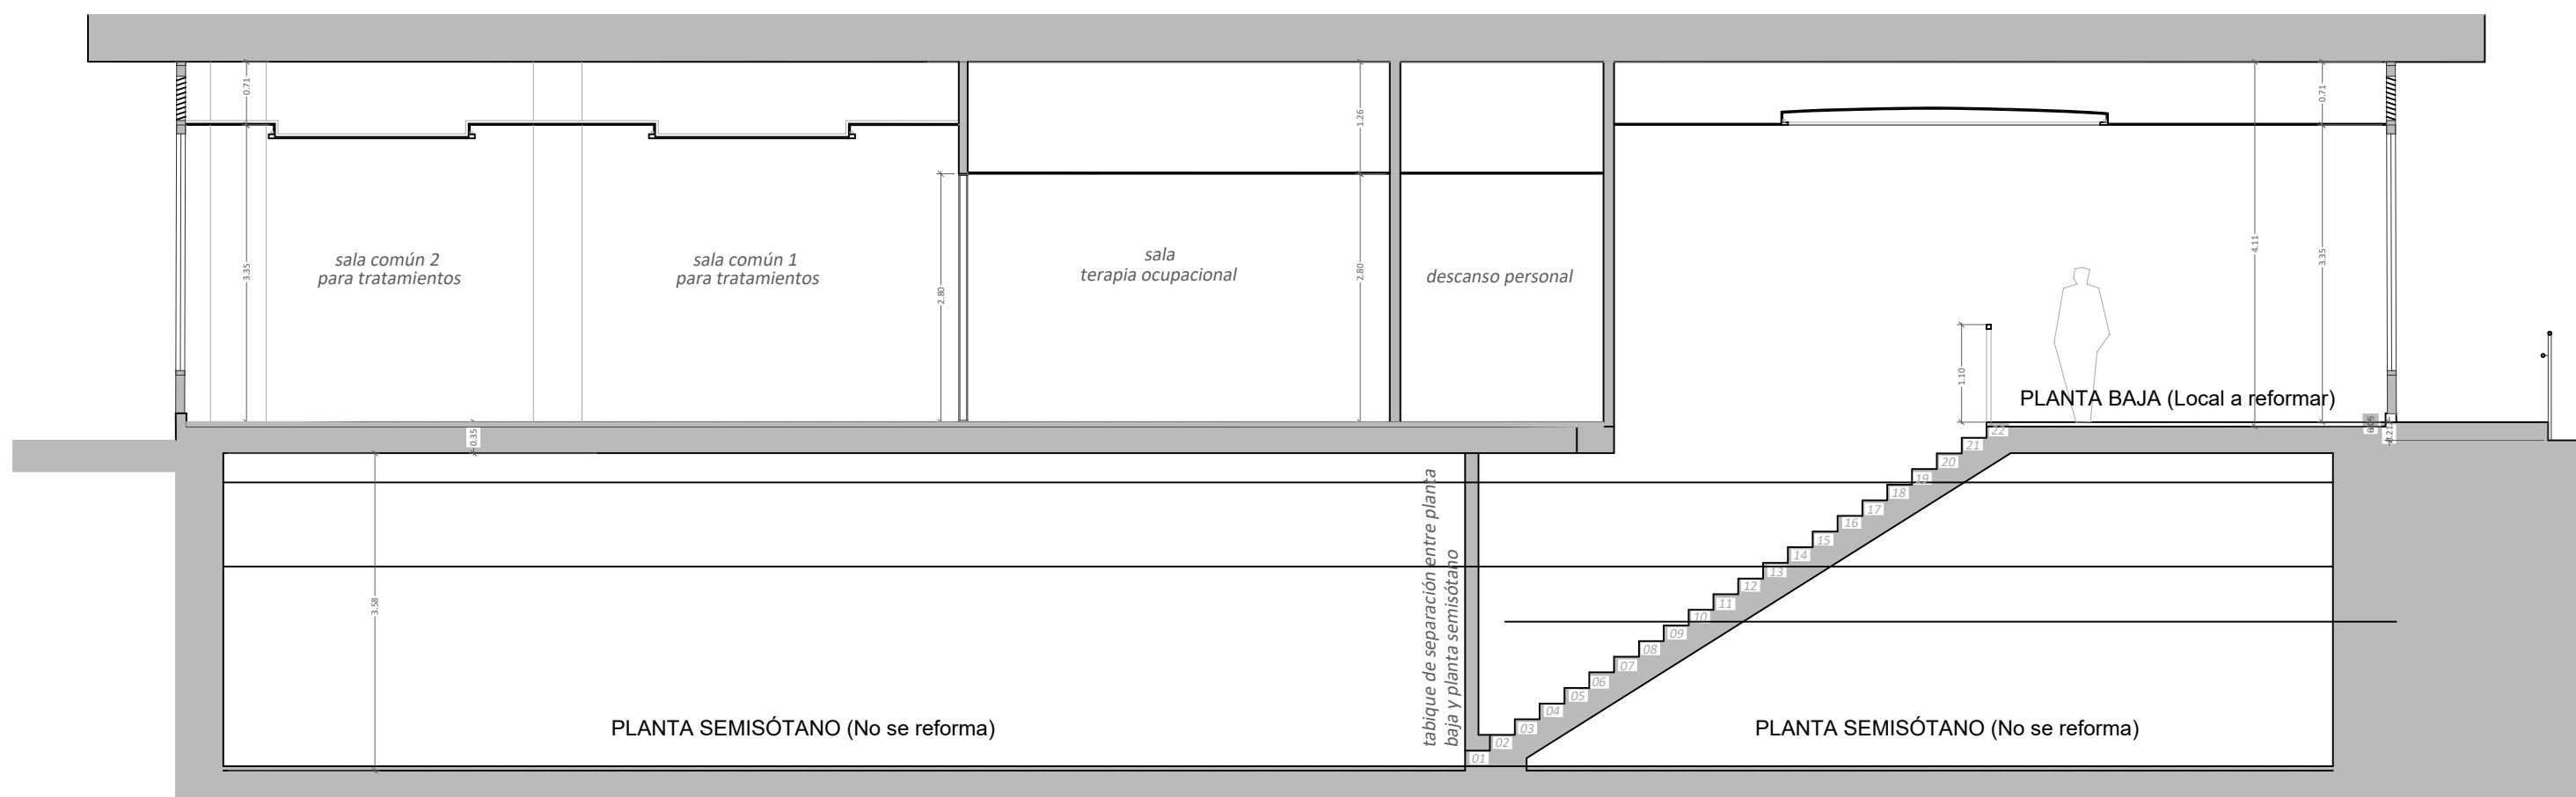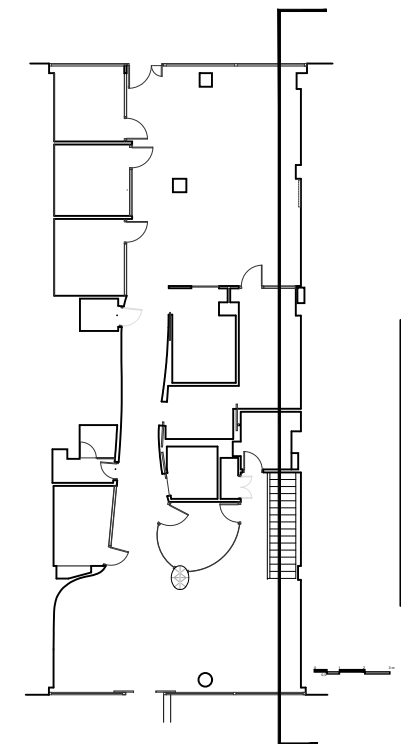

E: 1/75 0 0,5 1 2 3m



PEGASUS

REFORMA DE LOCAL PARA CENTRO DE REHABILITACIÓN EN AVDA. DE VALDEARGANDA, 2, ARGANDA DEL REY, MADRID (CP: 28500)

Arquitecto: Pablo Mosquera de Arancibia Con el patrocinio de:

colegiado COAM, nº: 11.444


educetrade

fecha: 27/11/2023


SECCIÓN LONGITUDINAL POR SALAS DE TRATAMIENTOS: ESTADO REFORMADO

FASE: DIRECCIÓN DE OBRA-CERTIFICADO FINAL DE OBRA

15

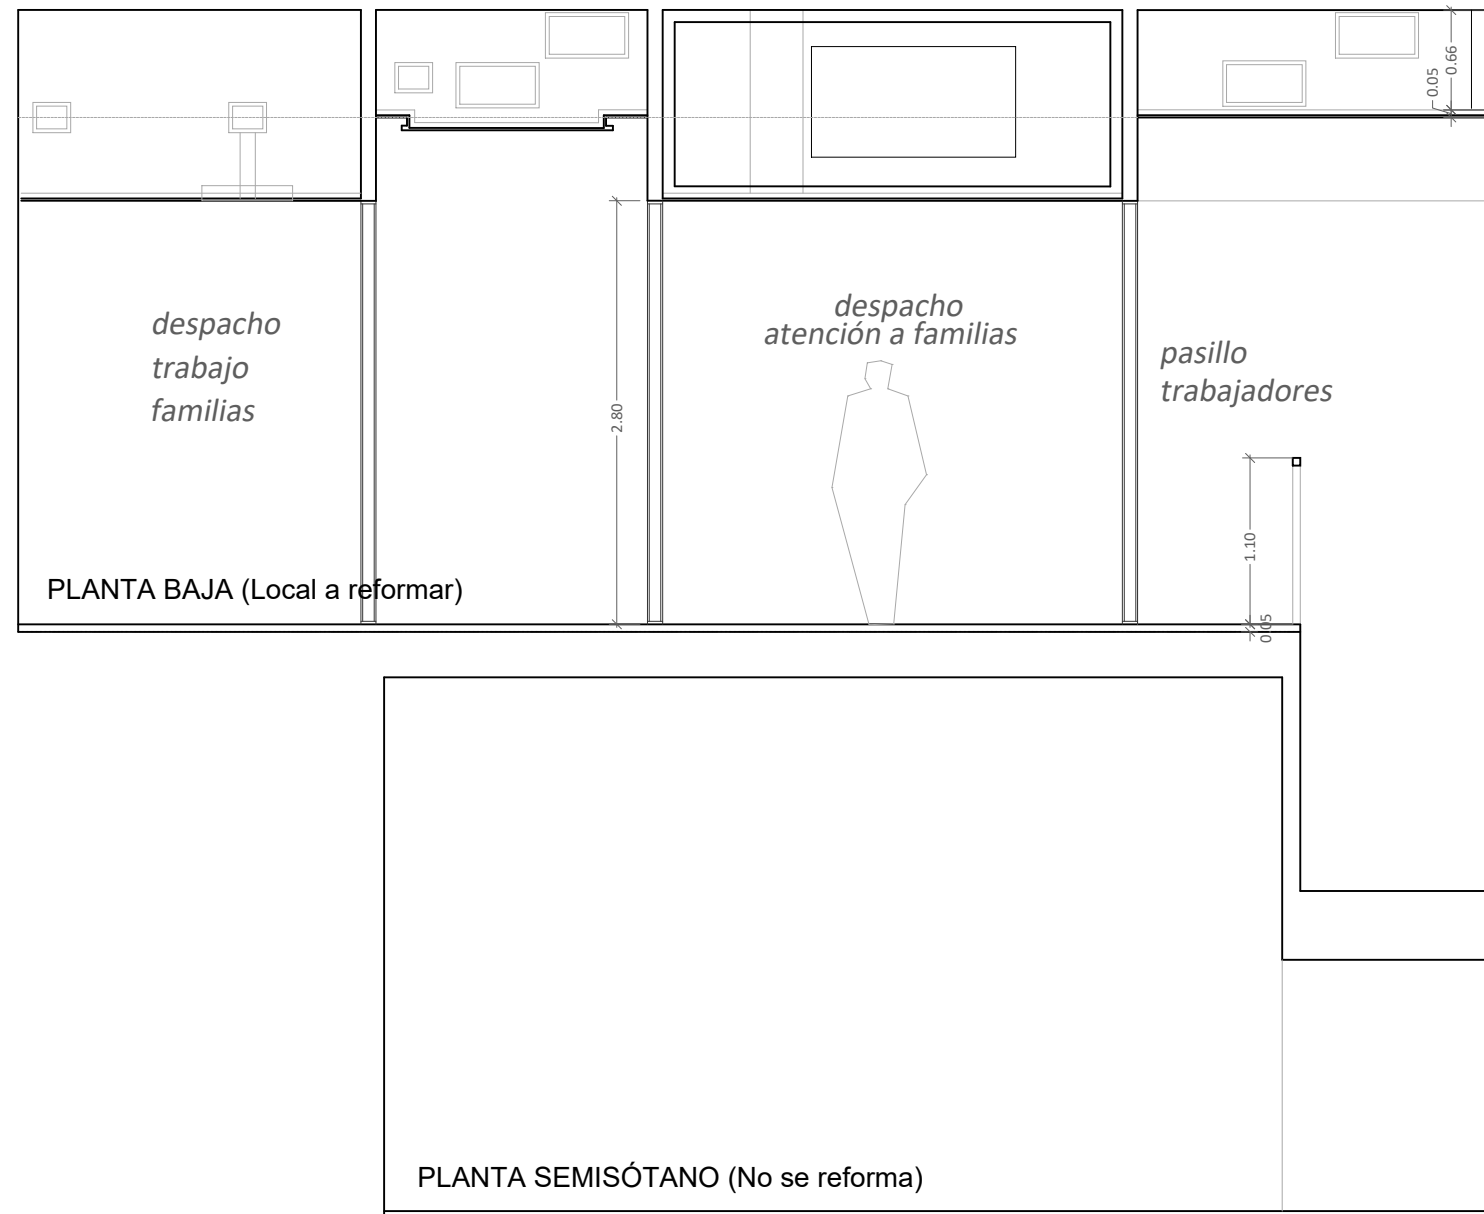

0 0,5 1 m
SECCIÓN A-A'

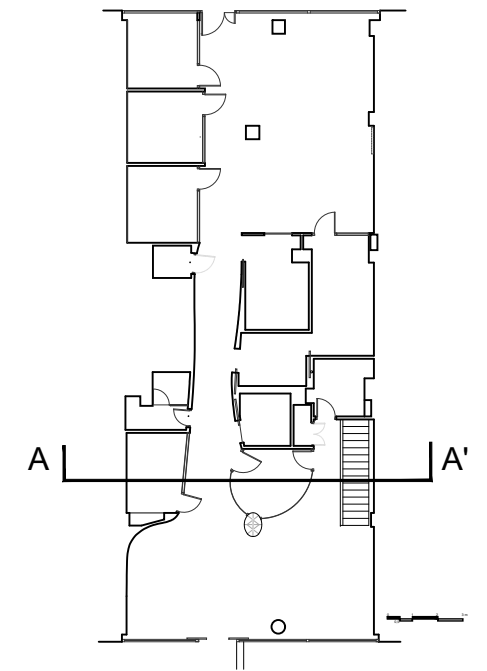

E: 1/50



PEGASUS

REFORMA DE LOCAL PARA CENTRO DE REHABILITACIÓN EN AVDA. DE VALDEARGANDA, 2, ARGANDA DEL REY, MADRID (CP: 28500)

Arquitecto: Pablo Mosquera de Arancibia Con el patrocinio de:

colegiado COAM, nº: 11.444


educetrade

fecha: 27/11/2023



SECCIÓN TRANSVERSAL POR PASILLO: ESTADO REFORMADO

FASE: DIRECCIÓN DE OBRA-CERTIFICADO FINAL DE OBRA

16

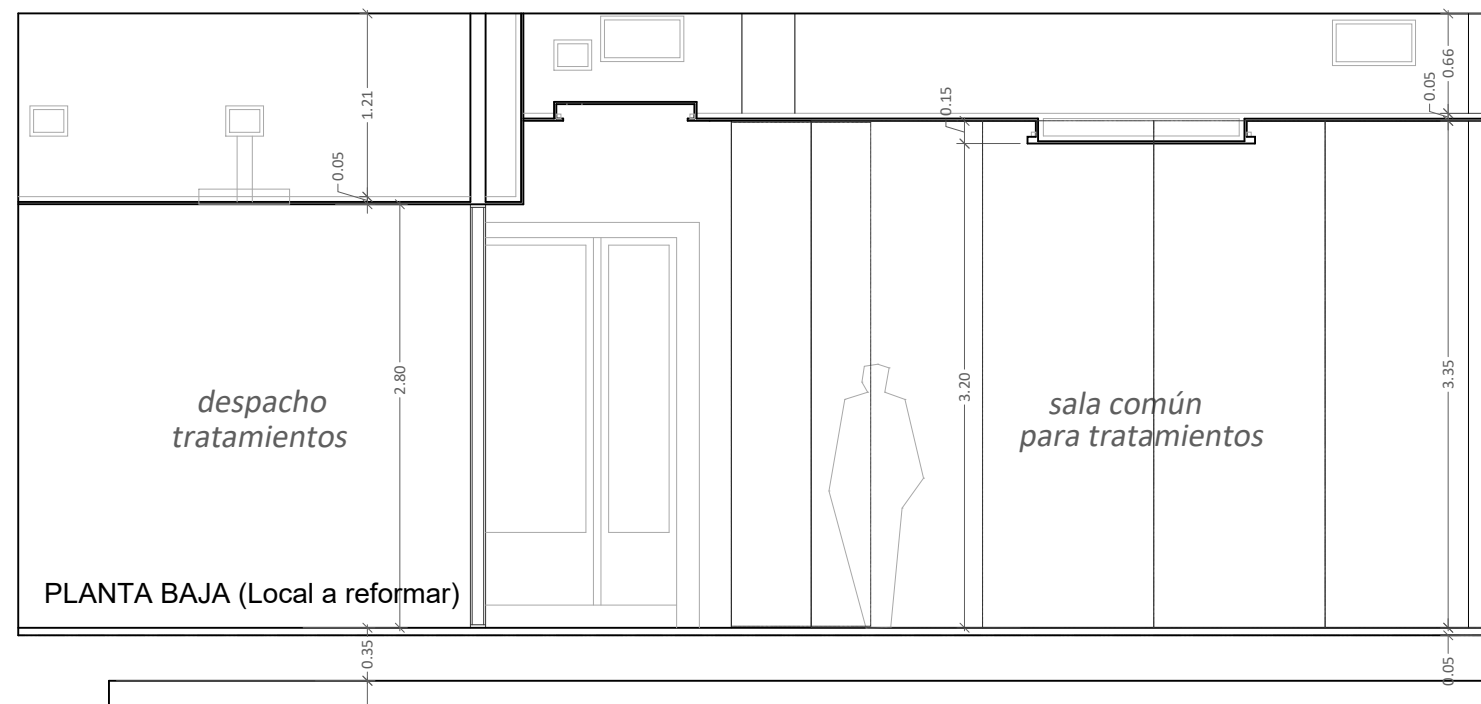

SECCIÓN B-B'

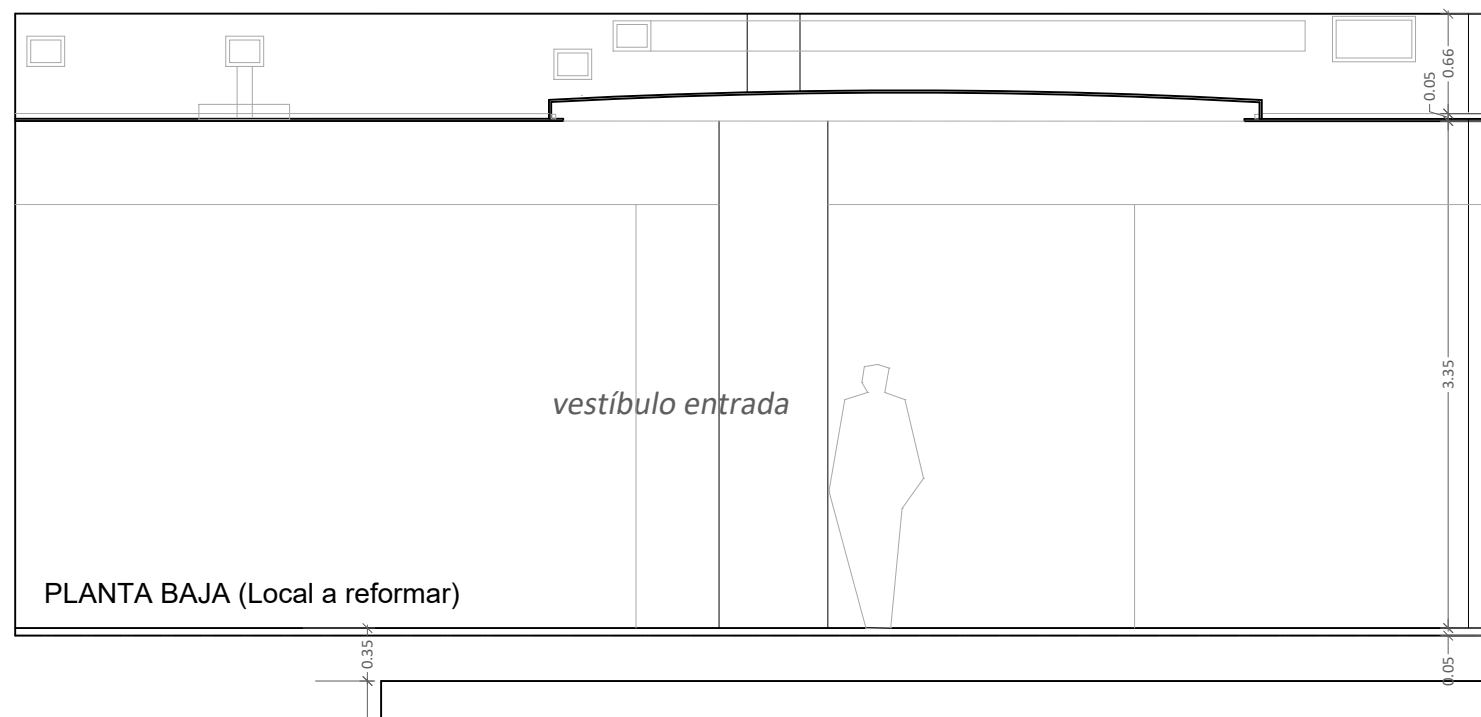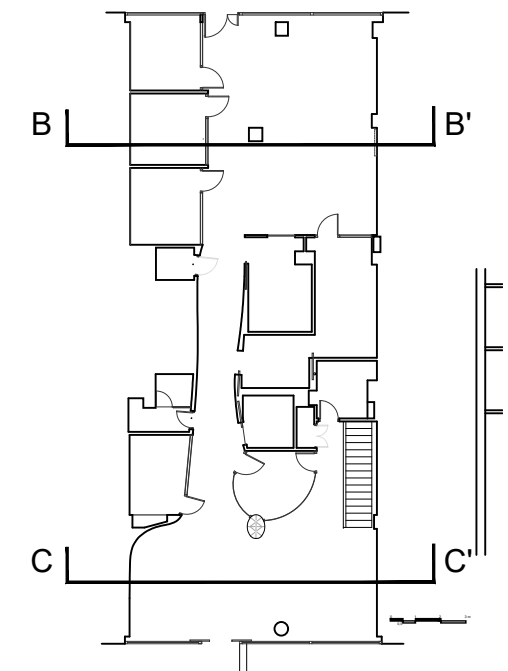

SECCIÓN C-C'

E: 1/50



PEGASUS

REFORMA DE LOCAL PARA CENTRO DE REHABILITACIÓN EN AVDA. DE VALDEARGANDA, 2, ARGANDA DEL REY, MADRID (CP: 28500)


Arquitecto: Pablo Mosquera de Arancibia Con el patrocinio de:

educetrade

colegiado COAM, nº: 11.444

fecha: 27/11/2023

17

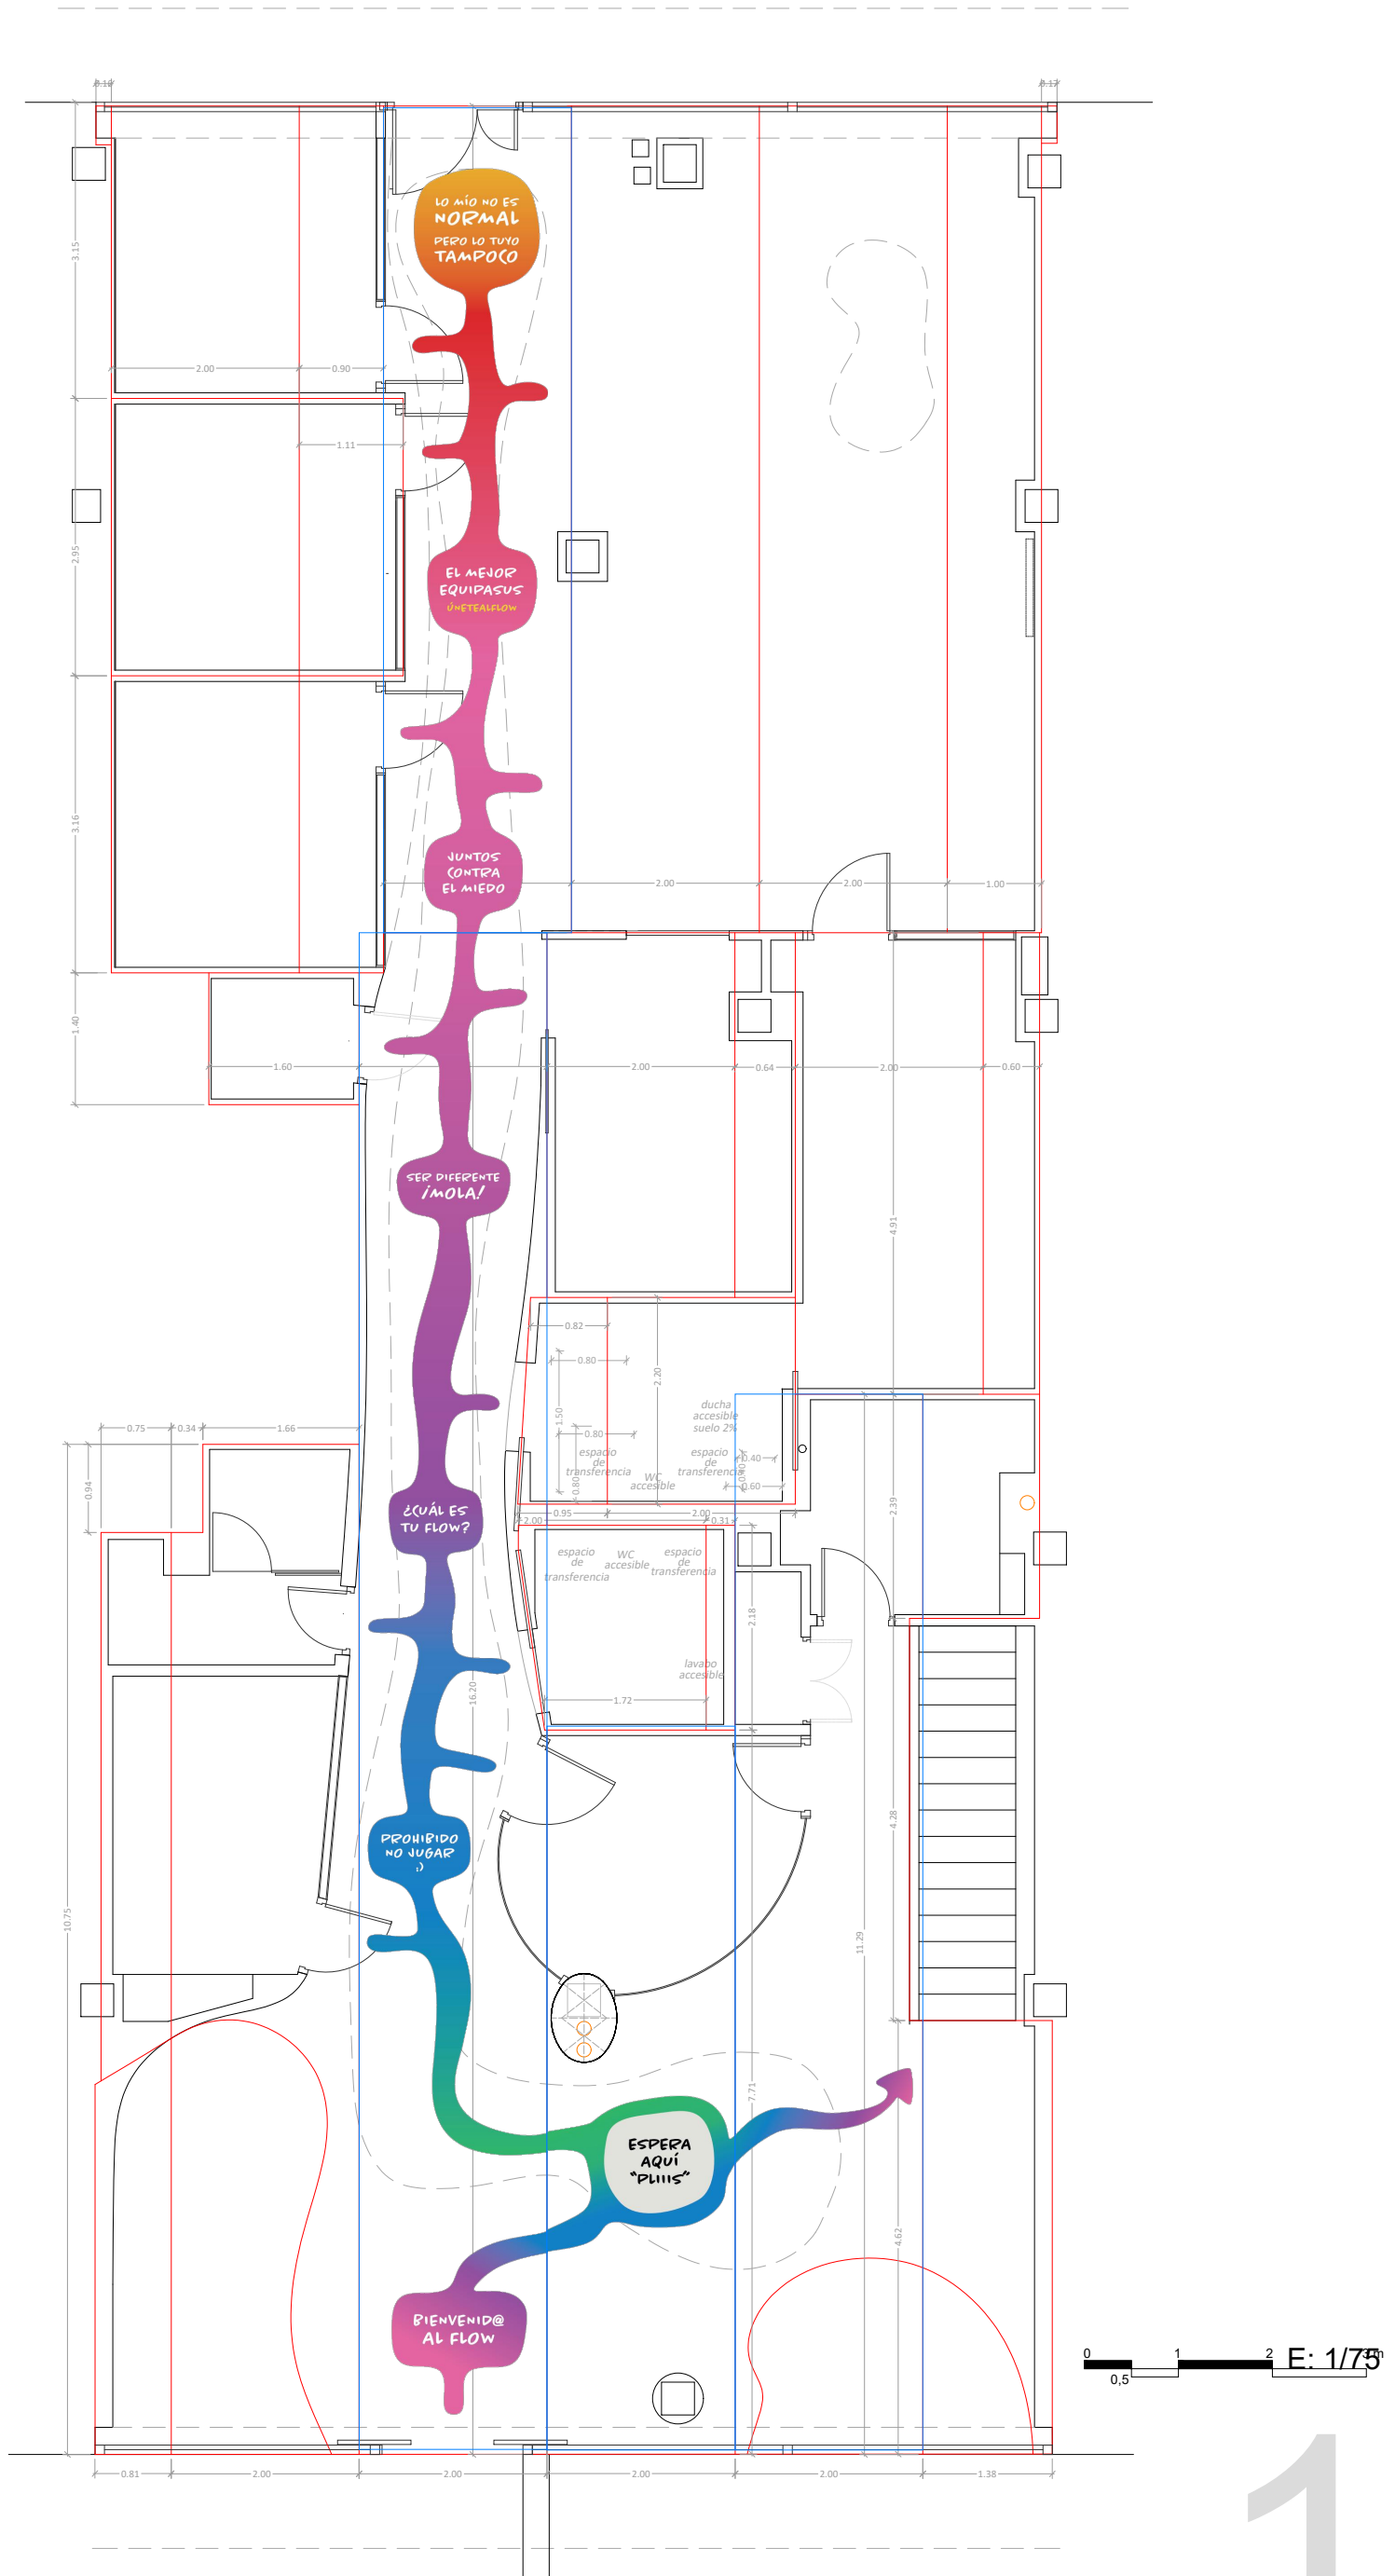

PLANTA BAJA: SUELOS



PEGASUS

REFORMA DE LOCAL PARA CENTRO DE REHABILITACIÓN EN AVDA. DE VALDEARGANDA, 2, ARGANDA DEL REY, MADRID (CP: 28500)


Arquitecto: Pablo Mosquera de Arancibia Con el patrocinio de:

eduētrade

fecha: 27/11/2023

colegiado COAM, nº: 11.444

FASE: DIRECCIÓN DE OBRA-CERTIFICADO FINAL DE OBRA

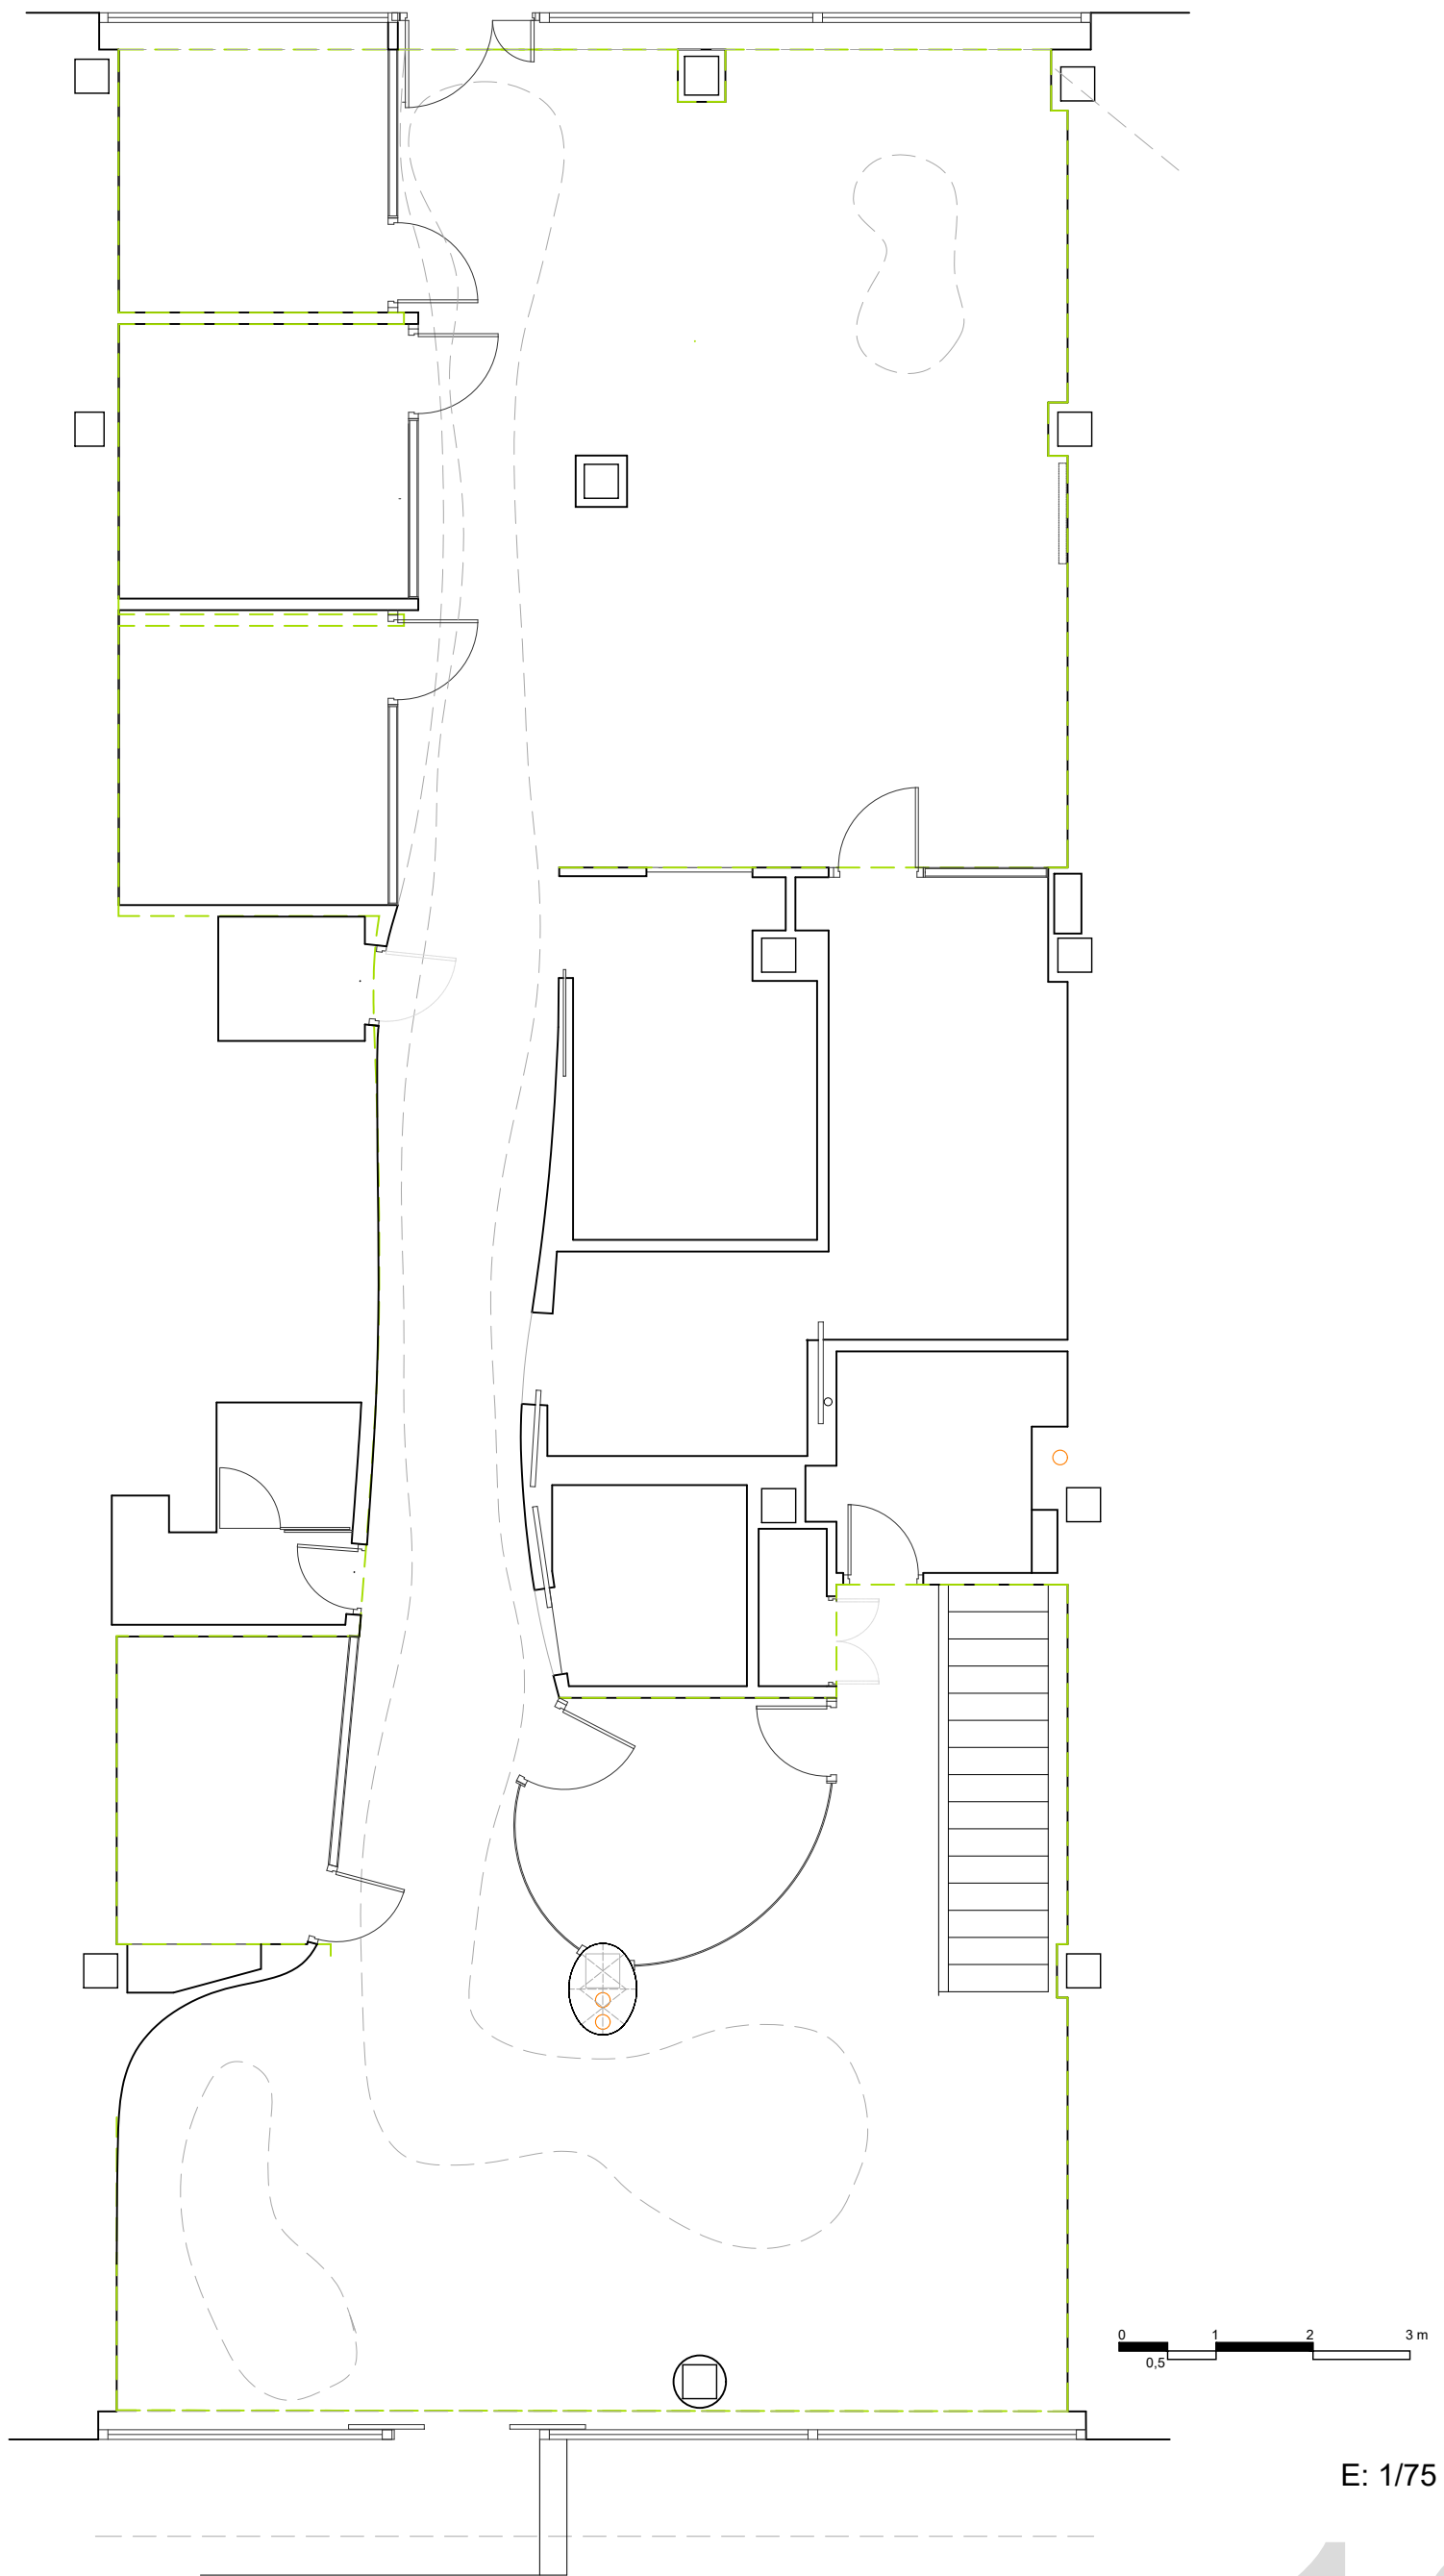

E: 1/75



PEGASUS

REFORMA DE LOCAL PARA CENTRO DE REHABILITACIÓN EN AVDA. DE VALDEARGANDA, 2, ARGANDA DEL REY, MADRID (CP: 28500)

Arquitecto: Pablo Mosquera de Arancibia Con el patrocinio de:


eduetrade

fecha: 27/11/2023

FASE: DIRECCIÓN DE OBRA-CERTIFICADO FINAL DE OBRA

PLANTA BAJA: TECHOS

19

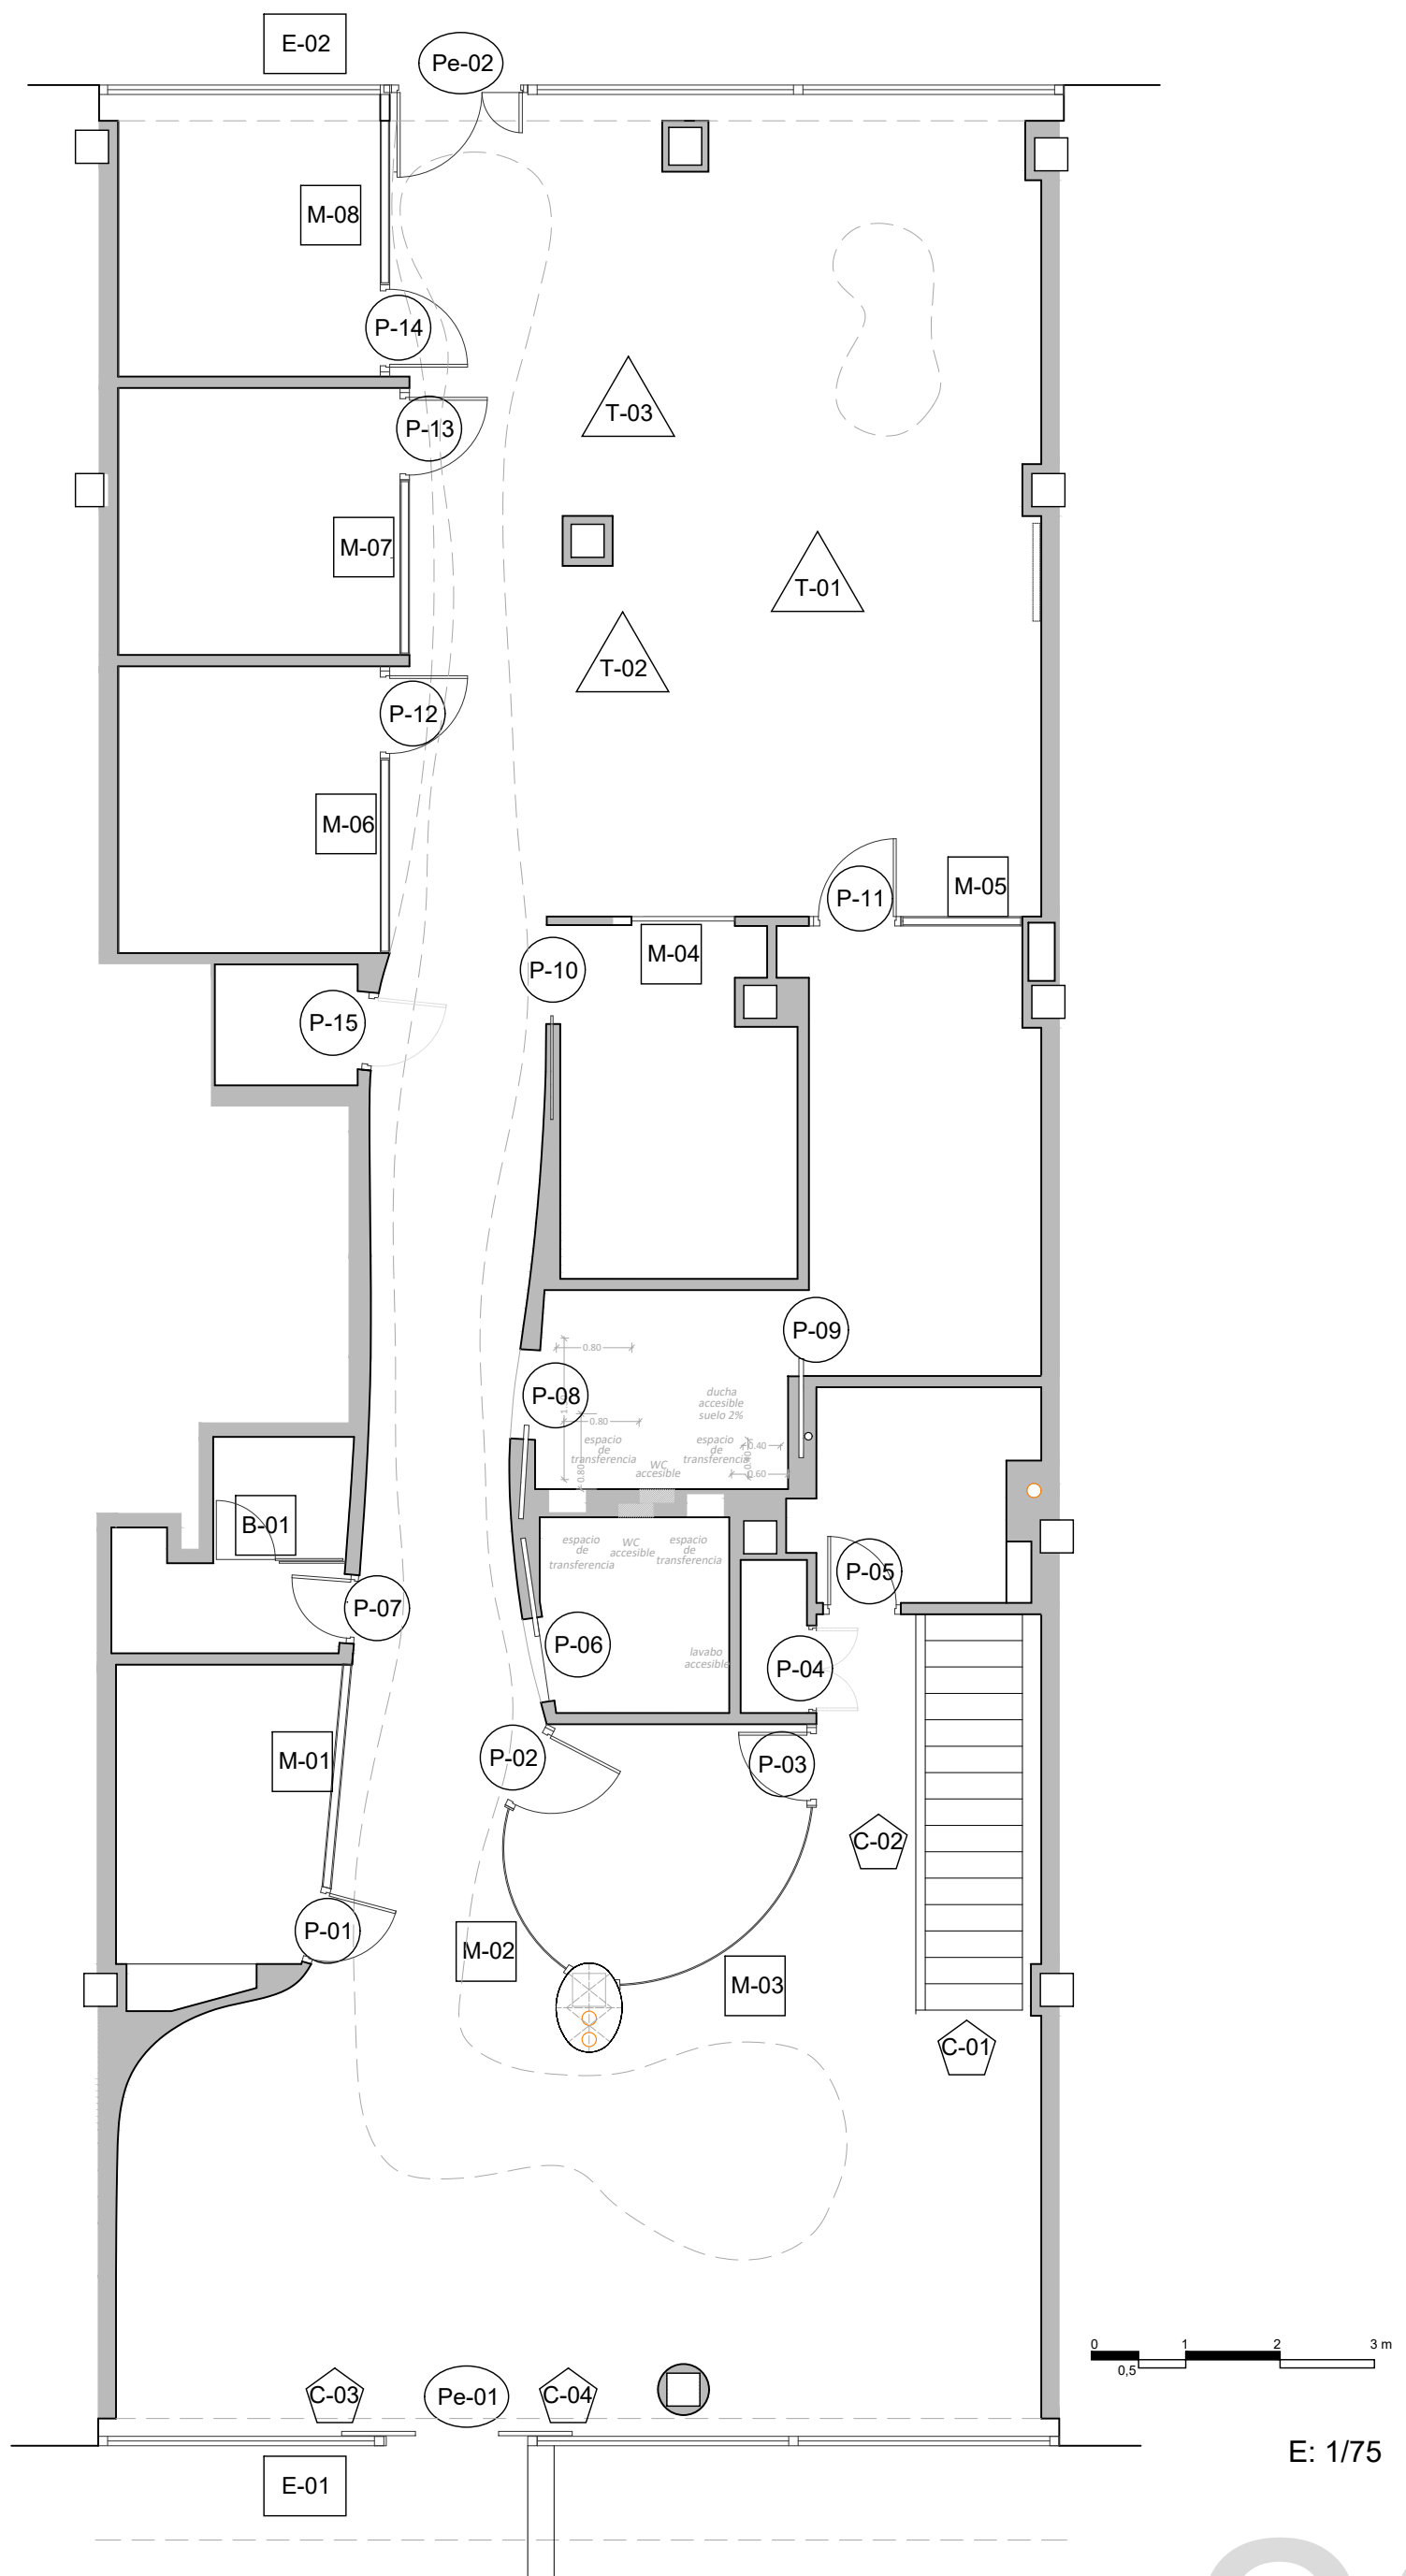

E: 1/75



PEGASUS

REFORMA DE LOCAL PARA CENTRO DE REHABILITACIÓN EN AVDA. DE VALDEARGANDA, 2, ARGANDA DEL REY, MADRID (CP: 28500)

Arquitecto: Pablo Mosquera de Arancibia Con el patrocinio de:


edustrade

fecha: 27/11/2023

FASE: DIRECCIÓN DE OBRA-CERTIFICADO FINAL DE OBRA

CARPINTERÍA: PLANTA

20

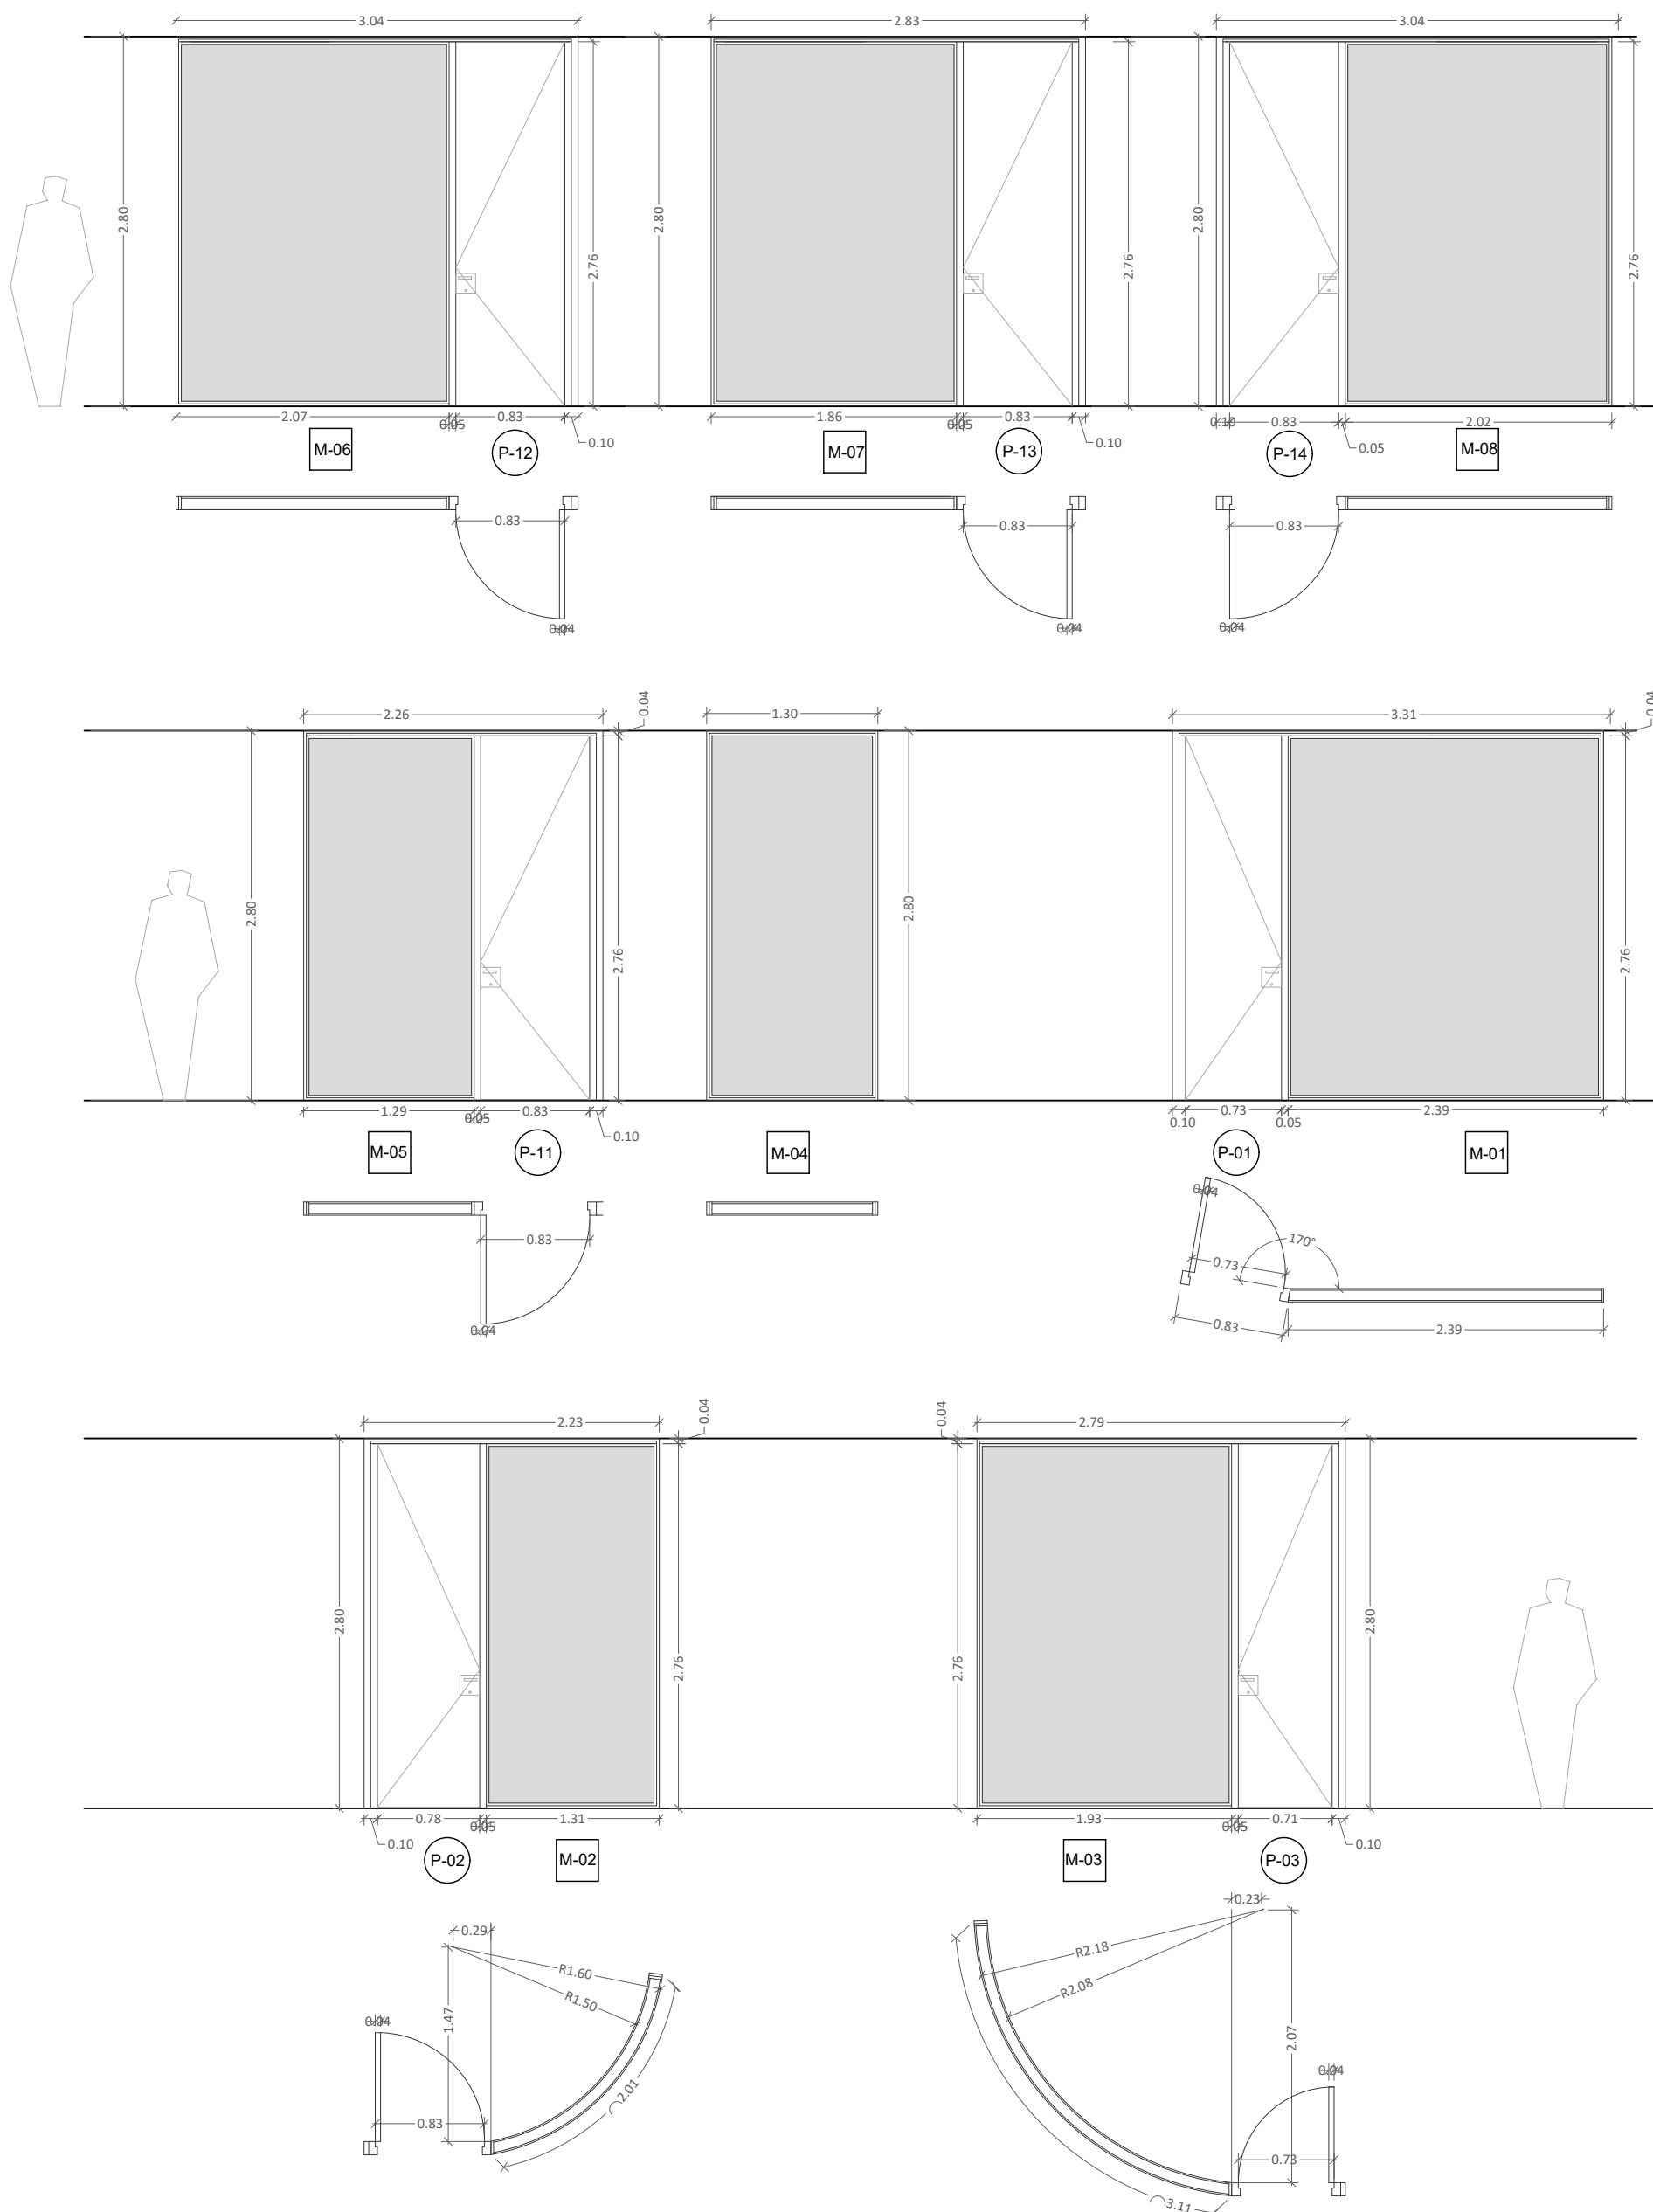

E: 1/50



PEGASUS

REFORMA DE LOCAL PARA CENTRO DE REHABILITACIÓN EN AVDA. DE VALDEARGANDA, 2, ARGANDA DEL REY, MADRID (CP: 28500)

Arquitecto: Pablo Mosquera de Arancibia Con el patrocinio de:

eduetrade




fecha: 27/11/2023


CARPINTERÍA: MAMPARAS

21

FASE: DIRECCIÓN DE OBRA-CERTIFICADO FINAL DE OBRA

colegiado COAM, nº: 11.444

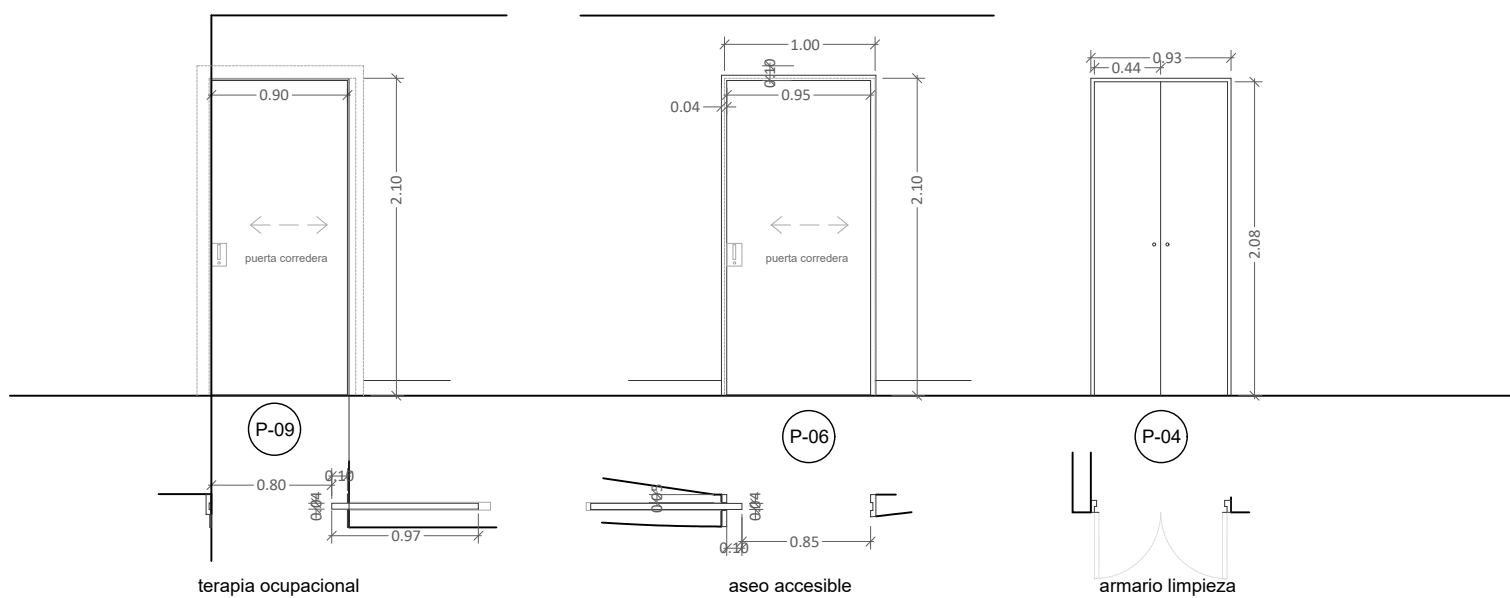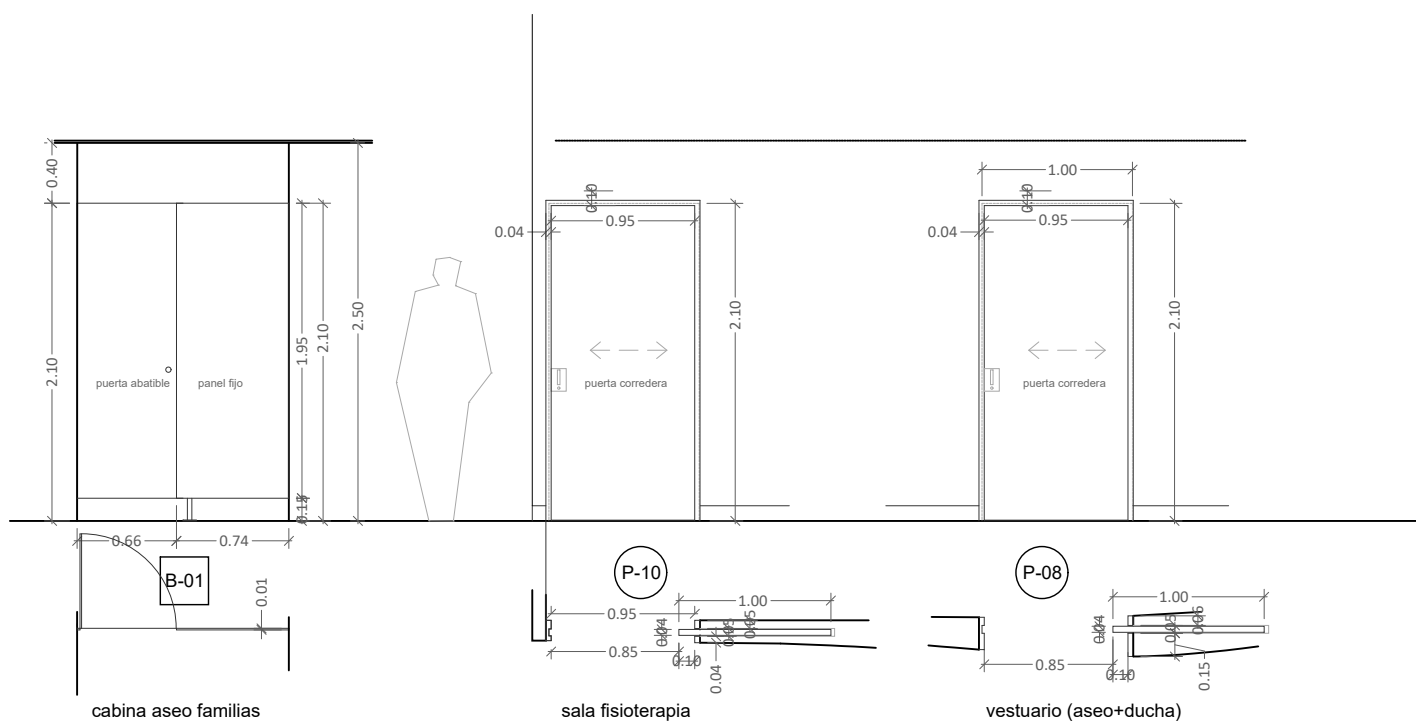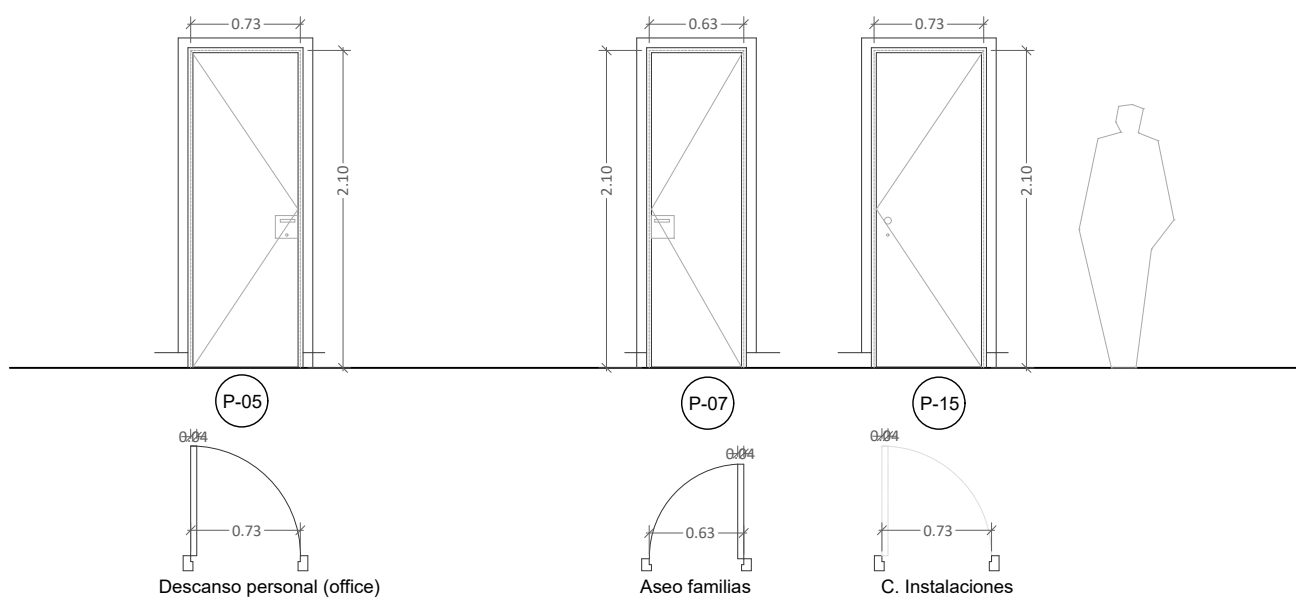

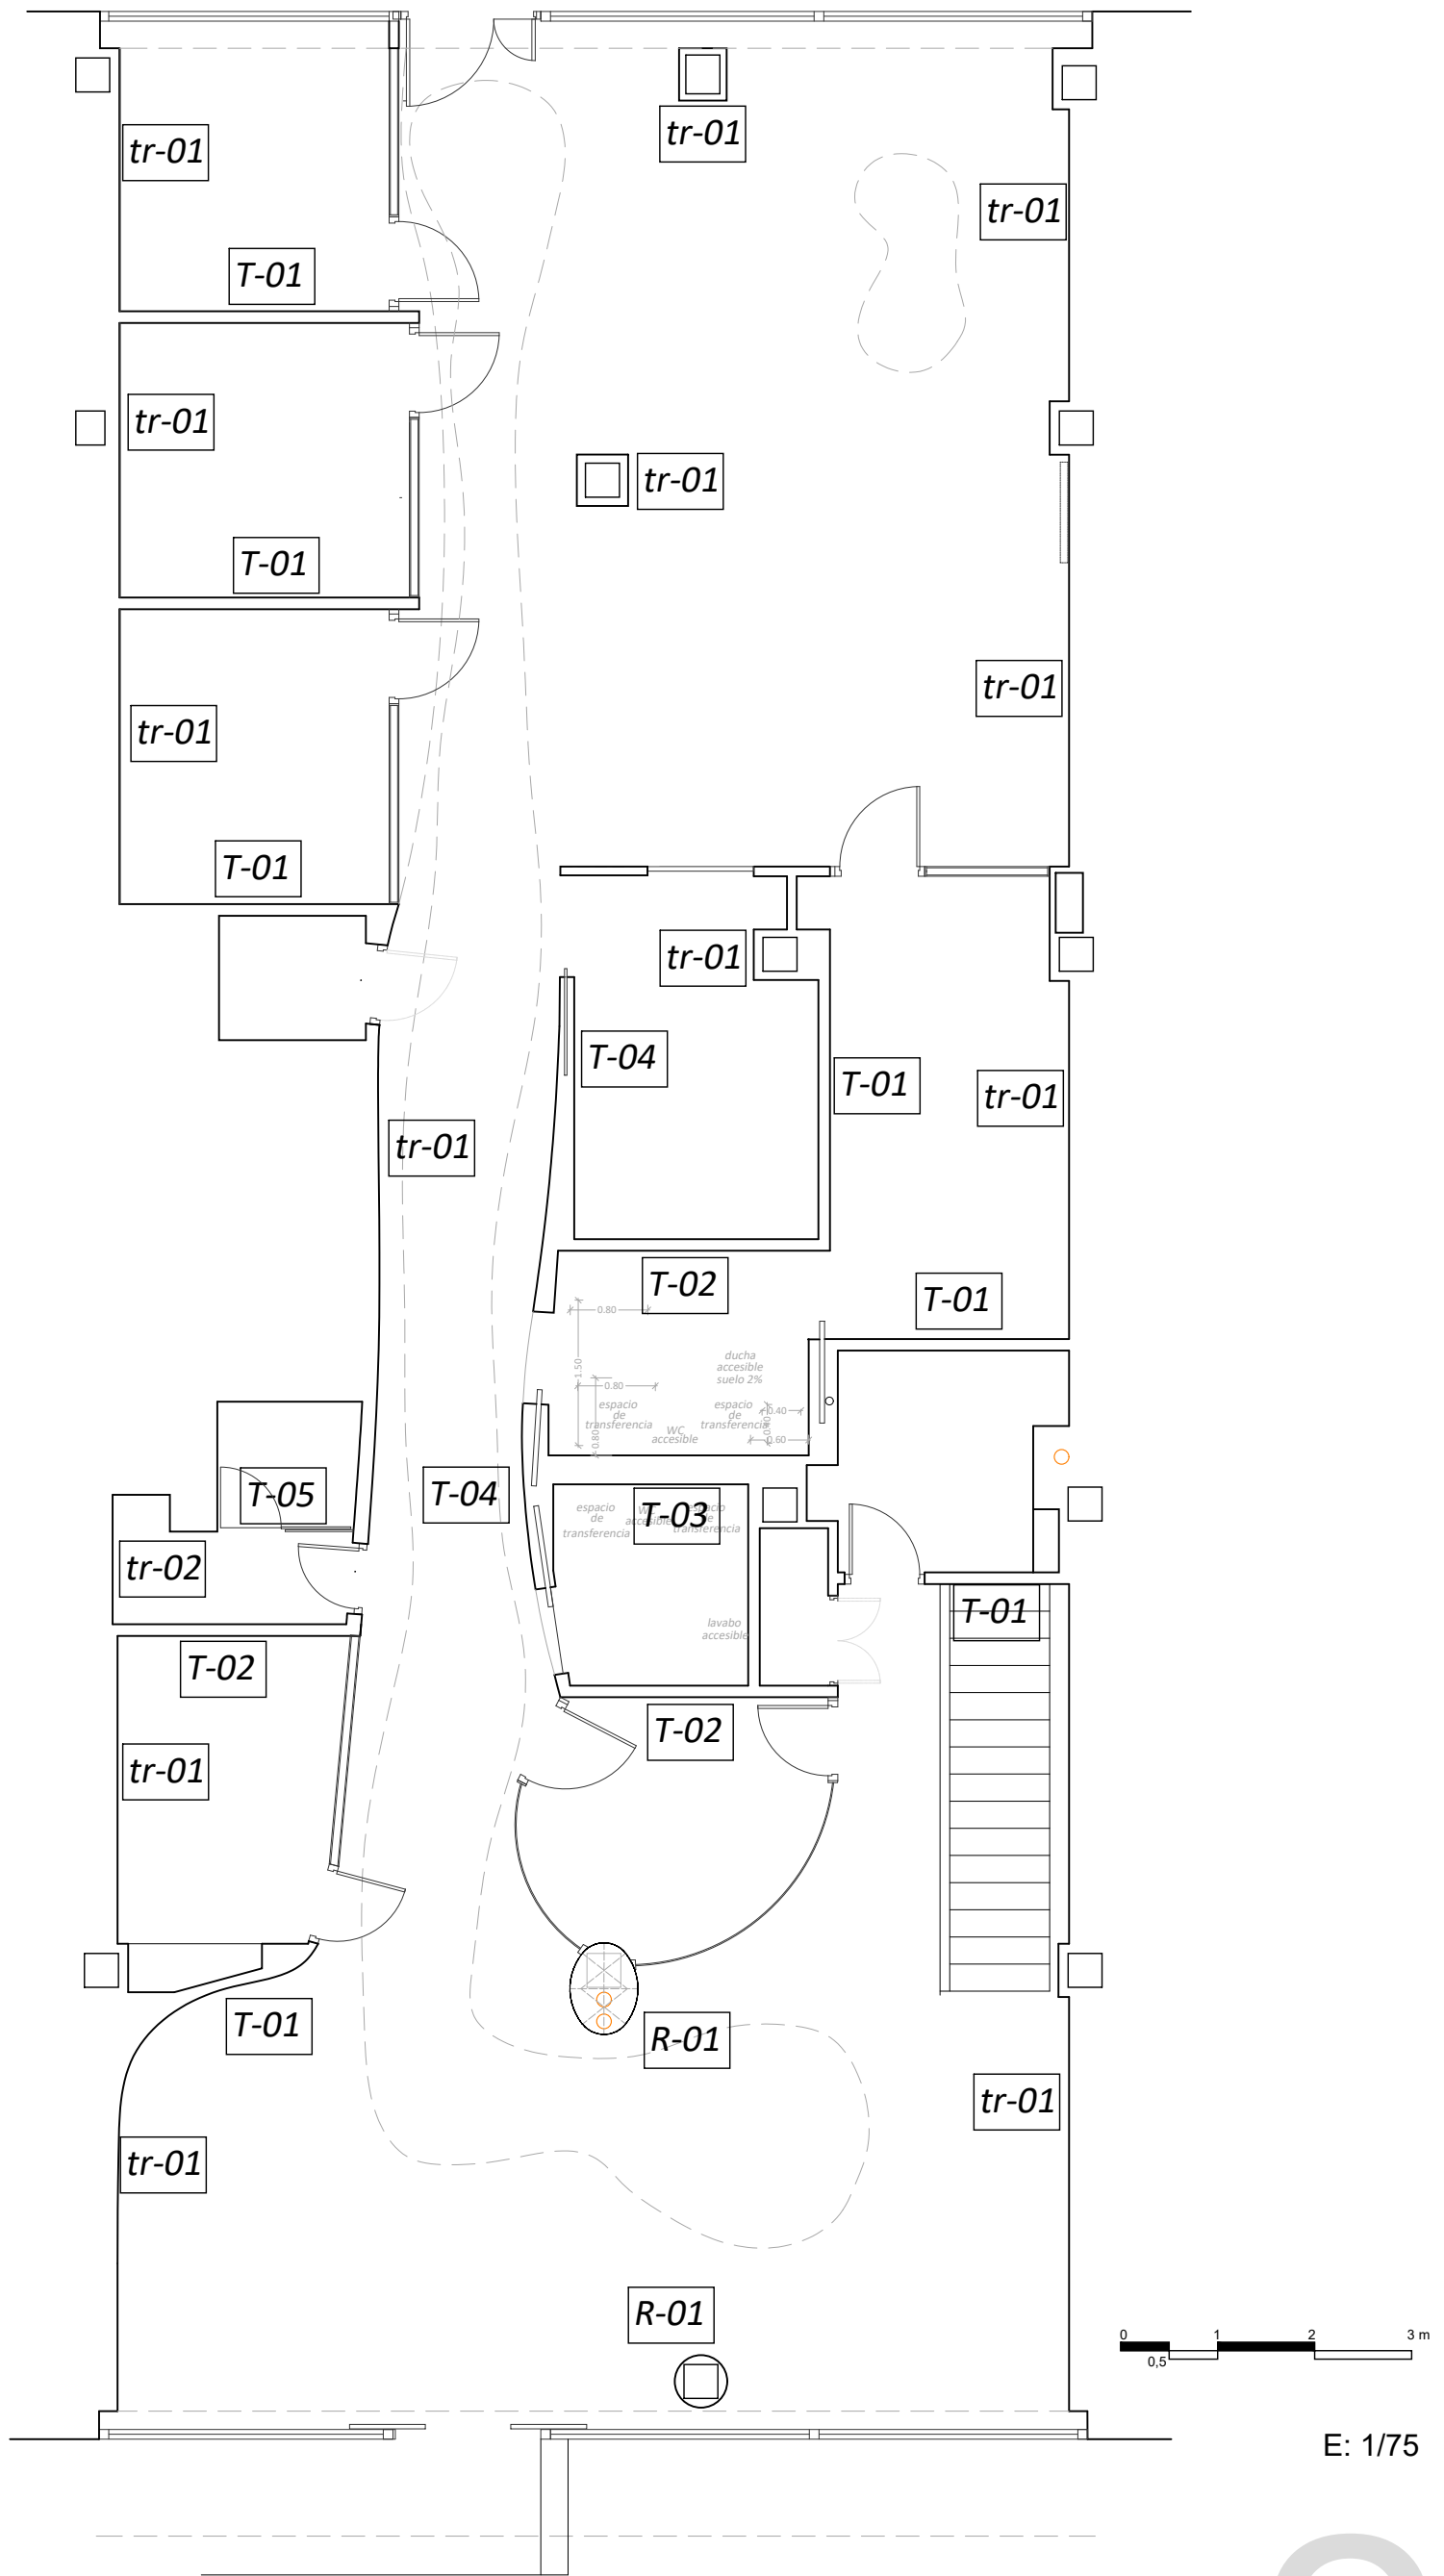

PEGASUS

REFORMA DE LOCAL PARA CENTRO DE REHABILITACIÓN EN AVDA. DE VALDEARGANDA, 2, ARGANDA DEL REY, MADRID (CP: 28500)

Arquitecto: Pablo Mosquera de Arancibia

Con el patrocinio de:


eduetrade

fecha: 27/11/2023

colegiado COAM, nº: 11.444

TABICUERÍA: PLANTA

23

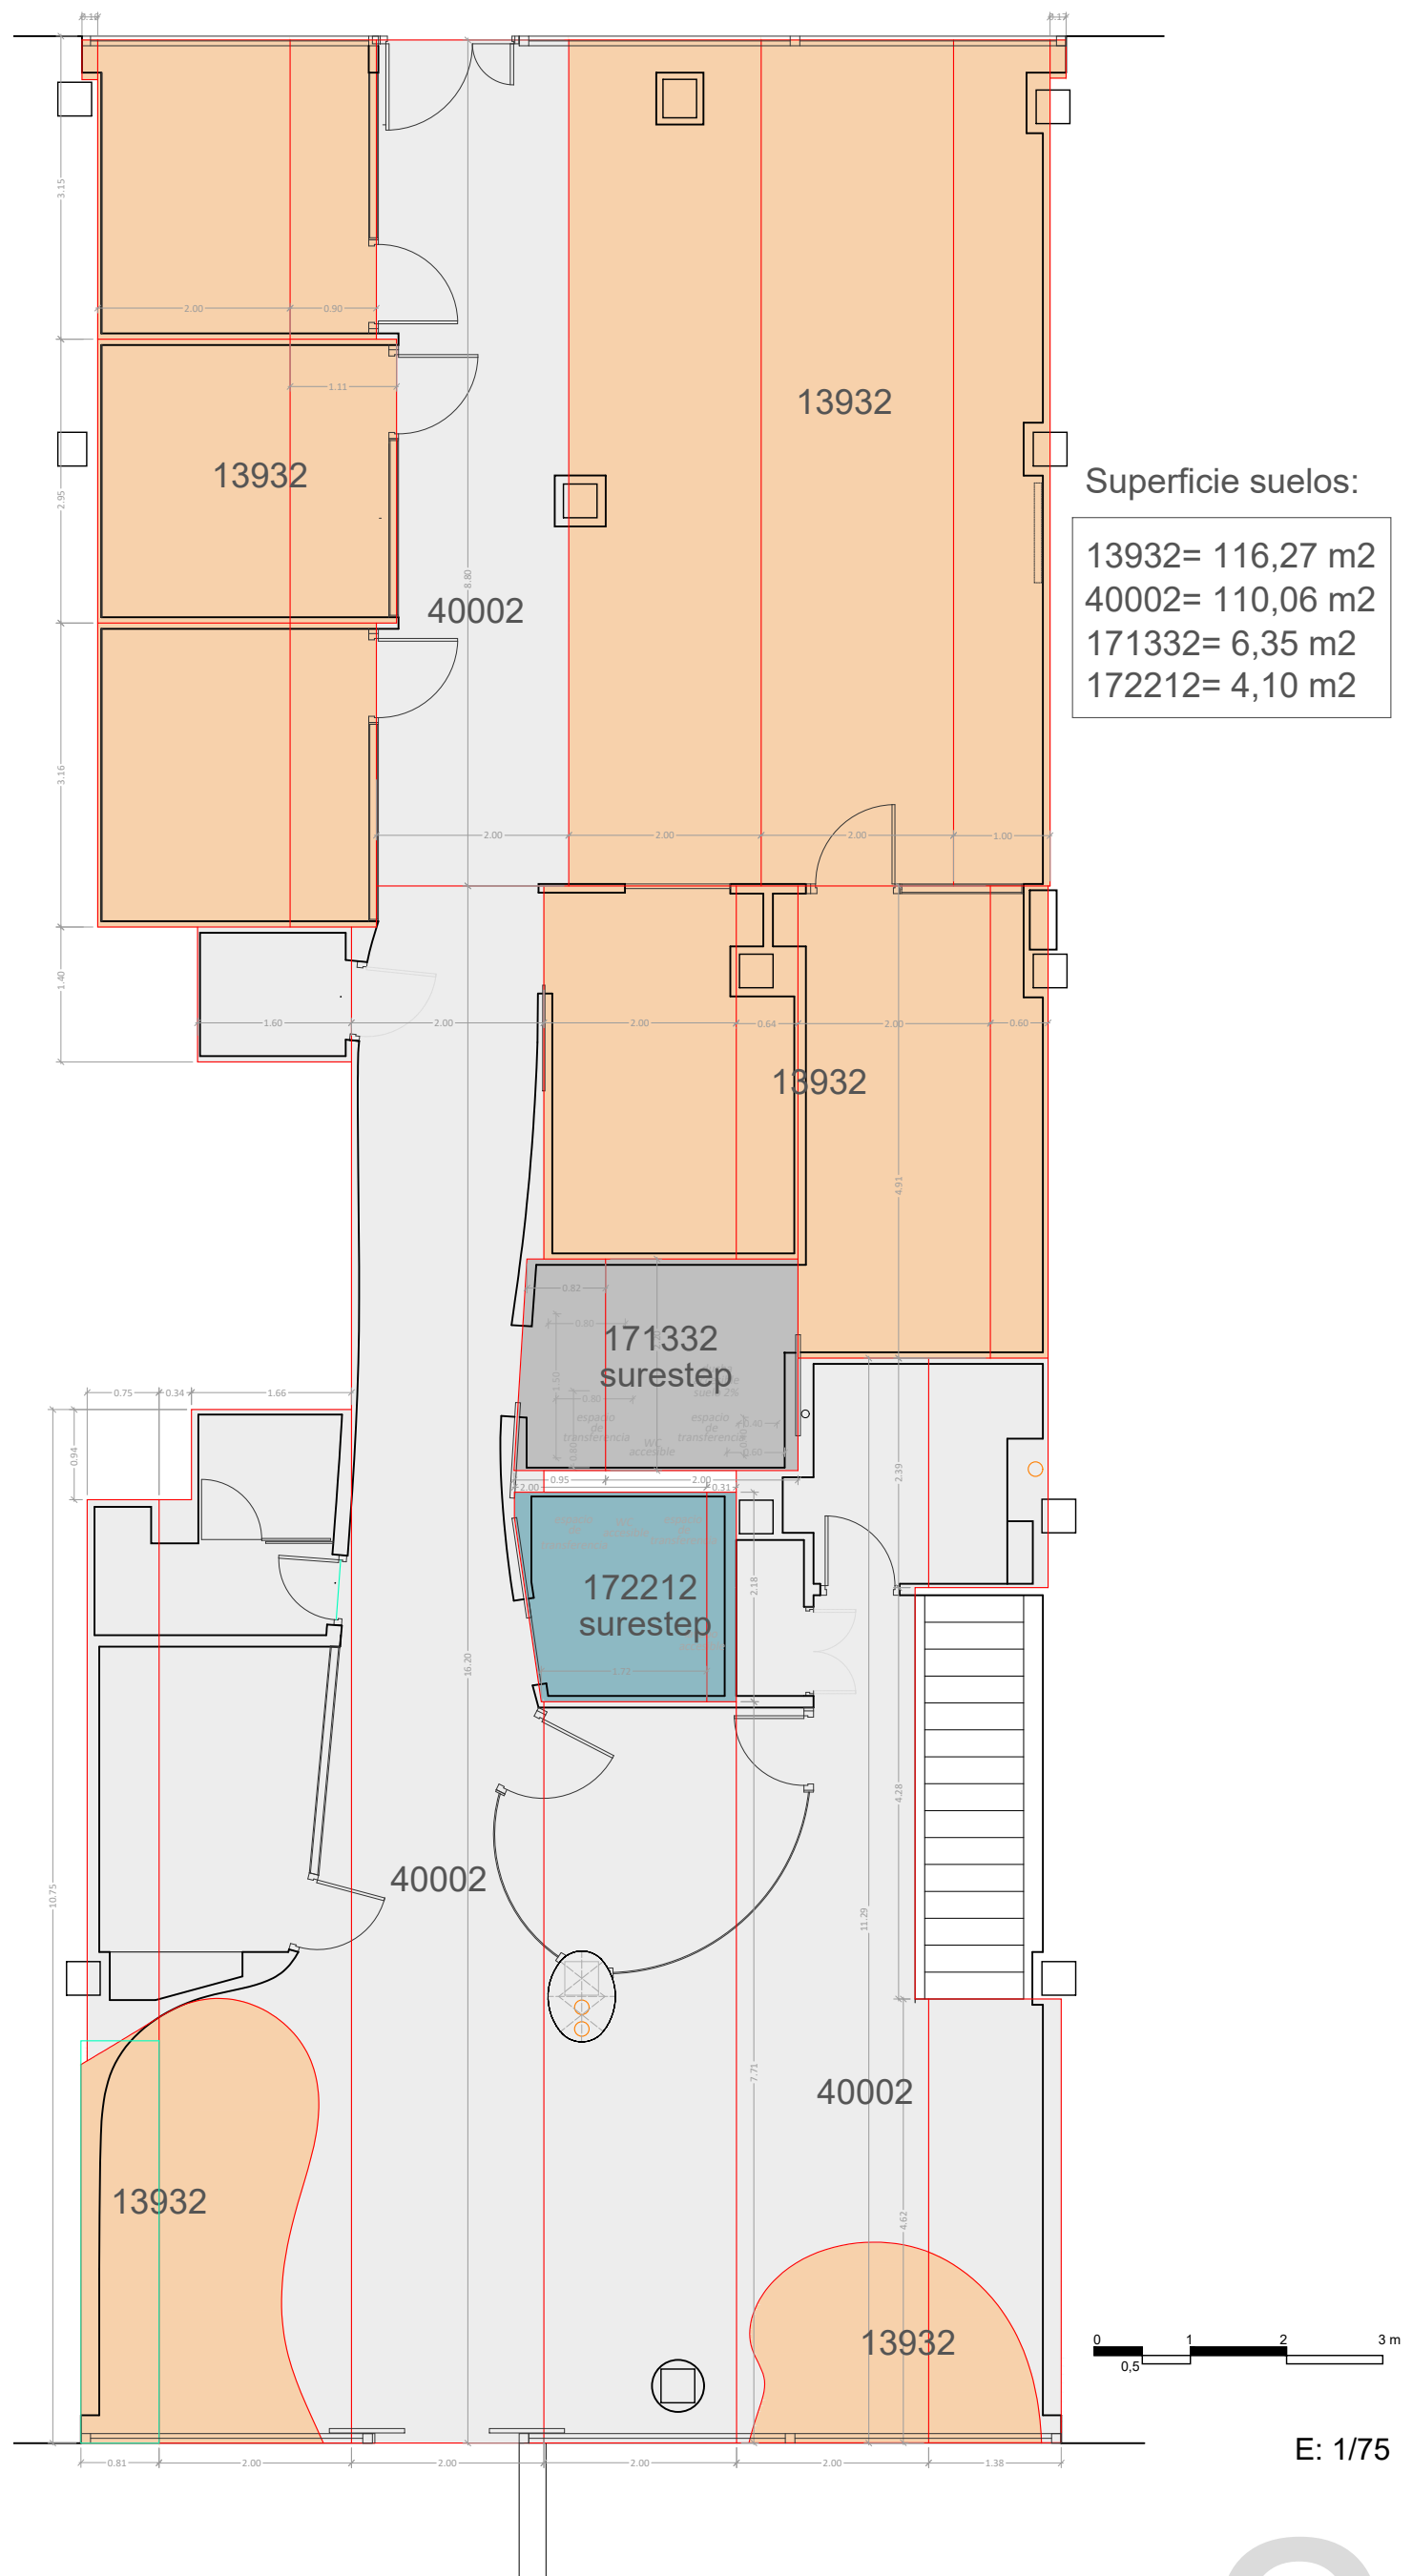

PEGASUS

REFORMA DE LOCAL PARA CENTRO DE REHABILITACIÓN EN AVDA. DE VALDEARGANDA, 2, ARGANDA DEL REY, MADRID (CP: 28500)

Arquitecto: Pablo Mosquera de Arancibia Con el patrocinio de:

edustrade

fecha: 27/11/2023


colegiado COAM, nº: 11.444

PLANTA BAJA: DESPIECE DE SUELOS VINÍLICOS

FASE: DIRECCIÓN DE OBRA-CERTIFICADO FINAL DE OBRA

E: 1/75

24

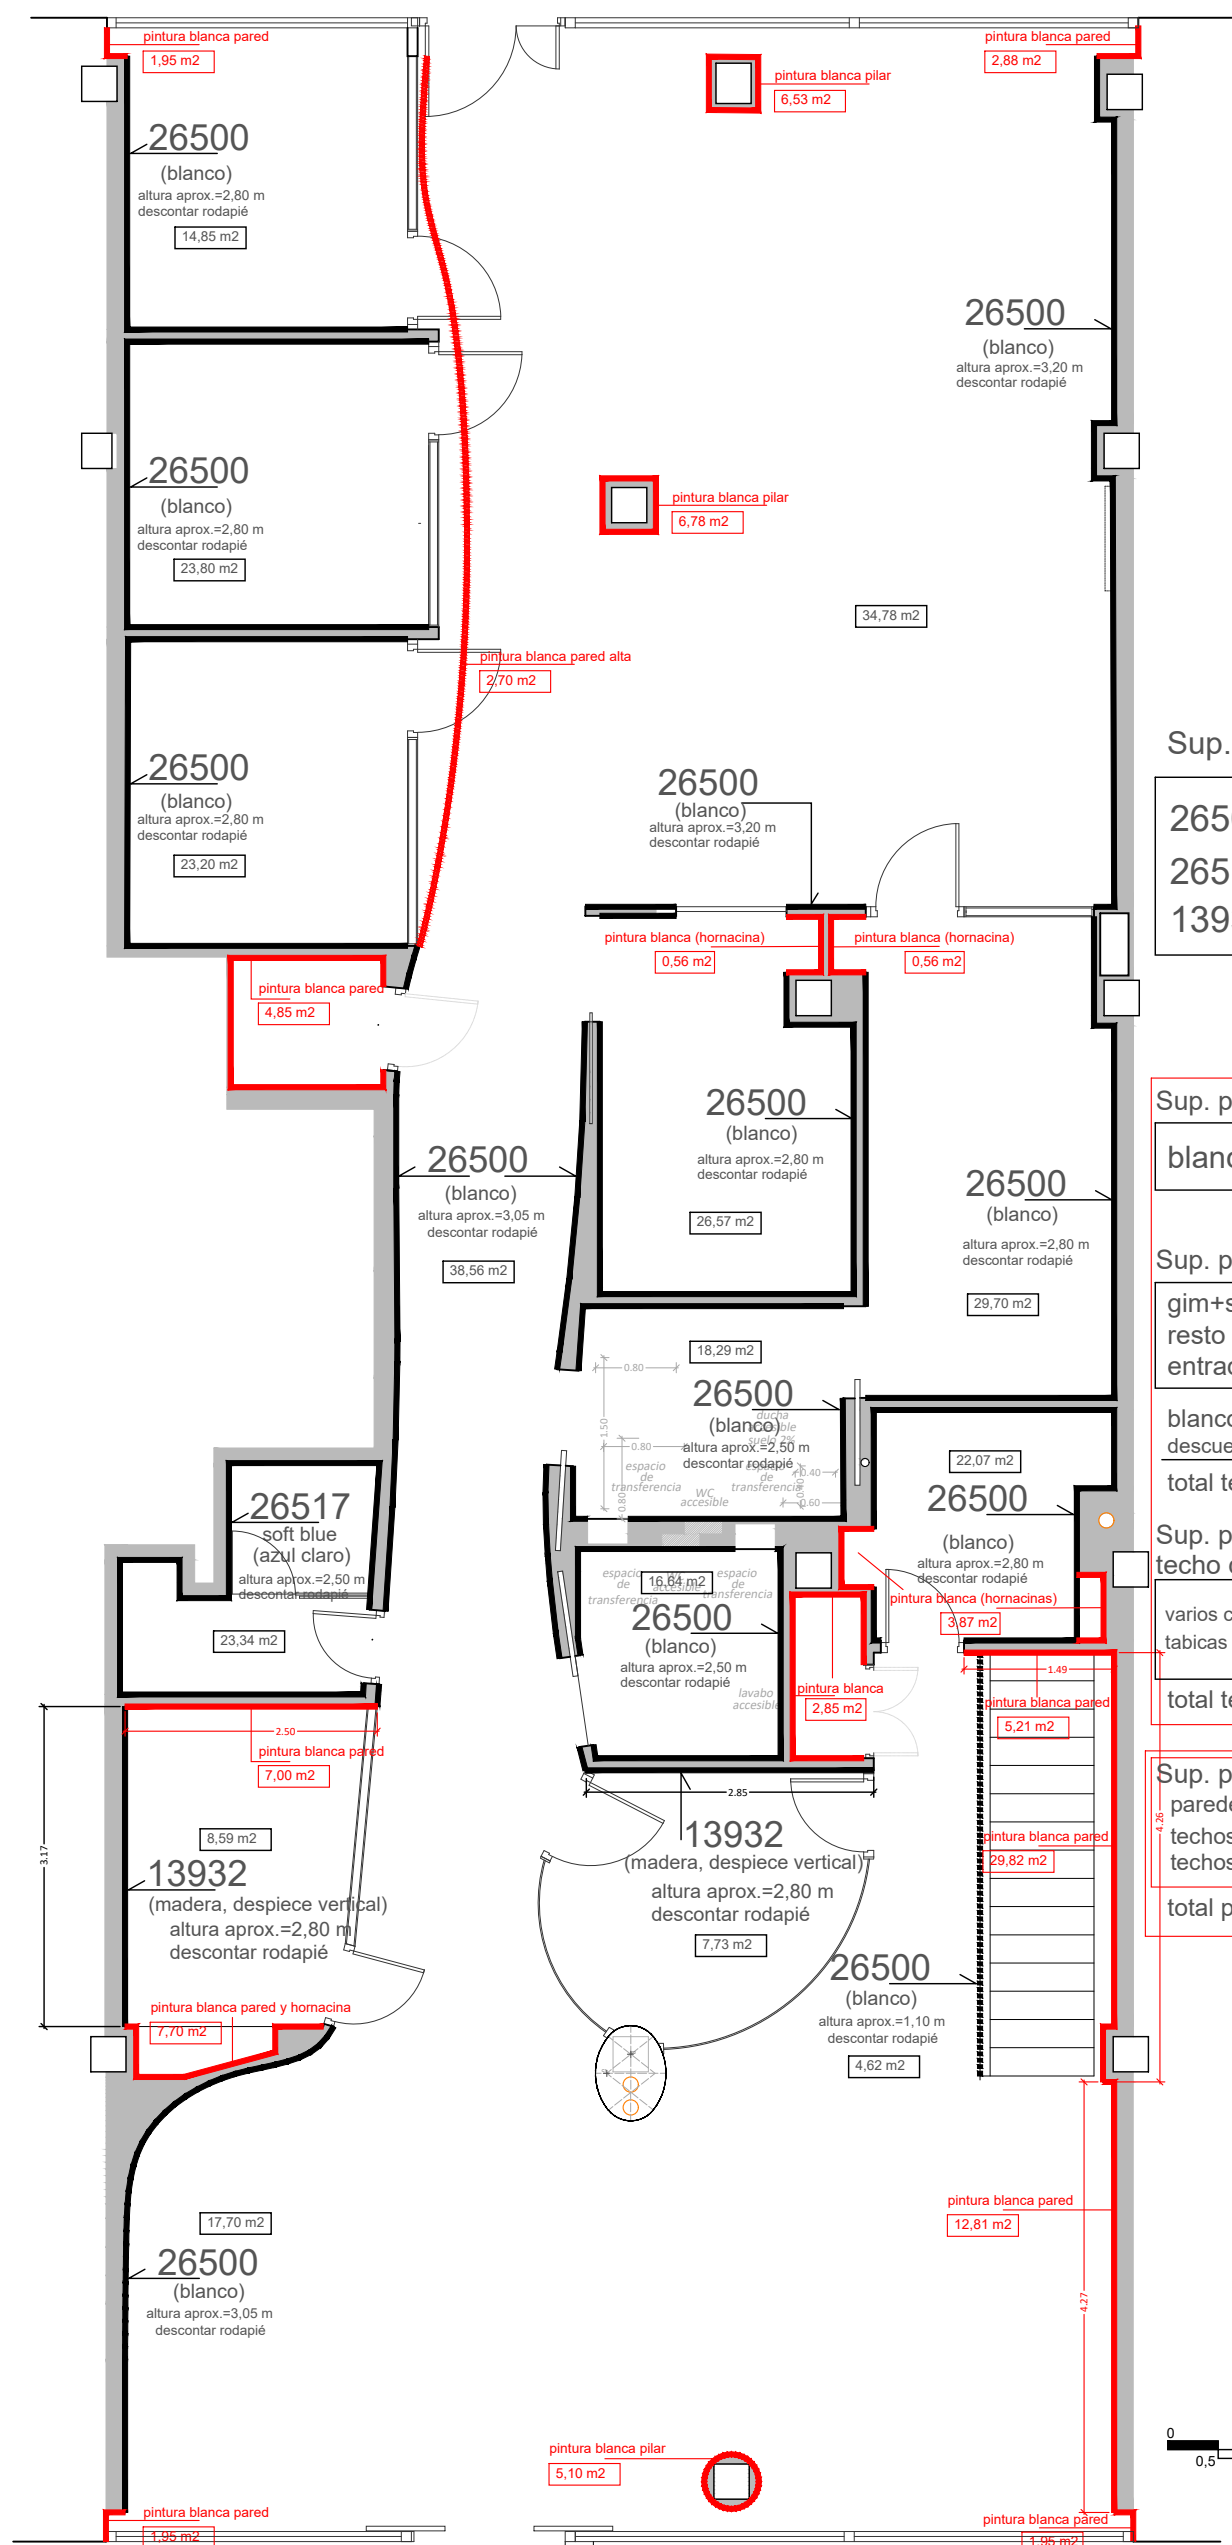

Sup. vinílicas paredes:

26500= 270,78 m2
26517= 23,34 m2
13932= 16,32 m2

310,44 m2

Sup. pintura paredes:

blanco= 105,07 m2

Sup. pintura techo plano:

gim+salas=85,00 m2
resto salas=50,57 m2
entrada+pasillo=84,2 m2

blanco= 219,77 m2
descuento techo curvo= -32,50 m2
total techo blanco= 187,27 m2

Sup. pintura
techo decorativo:

varios colores= 32,50 m2
tabicas color o blancas= 20,00 m2
total techo colores= 52,50 m2

Sup. pintura:

paredes blancas= 105,07 m2
techos blancos= 187,27 m2
techos colores= 52,50 m2
total pintura= 344,84 m2



PEGASUS

REFORMA DE LOCAL PARA CENTRO DE REHABILITACIÓN EN AVDA. DE VALDEARGANDA, 2, ARGANDA DEL REY, MADRID (CP: 28500)

Arquitecto: Pablo Mosquera de Arancibia Con el patrocinio de:

eduetrade


fecha: 27/11/2023

colegiado COAM, nº: 11.444

ACABADOS DE PAREDES (VINÍLICOS Y PINTURA) Y TECHOS (PINTURA)

FASE: DIRECCIÓN DE OBRA-CERTIFICADO FINAL DE OBRA

25

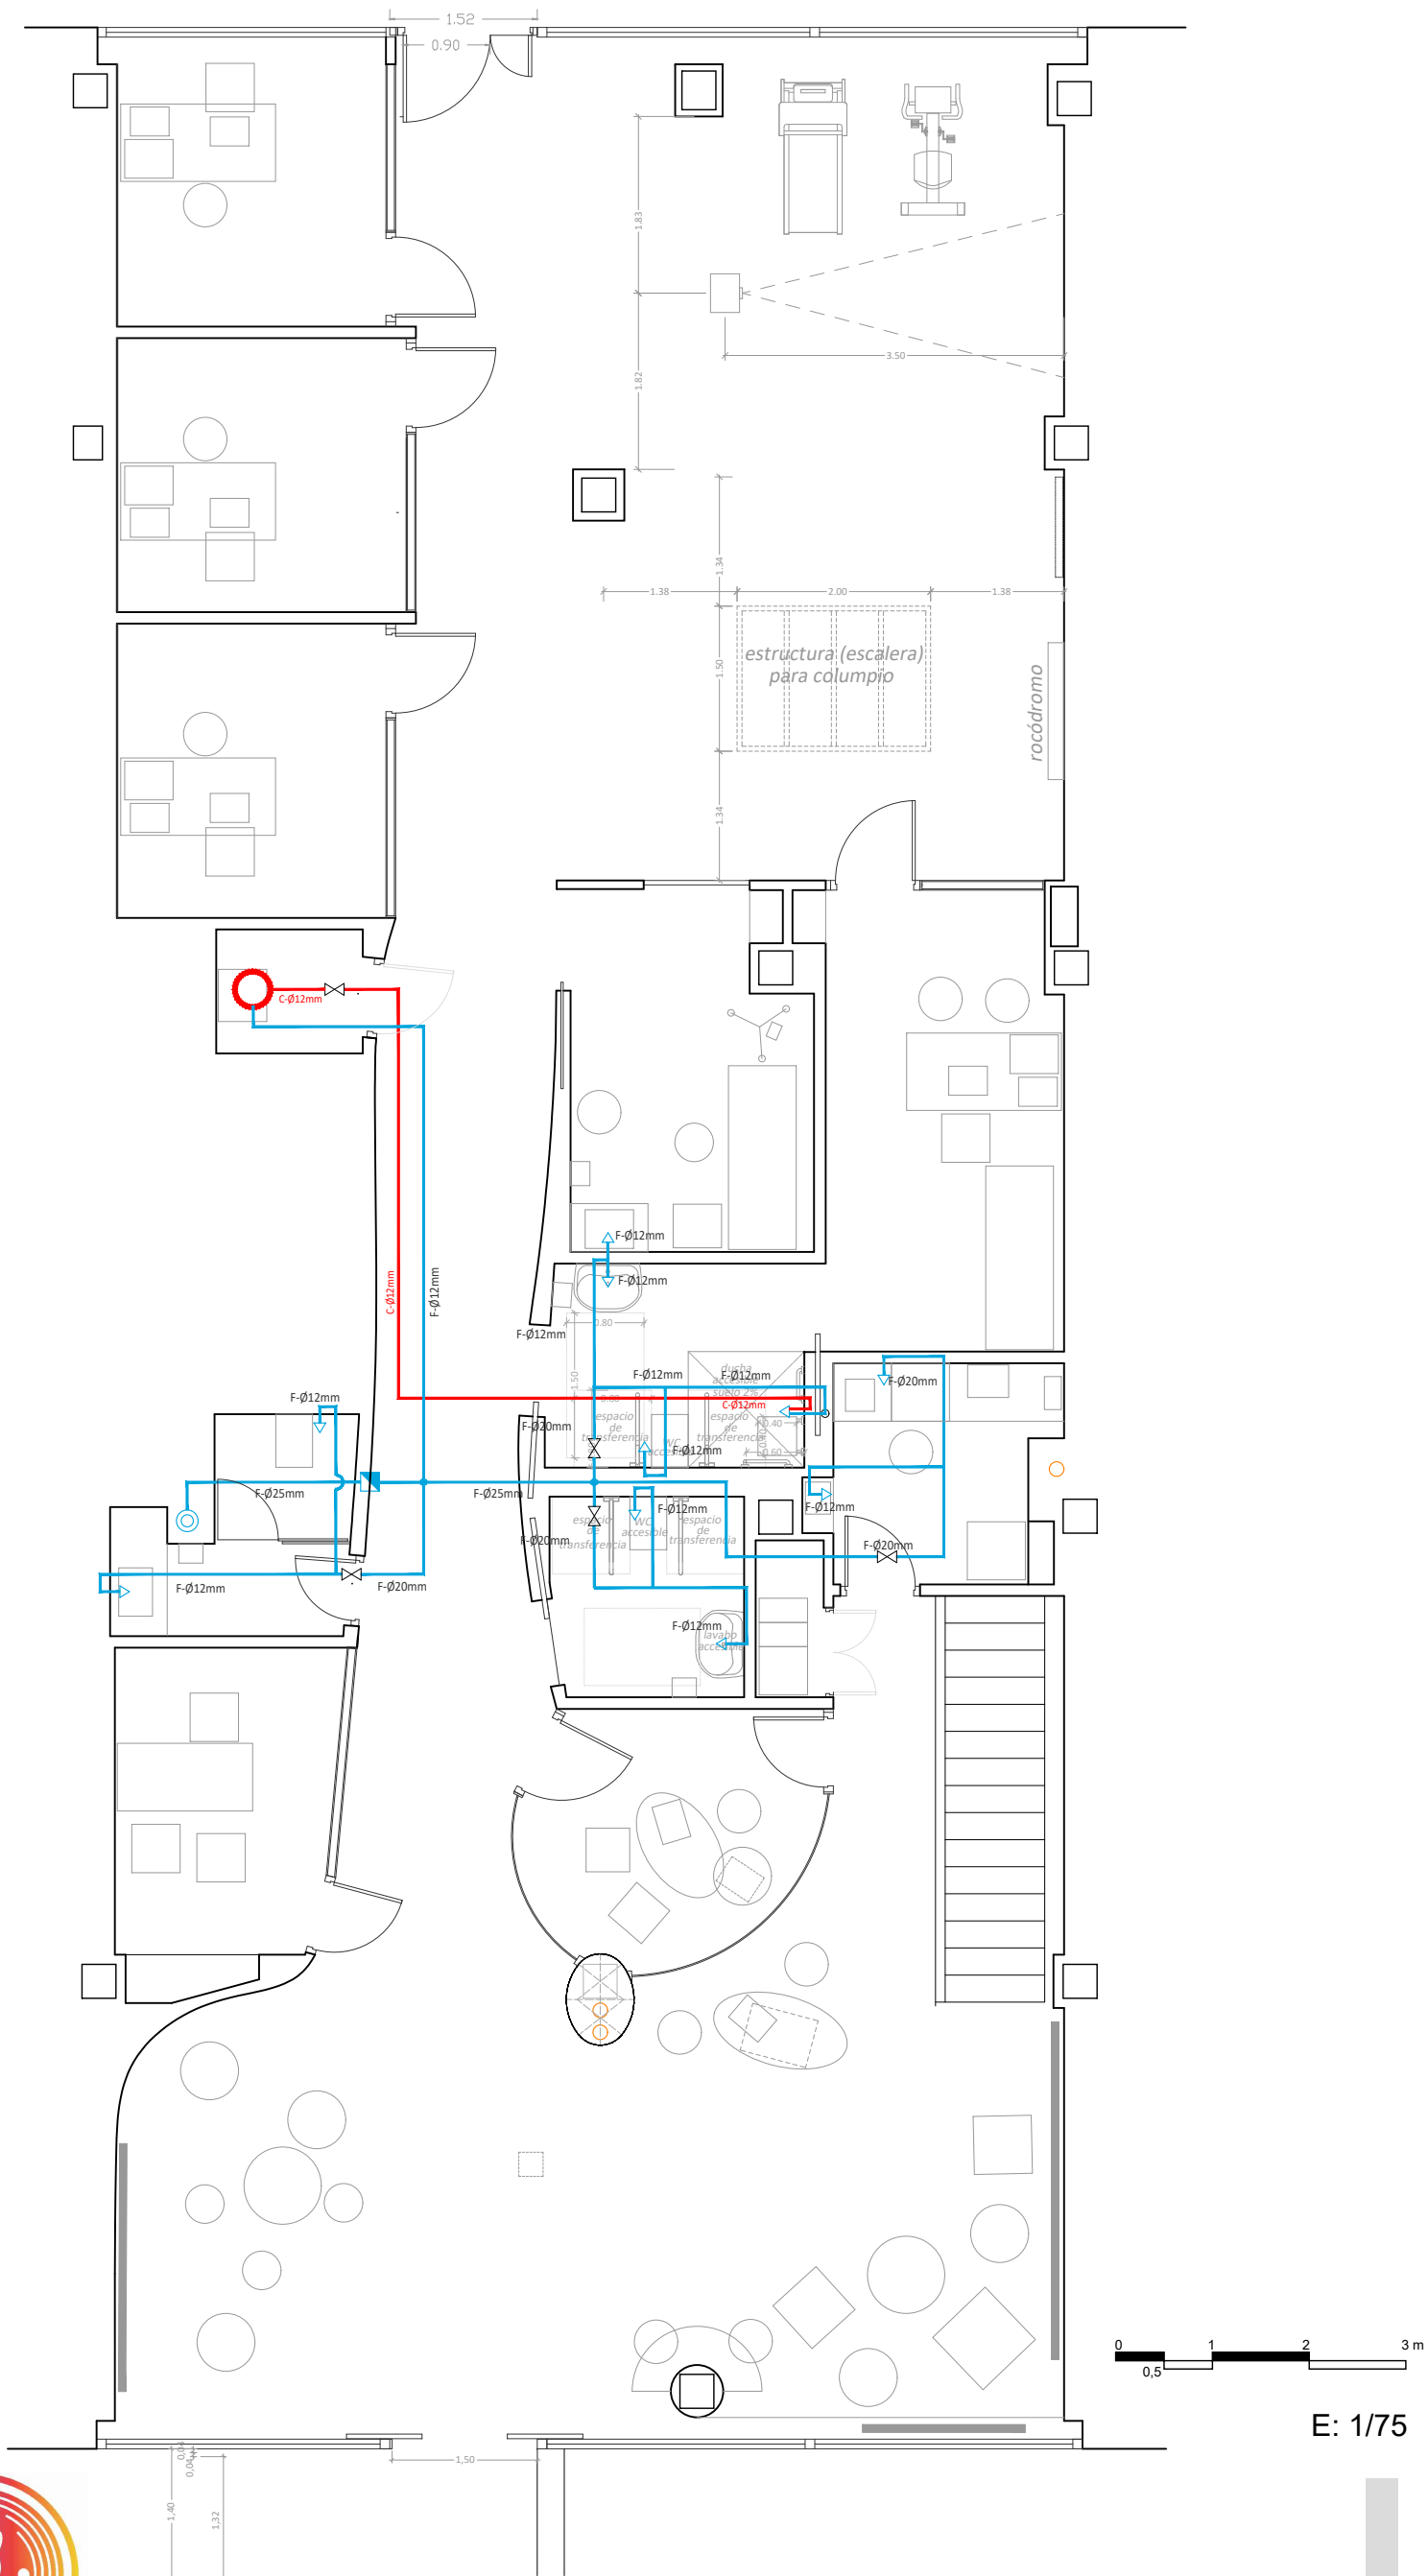

PEGASUS

REFORMA DE LOCAL PARA CENTRO DE REHABILITACIÓN EN AVDA. DE VALDEARGANDA, 2, ARGANDA DEL REY, MADRID (CP: 28500)


Arquitecto: Pablo Mosquera de Arancibia Con el patrocinio de:

edustrade

fecha: 27/11/2023

FONTANERÍA

1.01

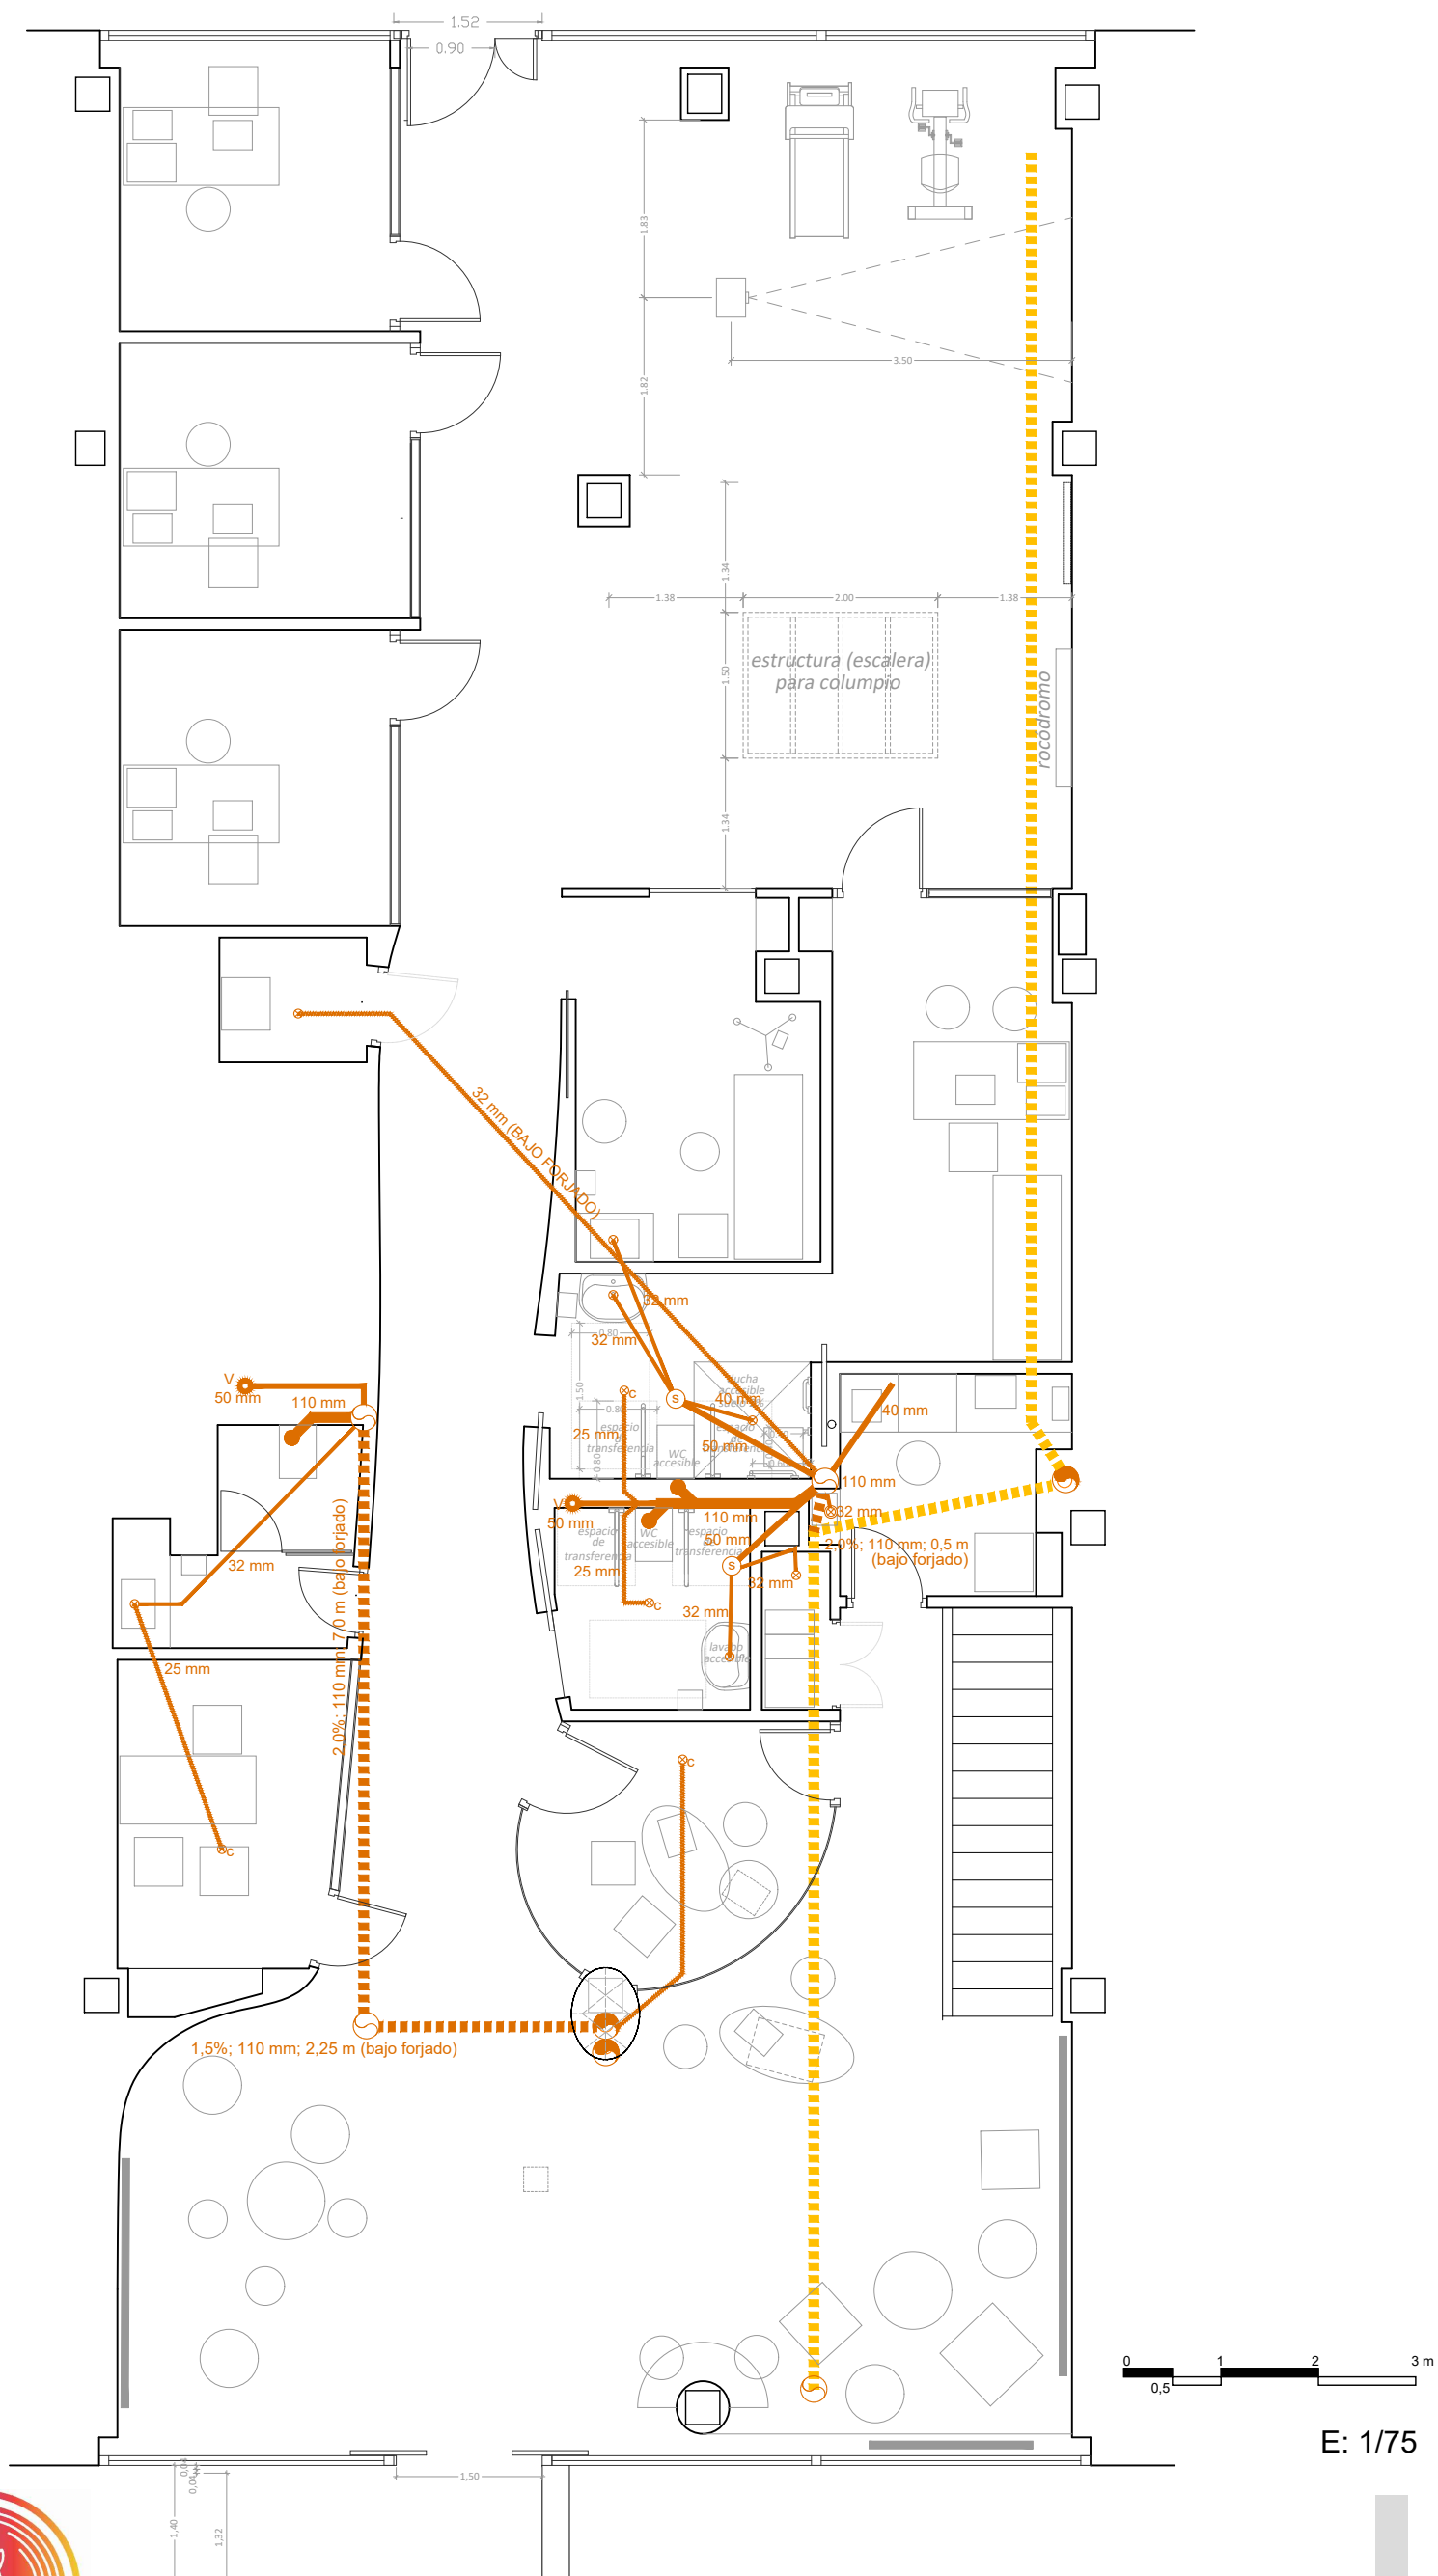

PEGASUS

REFORMA DE LOCAL PARA CENTRO DE REHABILITACIÓN EN AVDA. DE VALDEARGANDA, 2, ARGANDA DEL REY, MADRID (CP: 28500)



Arquitecto: Pablo Mosquera de Arancibia Con el patrocinio de:

edustrade

fecha: 27/11/2023

SANEAMIENTO

1.02

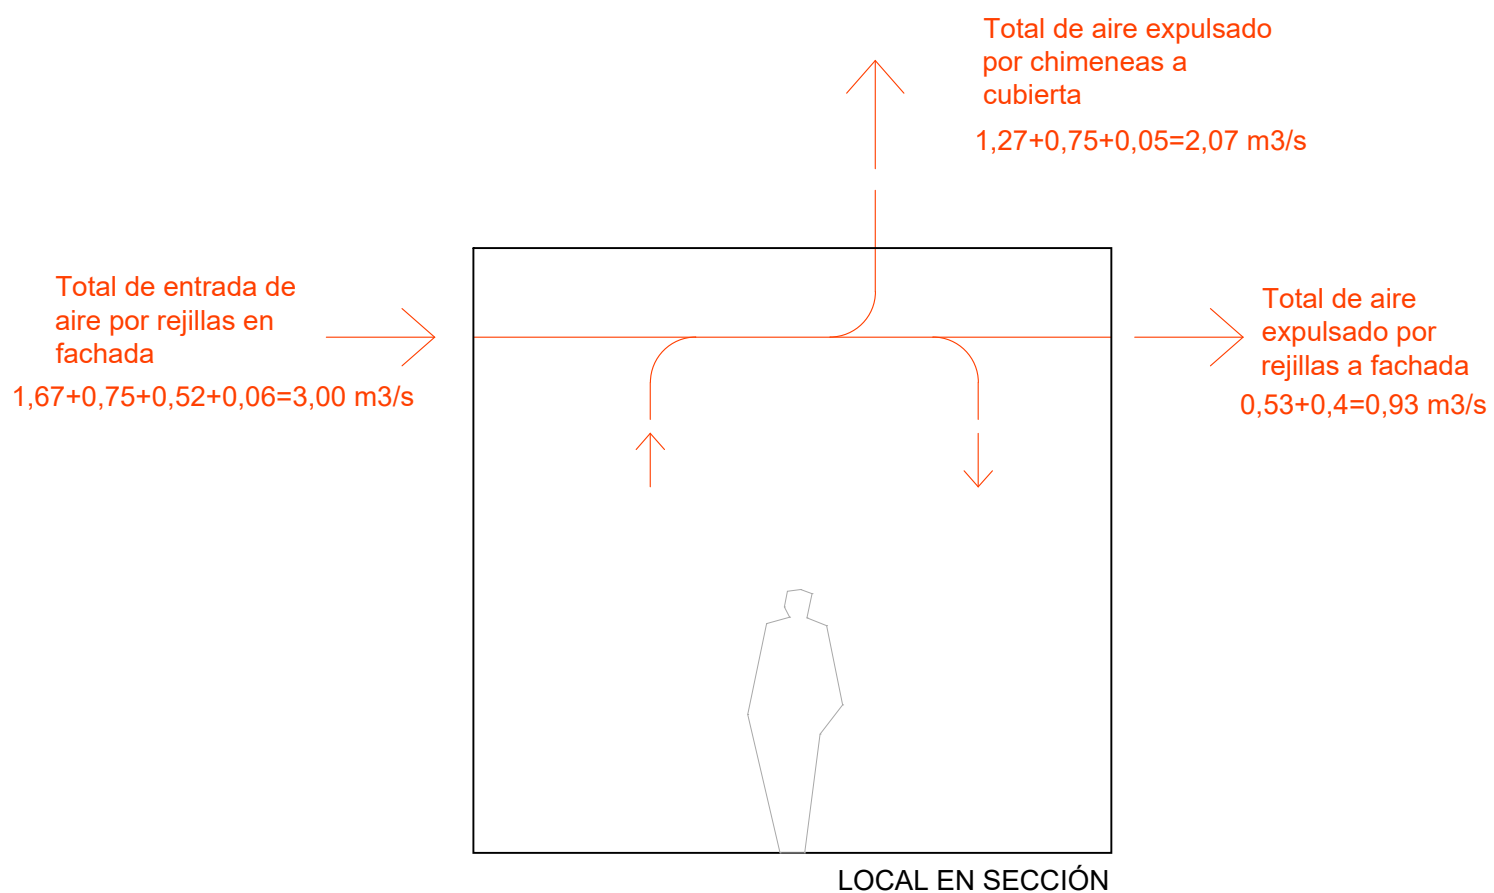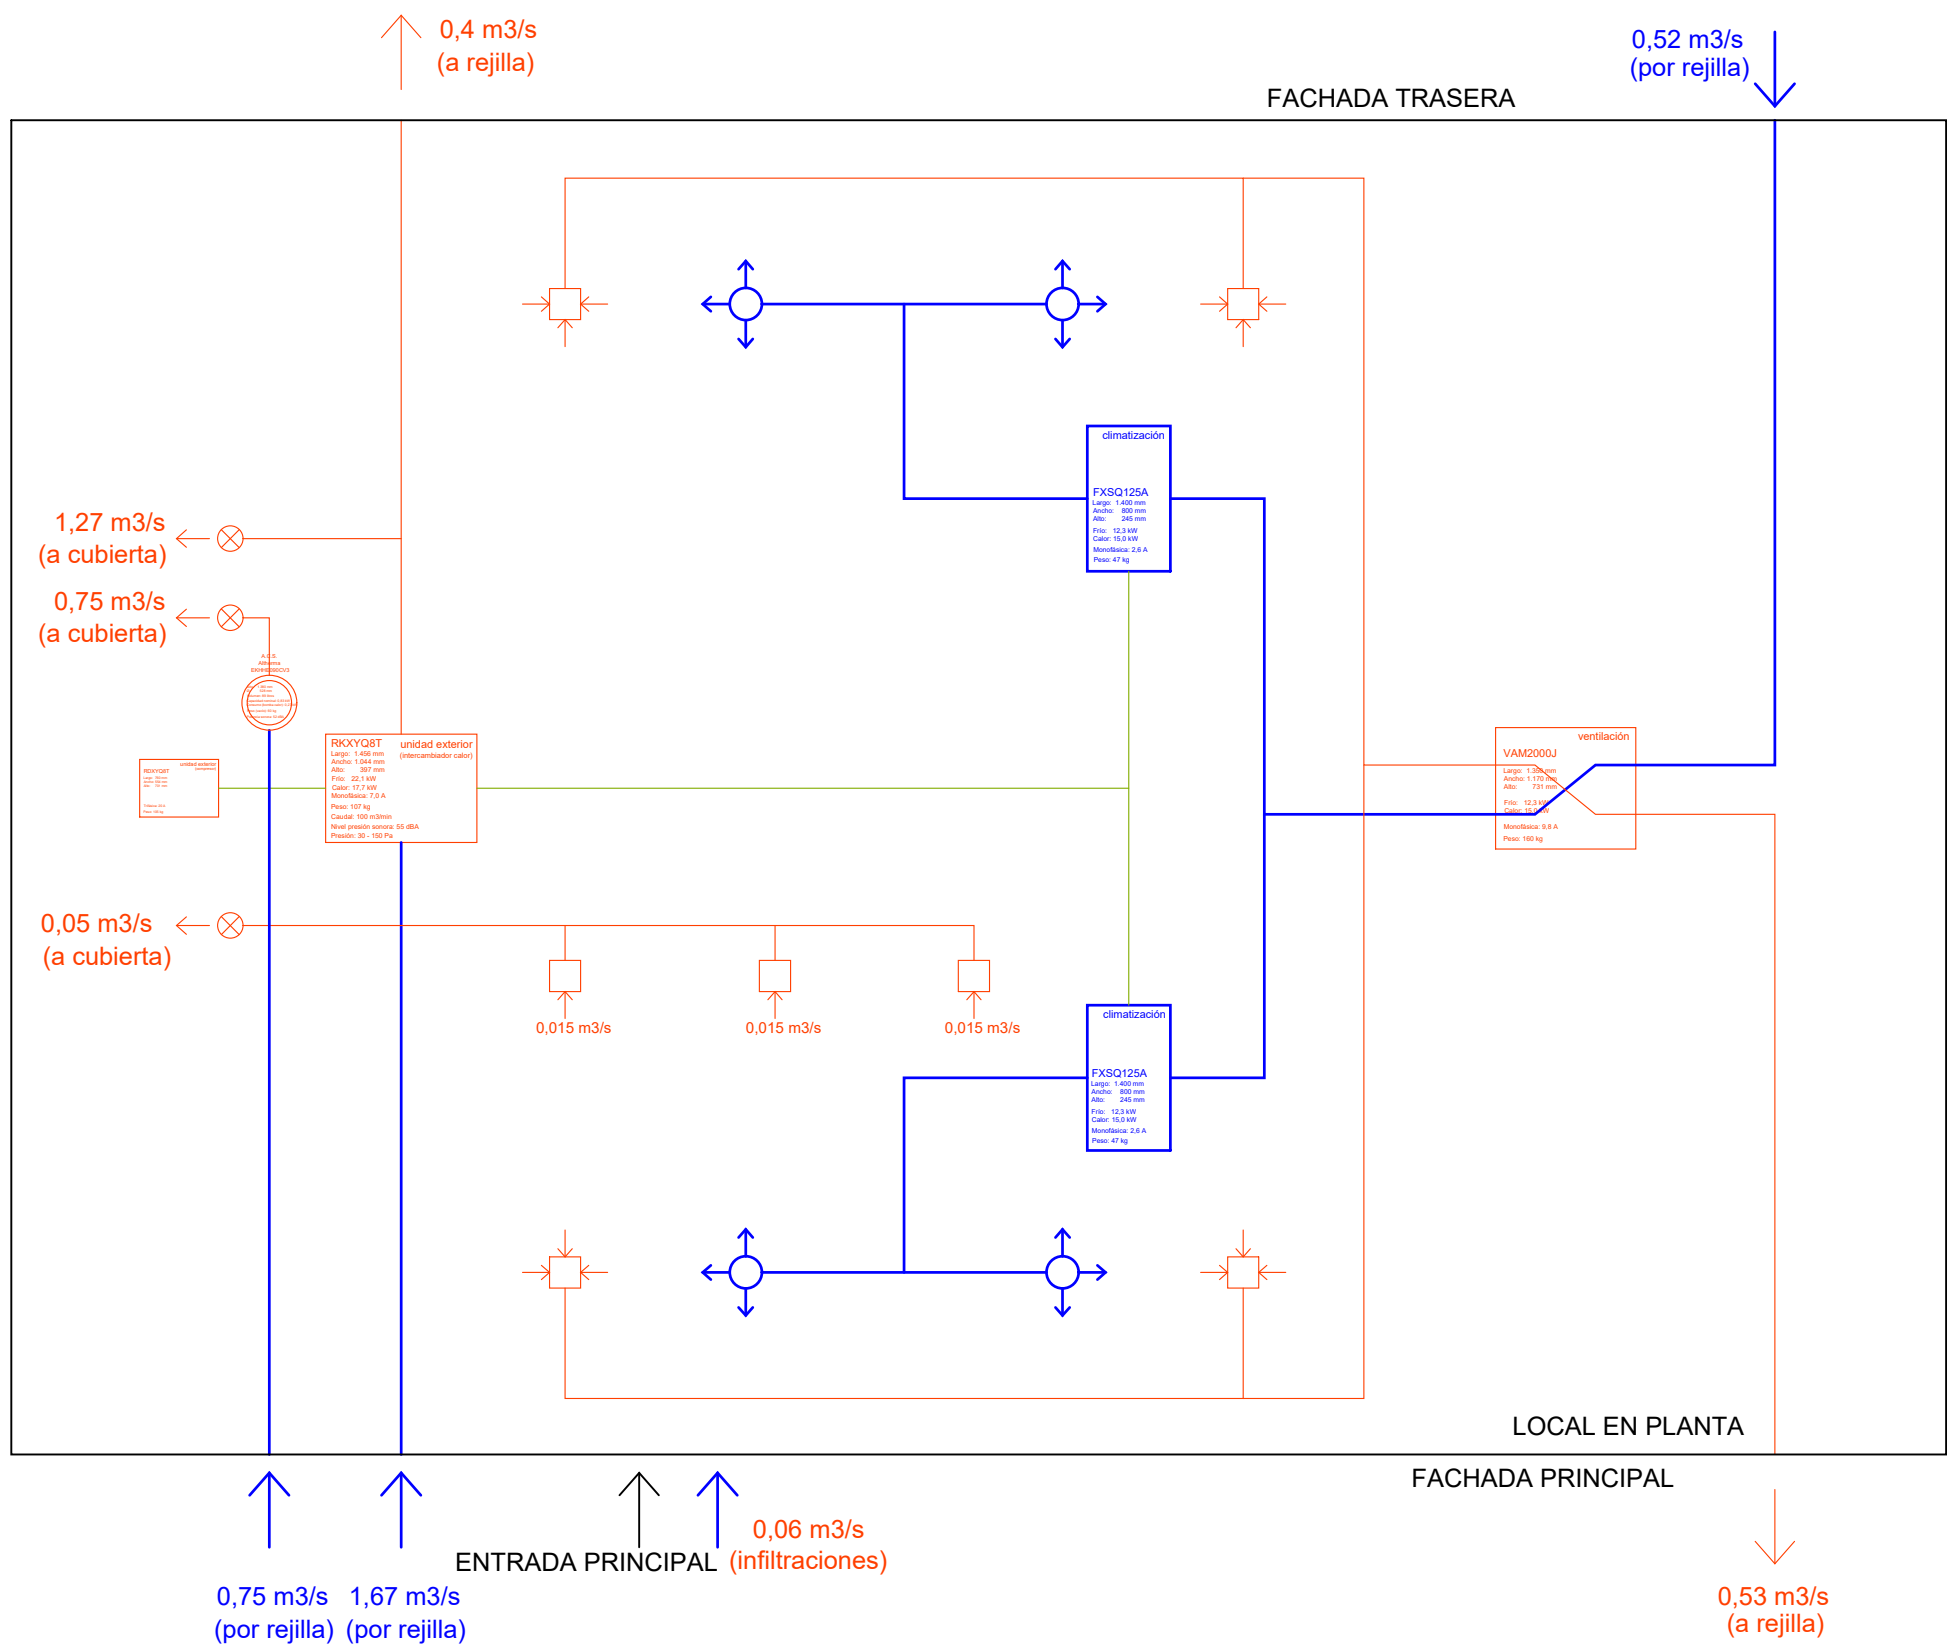

PEGASUS

REFORMA DE LOCAL PARA CENTRO DE REHABILITACIÓN EN AVDA. DE VALDEARGANDA, 2, ARGANDA DEL REY, MADRID (CP: 28500)

Arquitecto: Pablo Mosquera de Arancibia Con el patrocinio de:


eduetrade

fecha: 27/11/2023

colegiado COAM, nº: 11.444

ESQUEMA DE PRINCIPIO 1: CLIMATIZACIÓN Y VENTILACIÓN

FASE: DIRECCIÓN DE OBRA-CERTIFICADO FINAL DE OBRA

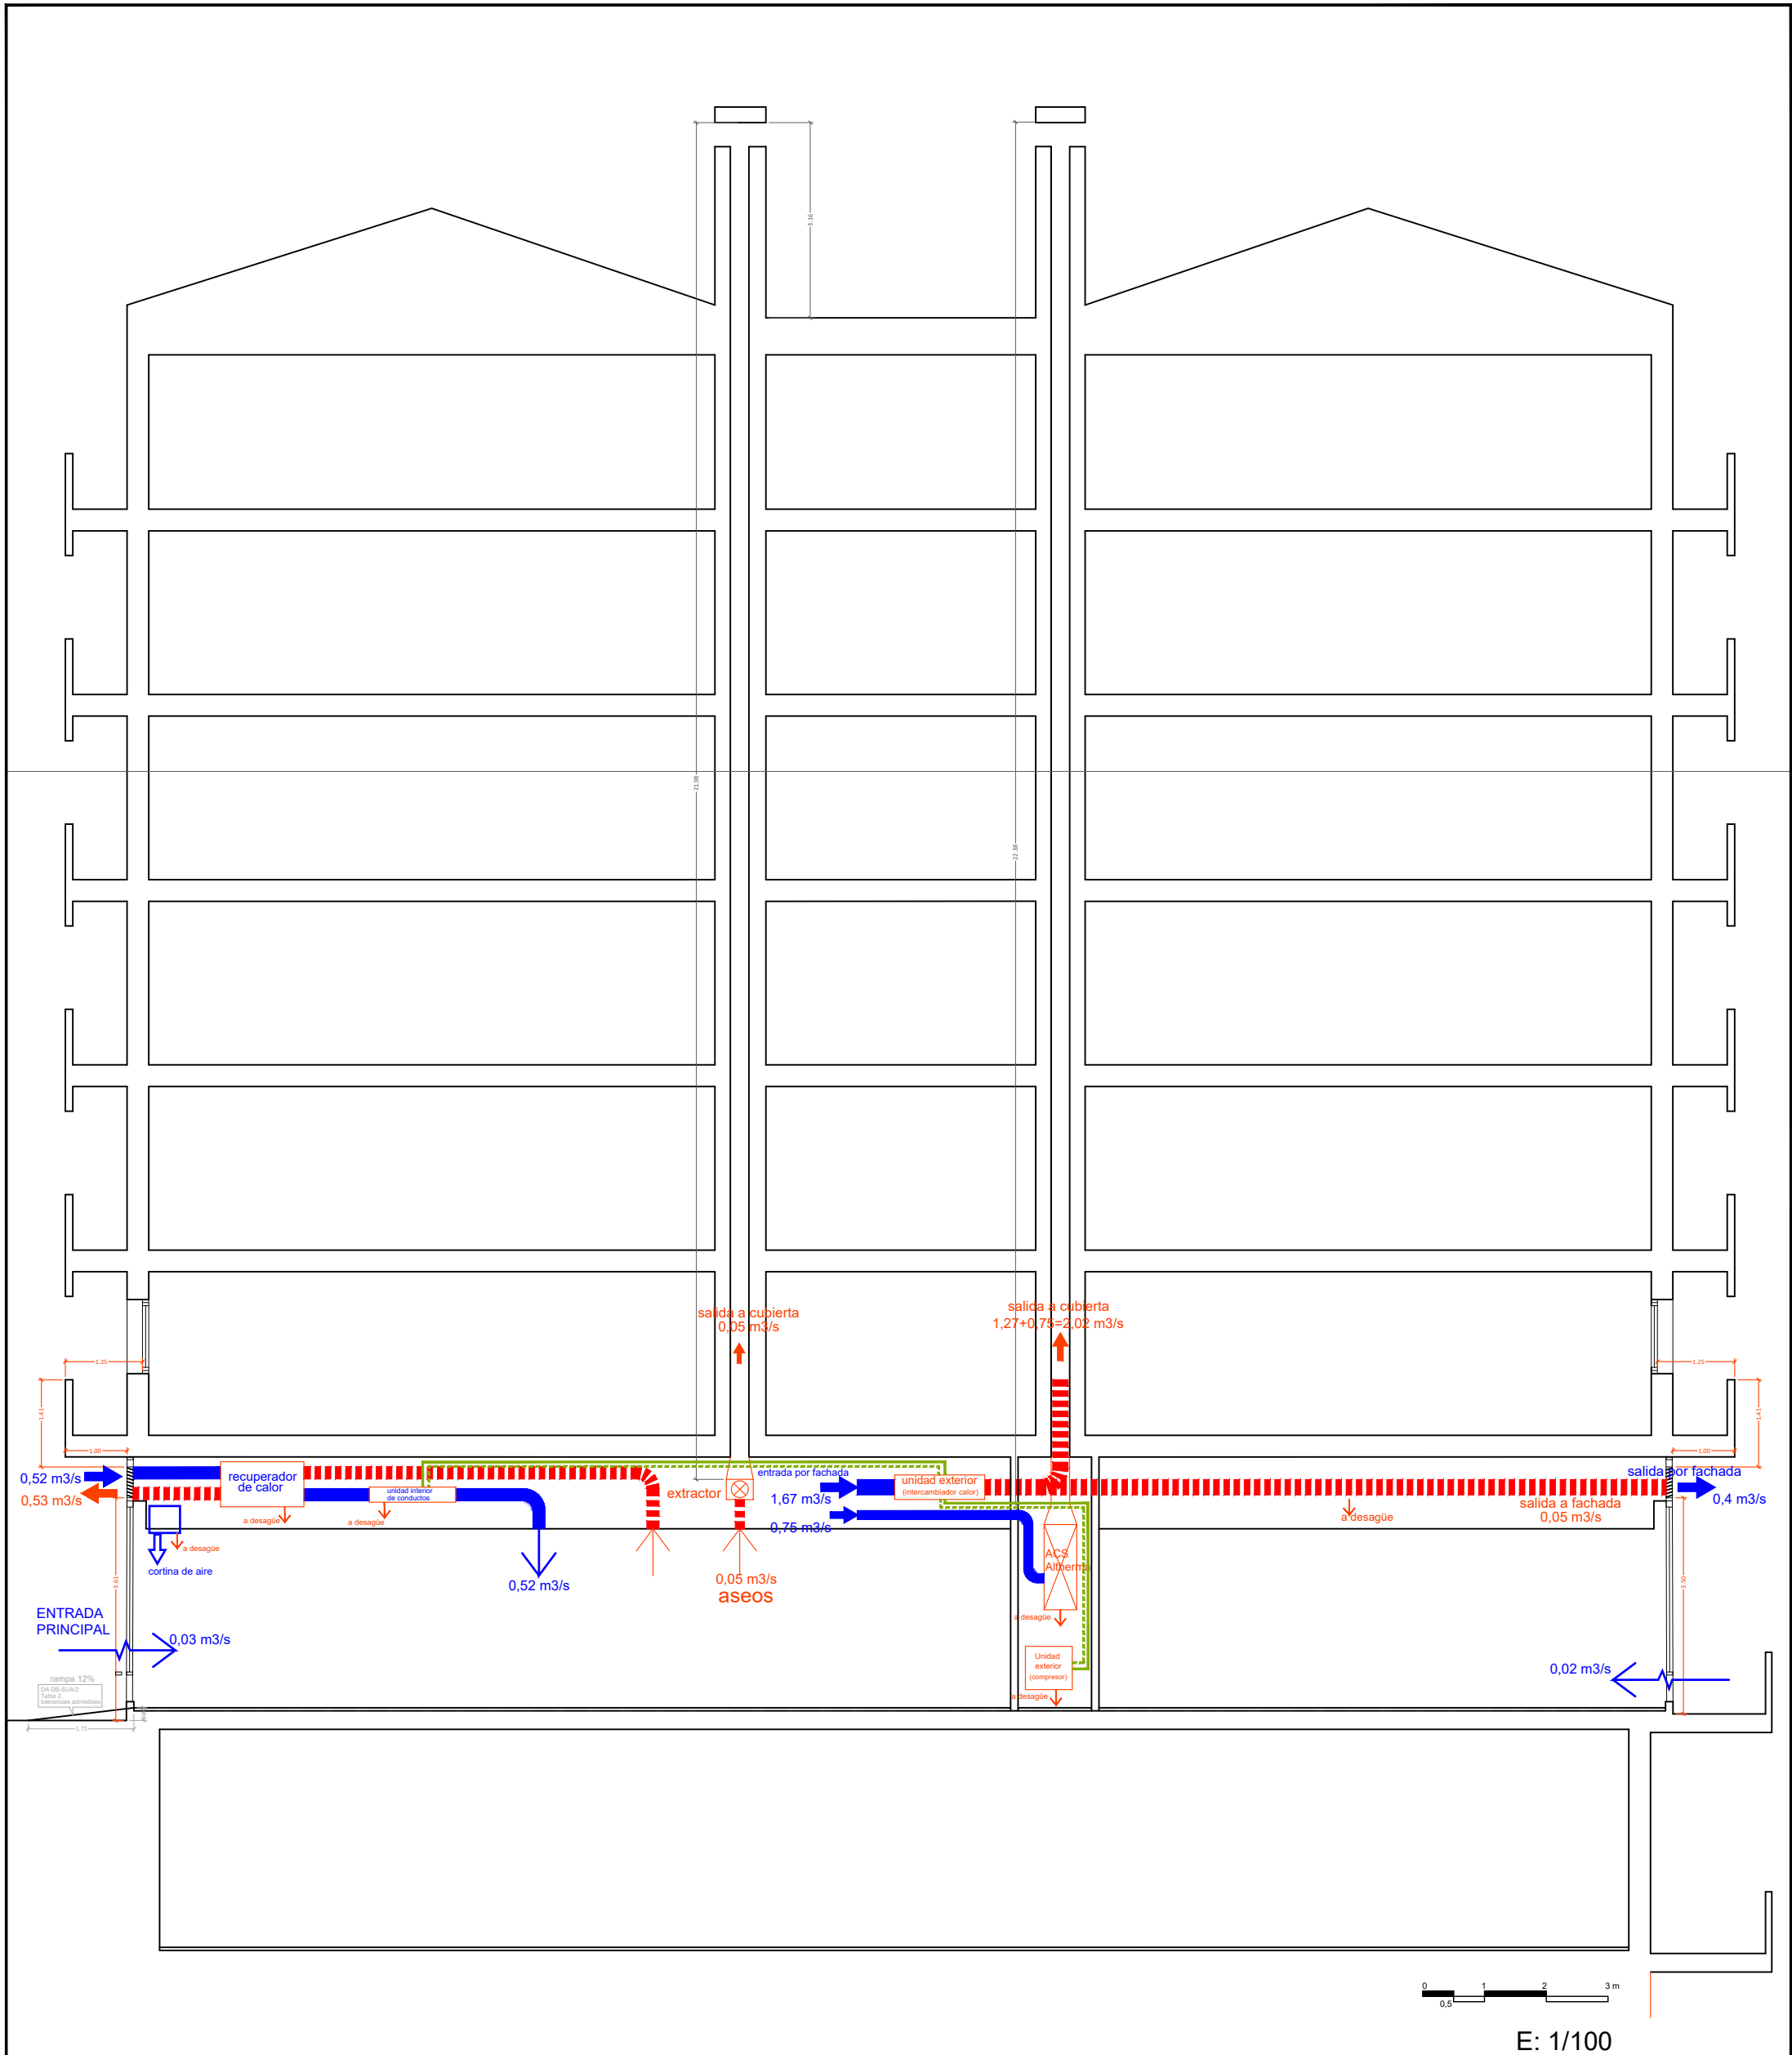

PEGASUS

REFORMA DE LOCAL PARA CENTRO DE REHABILITACIÓN EN AVDA. DE VALDEARGANDA, 2, ARGANDA DEL REY, MADRID (CP: 28500)

Arquitecto: Pablo Mosquera de Arancibia Con el patrocinio de:


eduetrade

fecha: 27/11/2023

colegiado COAM, nº: 11.444

ESQUEMA DE PRINCIPIO 2: SECCIÓN CLIMATIZACIÓN Y VENTILACIÓN

FASE: DIRECCIÓN DE OBRA-CERTIFICADO FINAL DE OBRA

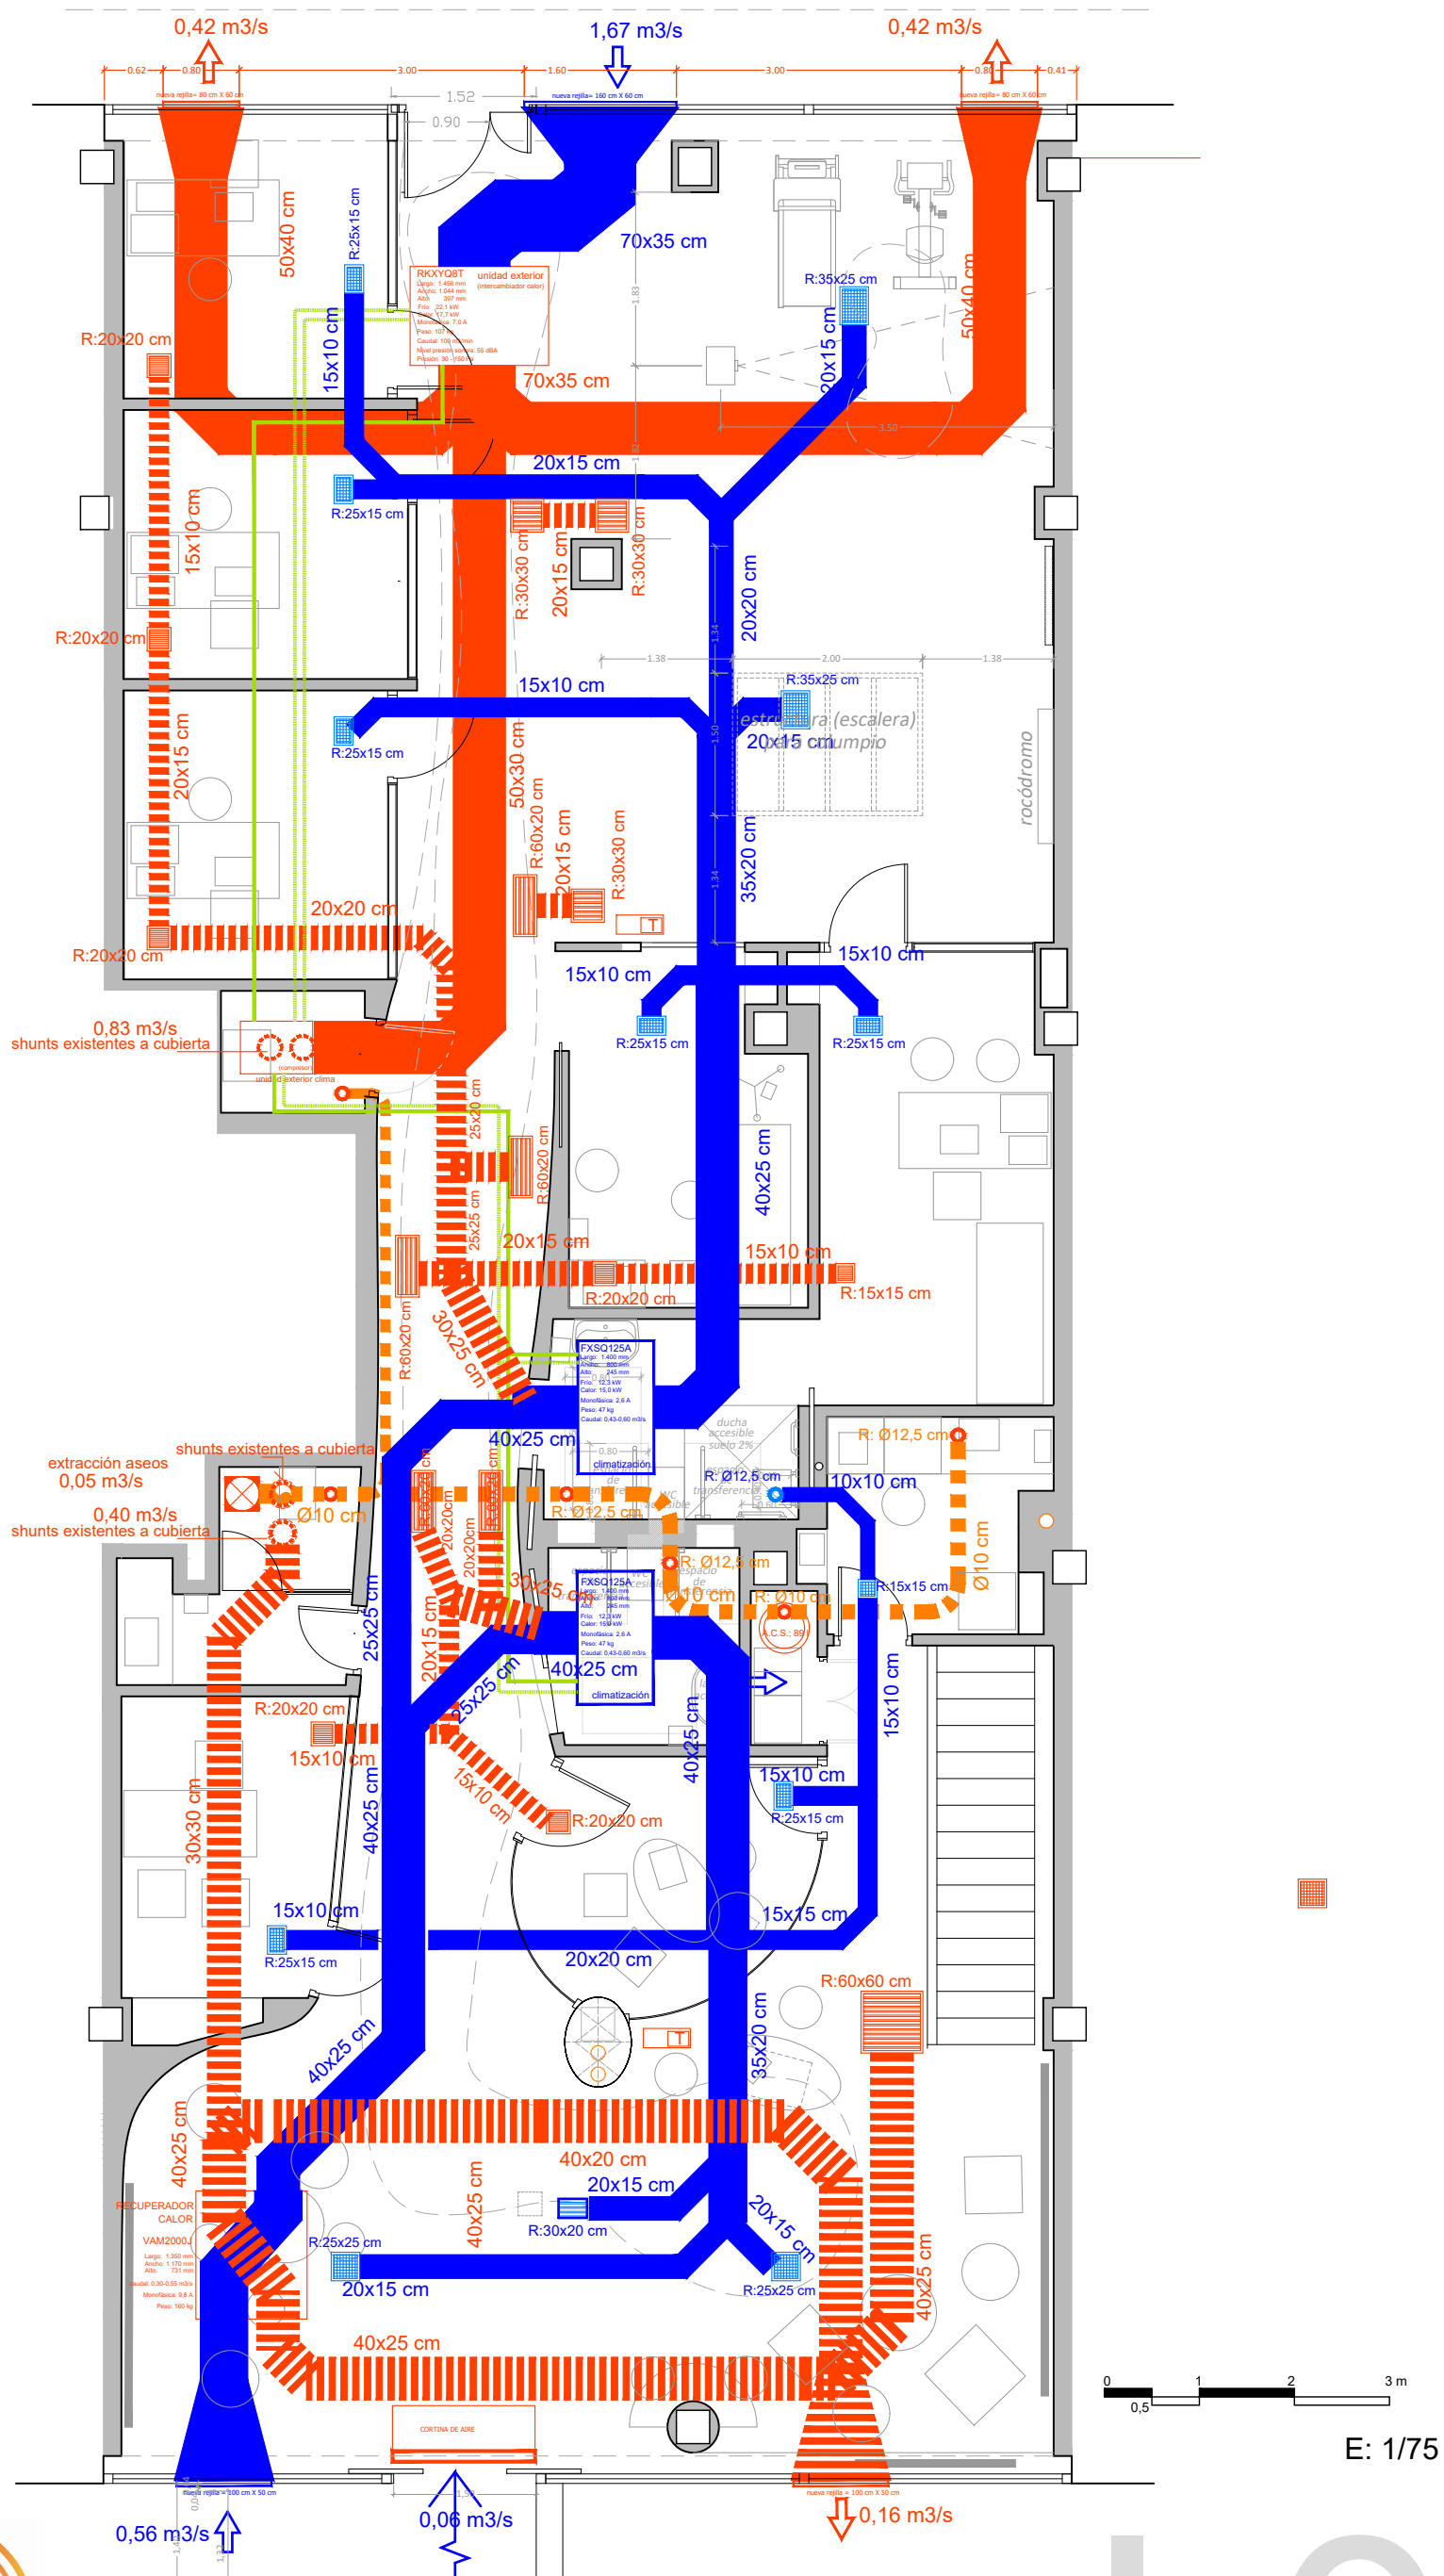

PEGASUS

REFORMA DE LOCAL PARA CENTRO DE REHABILITACIÓN EN AVDA. DE VALDEARGANDA, 2, ARGANDA DEL REY, MADRID (CP: 28500)

Arquitecto: Pablo Mosquera de Arancibia Con el patrocinio de:

eduetrade

fecha: 27/11/2023

colegiado COAM, nº: 11.444


PLANTA: CLIMATIZACIÓN Y VENTILACIÓN

FASE: DIRECCIÓN DE OBRA-CERTIFICADO FINAL DE OBRA



REFORMA DE LOCAL PARA CENTRO DE REHABILITACIÓN EN AVDA. DE VALDEARGANDA, 2, ARGANDA DEL REY, MADRID (CP: 28500)

Arquitecto: Pablo Mosquera de Arancibia Con el patrocinio de: **eduetrade**

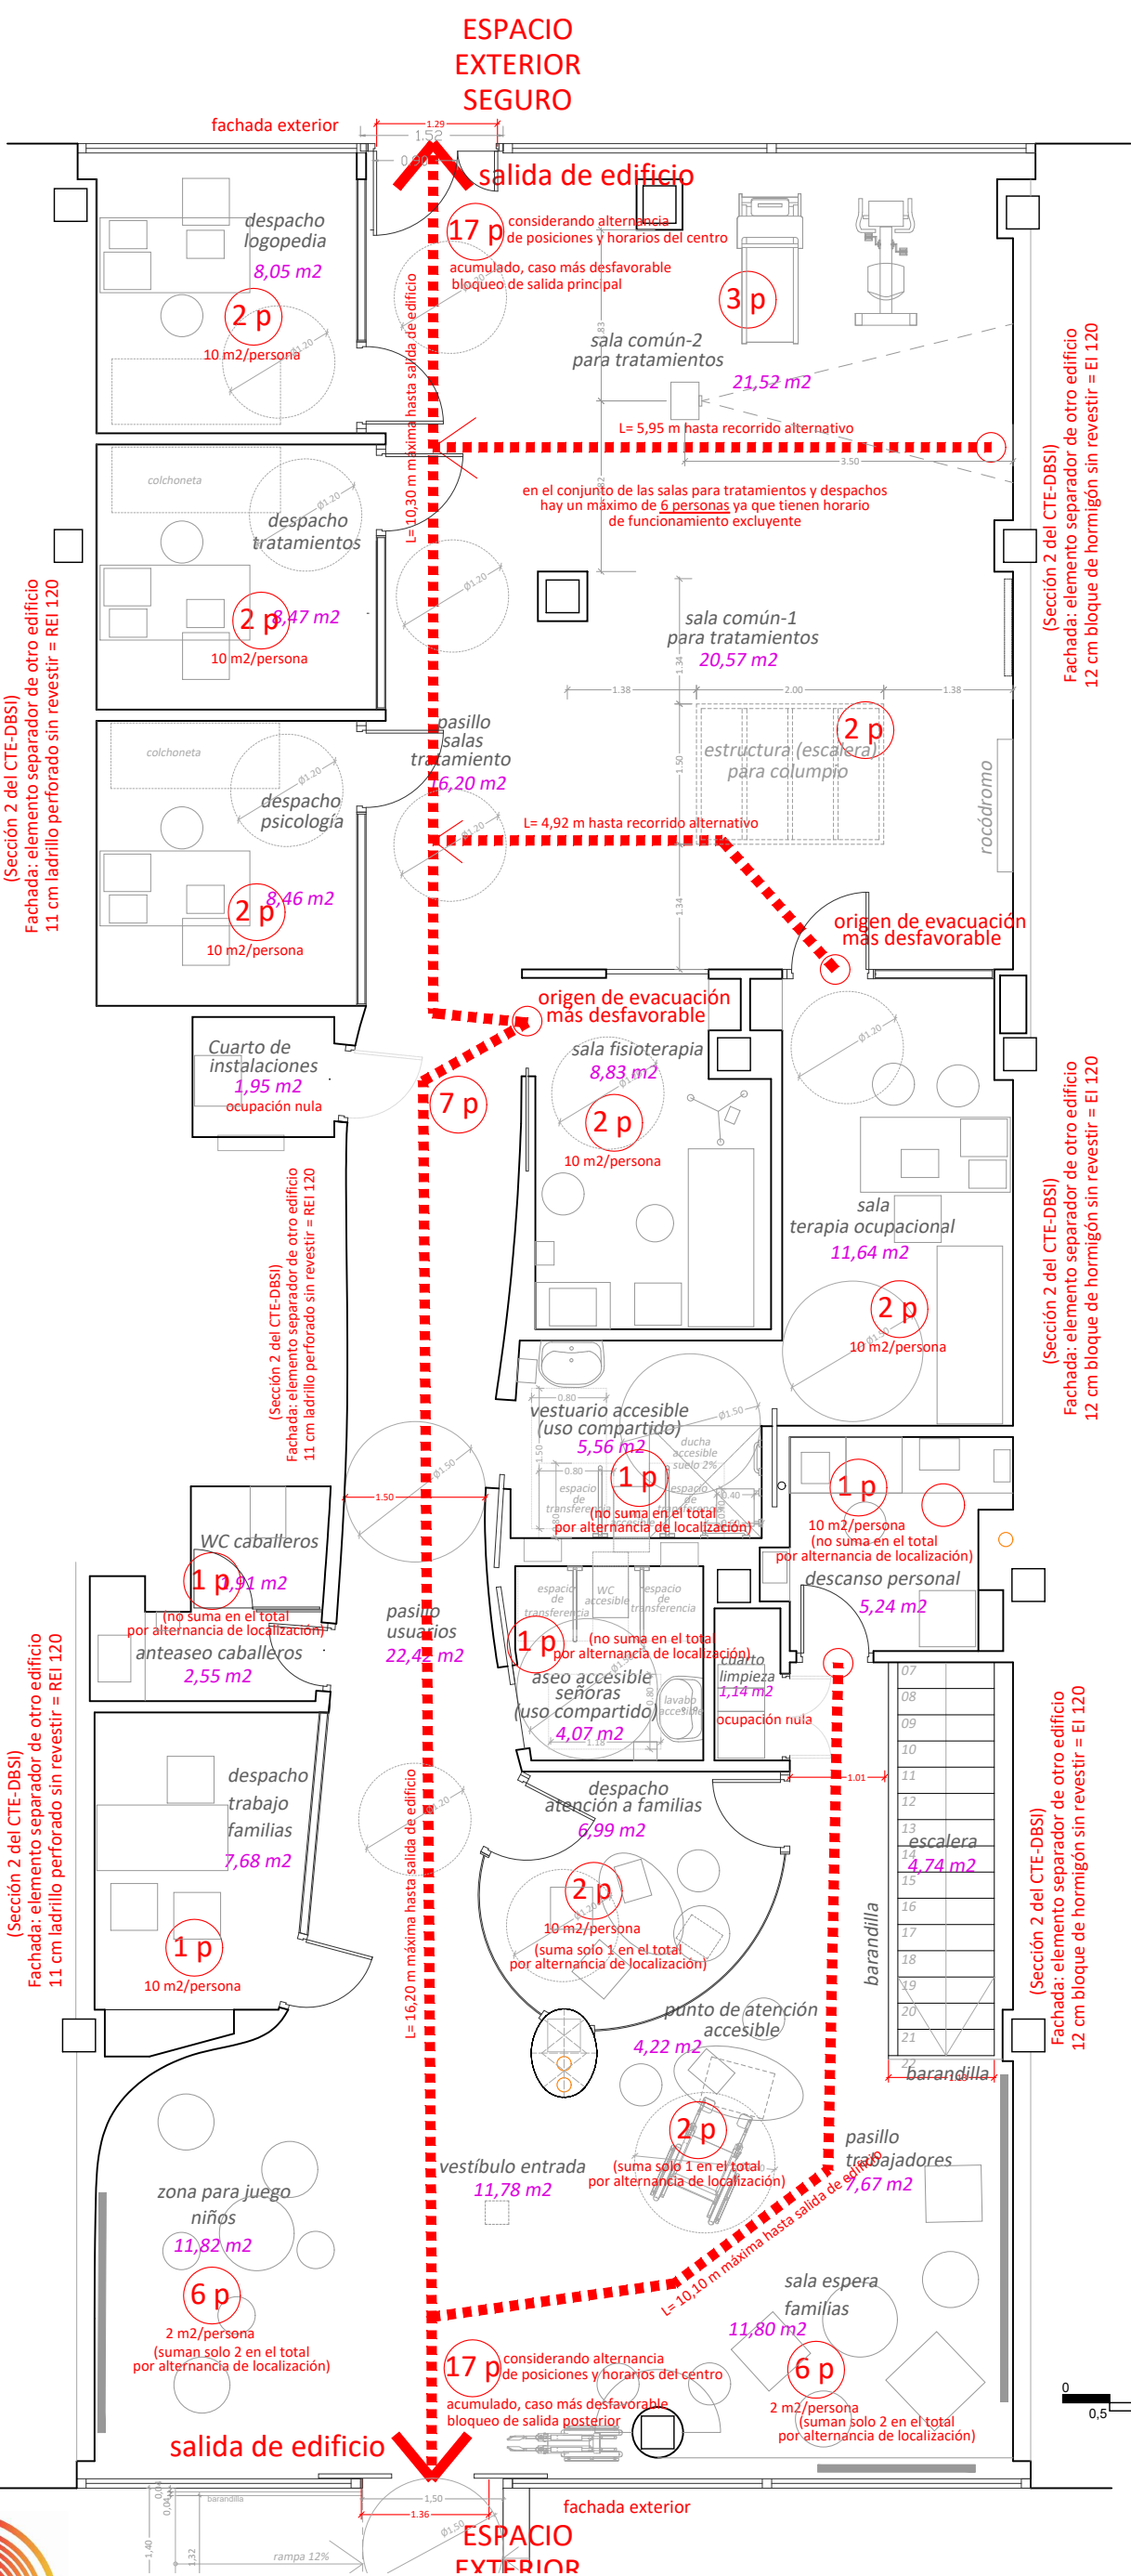

Origen de evacuación

Es todo punto ocupable de un edificio, exceptuando los del interior de las viviendas y los de todo recinto o conjunto de ellos comunicados entre sí, en los que la densidad de ocupación no exceda de 1 persona/5 m² y cuya superficie total no exceda de 50 m², como pueden ser las habitaciones de hotel, residencia u hospital, los despachos de oficinas, etc.

En general

- Todo establecimiento debe constituir sector de incendio diferenciado del resto del edificio excepto, en edificios cuyo uso principal sea Residencial Vivienda, los establecimientos cuya superficie construida no exceda de 500 m² y cuyo uso sea Docente, Administrativo o Residencial Público.

Tabla 2.1. Densidades de ocupación⁽¹⁾

Uso previsto	Zona, tipo de actividad	Ocupación (m²/persona)
Cualquiera	Zonas de ocupación ocasional y accesibles únicamente a efectos de mantenimiento: salas de máquinas, locales para material de limpieza, etc.	Ocupación nula
Residencial Vivienda	Asilos de planta	3
Residencial Vivienda	Plantas de vivienda	20
Residencial Público	Zonas de alojamiento	20
Residencial Público	Salones de uso múltiple	1
Residencial Público	Vestibulos generales y zonas generales de uso público en plantas de sótano, baja y entresuelo	2
Aparcamiento ⁽²⁾	Vinculado a una actividad sujeta a horarios: comercial, espectáculos, oficina, etc.	15
Aparcamiento ⁽²⁾	En otros casos	40
Administrativo	Plantas o zonas de oficinas	10
Administrativo	Vestibulos generales y zonas de uso público	2
Docente	Conjunto de la planta o del edificio	10
Docente	Locales diferentes de aulas, como laboratorios, talleres, gimnasios, salas de dibujo, etc.	5
Docente	Aulas (excepto de escuelas infantiles)	1,5
Docente	Aulas de escuelas infantiles y salas de lectura de bibliotecas	2
Hospitalario	Salas de espera	2
Hospitalario	Zonas de hospitalización	15
Hospitalario	Servicios ambulatorios y de diagnóstico	10

Se ha calculado la evacuación para una ocupación máxima de acuerdo a los ratios de densidades de ocupación del CTE-DB SI 3 (tabla 2.1.), asimilándolo al uso más parecido y teniendo en cuenta la alternancia de ocupaciones de los mismos usuarios en distintas zonas. El número máximo de trabajadores previsto en el edificio es de 7, con una previsión máxima de 12 pacientes y 8 familiares de forma simultánea.

Tabla F.1. Resistencia al fuego de muros y tabiques de fábrica de ladrillo cerámico o silico-calcáreo

Tipo de revestimiento	Espesor e de la fábrica en mm					
	Con ladrillo hueco	Con ladrillo macizo o perforado	Con bloques de arcilla ligada	Con bloques de arcilla ligada	Con bloques de arcilla ligada	Con bloques de arcilla ligada
Sin revestir	405e<80	805e<110	1105e<200	1405e<240	1405e<240	1405e<240
	(1)	(1)	REI-120	REI-240	REI-180	REI-240
Enfoscado	Por la cara expuesta	REI-30	REI-90	REI-120	REI-180	REI-240
	Por las dos caras	REI-60	REI-120	REI-180	REI-240	REI-240
Guarnecido	Por la cara expuesta	REI-60	REI-120	REI-180	REI-240	REI-240
	Por las dos caras	REI-90	REI-180	REI-240	REI-240	REI-240

(1) No es unid.

Resistencia al fuego de muros y tabiques de fábrica de ladrillo cerámico o silico-calcáreo

Puede considerarse que, a igualdad de espesor, un muro de ladrillo macizo o perforado tiene al menos la misma resistencia al fuego que un muro de ladrillo hueco, si trata de una solución con más masa.

Tabla F.2. Resistencia al fuego de muros y tabiques de fábrica de bloques de hormigón

Tipo de cámara	Tipo de árido	Tipo de revestimiento	Espesor nominal en mm	Resistencia al fuego
Simple	Silíceo	Sin revestir	100	EI-15
			150	REI-60
	Calizo	Sin revestir	100	EI-60
			150	REI-120
Doble	Arcilla expandida	Sin revestir	120	REI-120
			200	REI-180
	Guarnecido por las dos caras	Guarnecido por la cara expuesta (enfoscado por la cara exterior)	90	EI-180
			120	REI-240

0 0,5 1 2 3 m

E: 1/75

PROTECCIÓN CONTRA INCENDIOS OCUPACIÓN Y EVACUACIÓN

FASE: DIRECCIÓN DE OBRA-CERTIFICADO FINAL DE OBRA

REFORMA DE LOCAL PARA CENTRO DE REHABILITACIÓN EN AVDA. DE VALDEARGANDA, 2, ARGANDA DEL REY, MADRID (CP: 28500)

Arquitecto: Pablo Mosquera de Arancibia Con el patrocinio de: **eduetrade**

fecha: 27/11/2023

colegiado COAM, nº: 11.444


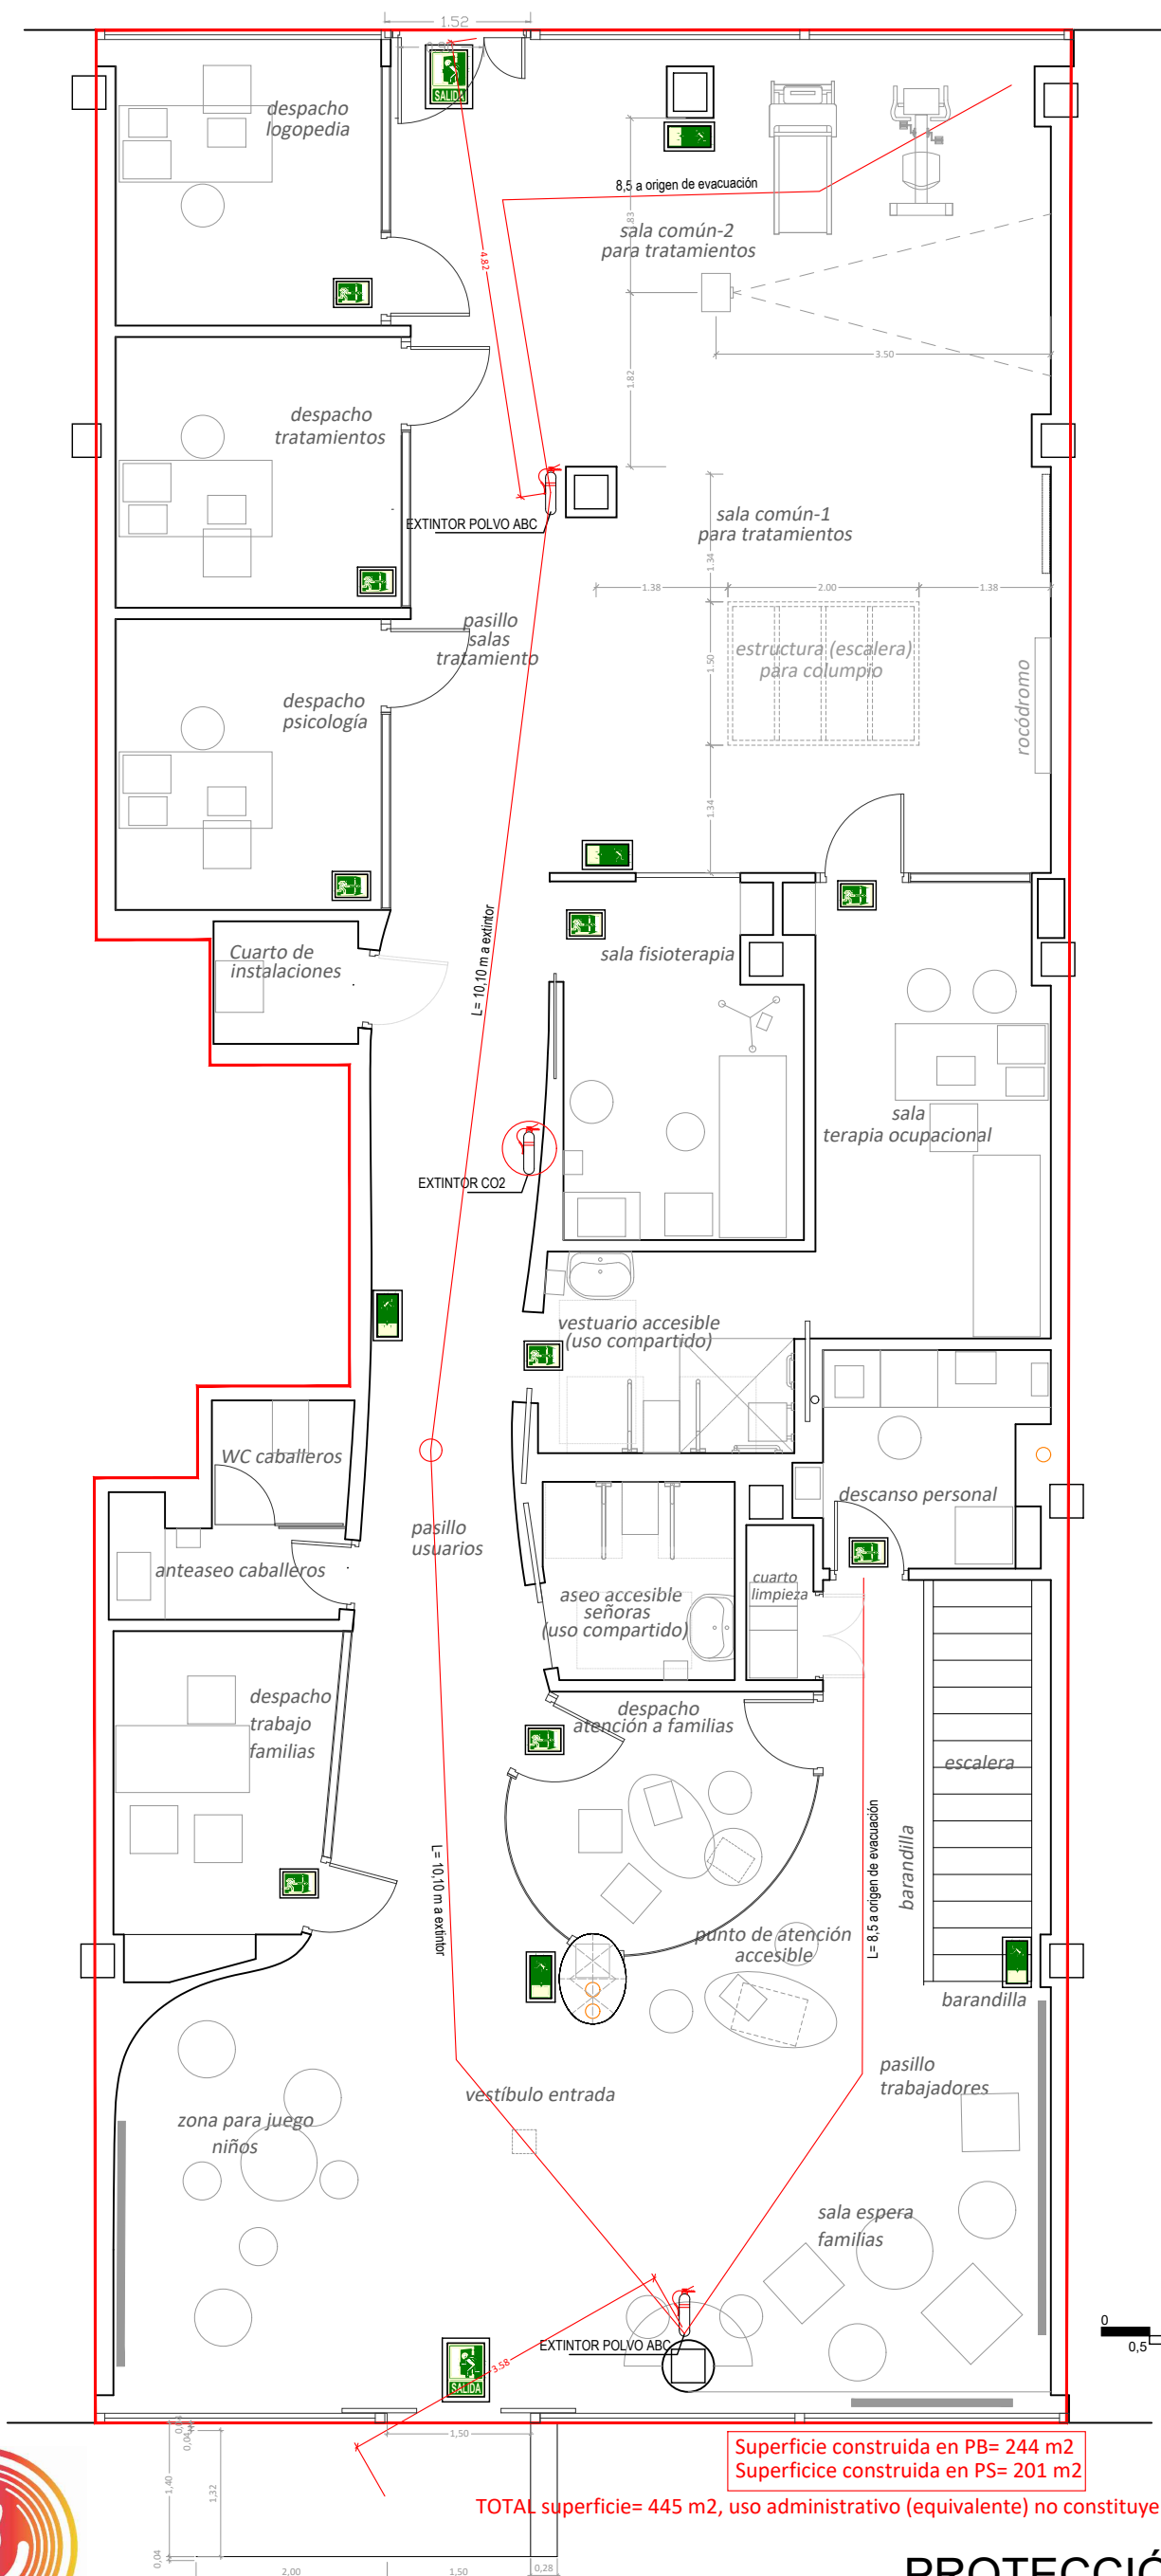


Tabla 1.1. Dotación de instalaciones de protección contra incendios	
Uso previsto del edificio o establecimiento	Condiciones
Instalación	
En general	
Extintores portátiles	Uno de oficina 21A-113B: - A 15 m de recorrido en cada planta, como máximo, desde todo origen de evacuación. - En las zonas de riesgo especial conforme al capítulo 2 de la Sección 1^ª de este DB.
Administrativo	
Bocas de incendio equipadas	Si la superficie construida excede de 2.000 m ² . ⁽¹⁾
Columna seca ⁽²⁾	Si la altura de evacuación excede de 24 m.
Sistema de alarma ⁽³⁾	Si la superficie construida excede de 1.000 m ² .
Sistema de detección de incendio	Si la superficie construida excede de 2.000 m ² , detecciones en zonas de riesgo alto conforme al capítulo 2 de la Sección 1 de este DB. Si excede de 5.000 m ² , en todo el edificio.
Hidrantas exteriores	Uno si la superficie total construida está comprendida entre 5.000 y 10.000 m ² . Uno más por cada 10.000 m ² adicionales o fracción. ⁽⁴⁾

LEYENDA	
	SEÑALIZACIÓN DE SALIDA
	SEÑALIZACIÓN DE SENTIDO DE EVACUACIÓN
	SEÑALIZACIÓN DE SALIDA POR ESCALERA ASCENDENTE
	EXTINTOR CO2 5 kg
	EXTINTOR POLVO ABC 6 kg

SEÑALIZACIÓN de los MEDIOS DE EVACUACIÓN DE ACUERDO AL pto. 7 del DB-SI-3 CUMPLIENDO CON LAS NORMAS UNE:

- UNE 23034: 1988
- UNE 23035-1: 2003
- UNE 23035-2: 2003
- UNE 23035-3: 2003
- UNE 23035-4: 2003

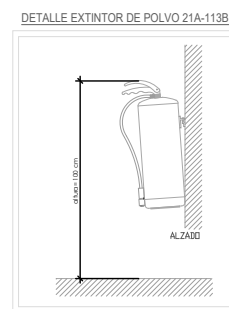

0 0,5 1 2 3 m

E: 1/75

Superficie construida en PB= 244 m2
Superficie construida en PS= 201 m2

TOTAL superficie= 445 m2, uso administrativo (equivalente) no constituye sector de incendios.



PEGASUS

REFORMA DE LOCAL PARA CENTRO DE REHABILITACIÓN EN AVDA. DE VALDEARGANDA, 2, ARGANDA DEL REY, MADRID (CP: 28500)

Arquitecto: Pablo Mosquera de Arancibia Con el patrocinio de:

eduetrade

fecha: 27/11/2023

colegiado COAM, nº: 11.444

FASE: DIRECCIÓN DE OBRA-CERTIFICADO FINAL DE OBRA

PROTECCIÓN CONTRA INCENDIOS
INSTALACIONES




LEYENDA	
 3lux;2,20m 150lm	SEÑALIZACIÓN DE EMERGENCIA: 150 lm; 3 lux, (altura colocación)
 5lux;2,20m 300lm	SEÑALIZACIÓN DE EMERGENCIA: 300 lm; 5 lux, (altura colocación)
	Foco empotrado en techo aseo (10 W); 4.000 K; 1.000 lm
	Foco empotrado en techo aseo (15 W); 4.000 K; 1.500 lm
	Luminaria empotrada en techo (20 W) 4.000 K; 2.560 lm

E: 1/75



ILUMINACIÓN

fecha: 27/11/2023

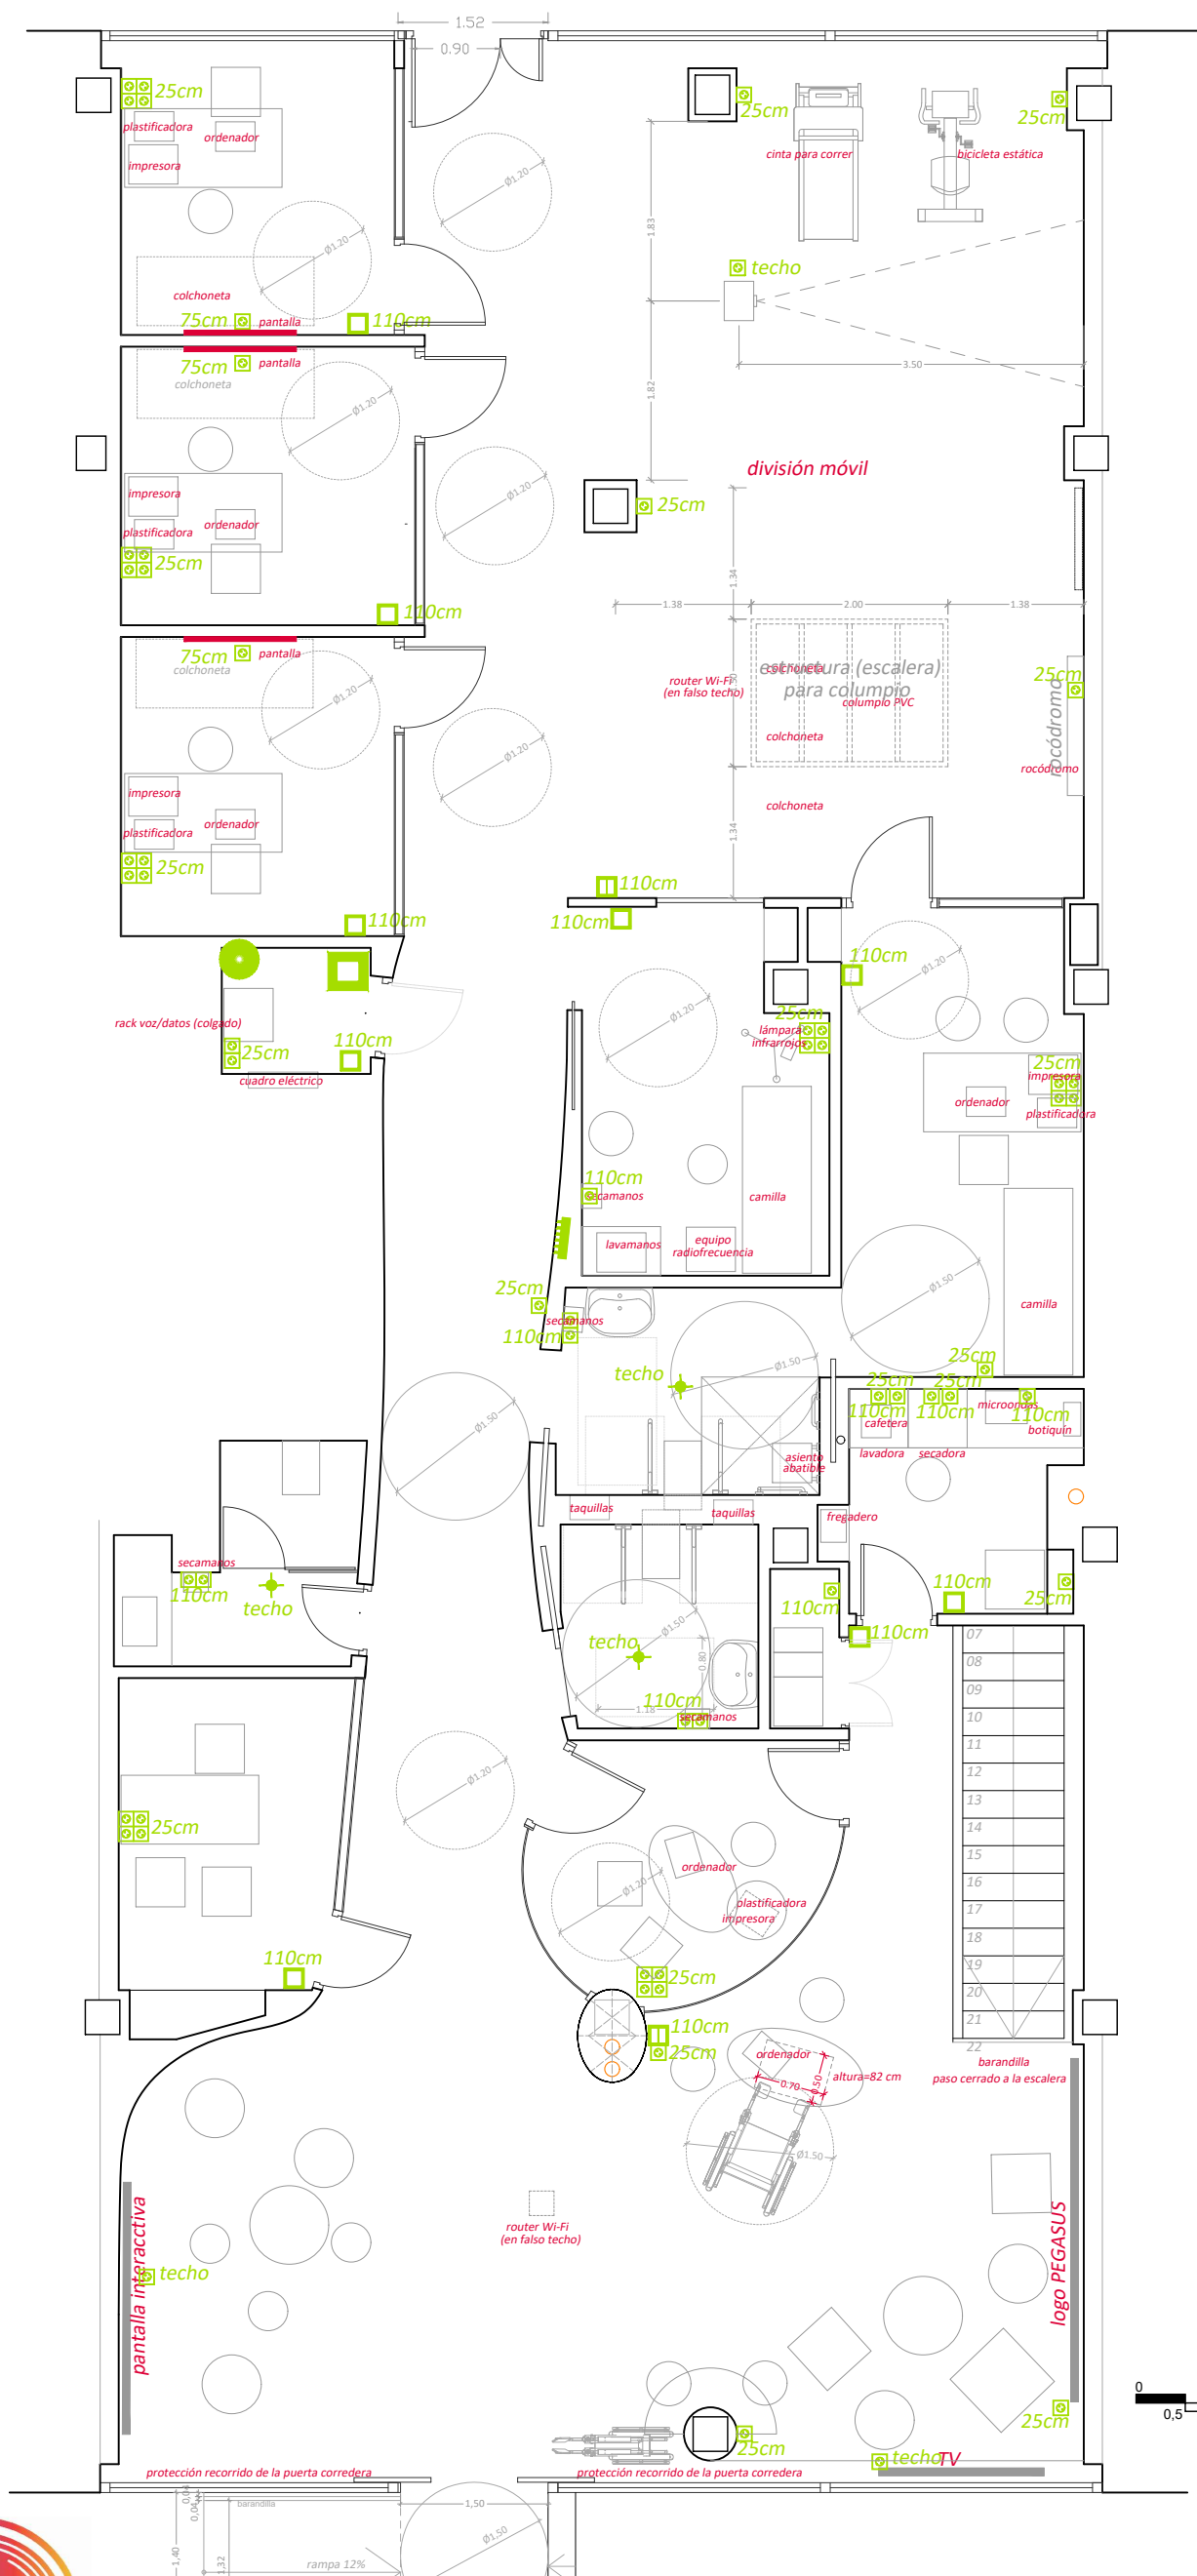

LEYENDA	
	ACOMETIDA
	CONTADOR
	TOMA ELÉCTRICA SENCILLA
	TOMA ELÉCTRICA CUÁDRUPLE
	INTERRUPTOR SENCILLO
	INTERRUPTOR DOBLE
	DETECTOR DE PRESENCIA
	CUADRO ELÉCTRICO



E: 1/75



PEGASUS

REFORMA DE LOCAL PARA CENTRO DE REHABILITACIÓN EN AVDA. DE VALDEARGANDA, 2, ARGANDA DEL REY, MADRID (CP: 28500)

Arquitecto: Pablo Mosquera de Arancibia Con el patrocinio de:

eduetrade

fecha: 27/11/2023


FASE: DIRECCIÓN DE OBRA-CERTIFICADO FINAL DE OBRA

ELECTRICIDAD - FUERZA

1.09

Potencia total: 16,31 kW
ACOMETIDA TRIFÁSICA: 10 m
ACOMETIDA TRIFÁSICA: 3X10 mm2

tipo de circuito	interruptor automático	nº máx. tomas	sección mínima de conductor	Ø mínimo de tubo
Iluminación	10 A	30	1,5 mm2	16 mm
Usos varios	16 A	20	2,5 mm2	20 mm
Aseos	16 A	20	2,5 mm2	20 mm
Lavadora y secadora	20 A	3	4 mm2	20 mm
Otros lectrodomésticos	16 A	6	2,5 mm2	20 mm
Bomba calor ACS	16 A	1	2,5 mm2	20 mm
Unidad exterior climatiz.	32 A (III)	1	5x4 mm2	68 mm
Unidad exterior compr.	20 A	1	4 mm2	20 mm
Unidad interior clima	16 A	2	2,5 mm2	20 mm
Recuperador de calor	16 A	1	2,5 mm2	20 mm
Extractor	10 A	1	2,5 mm2	20 mm

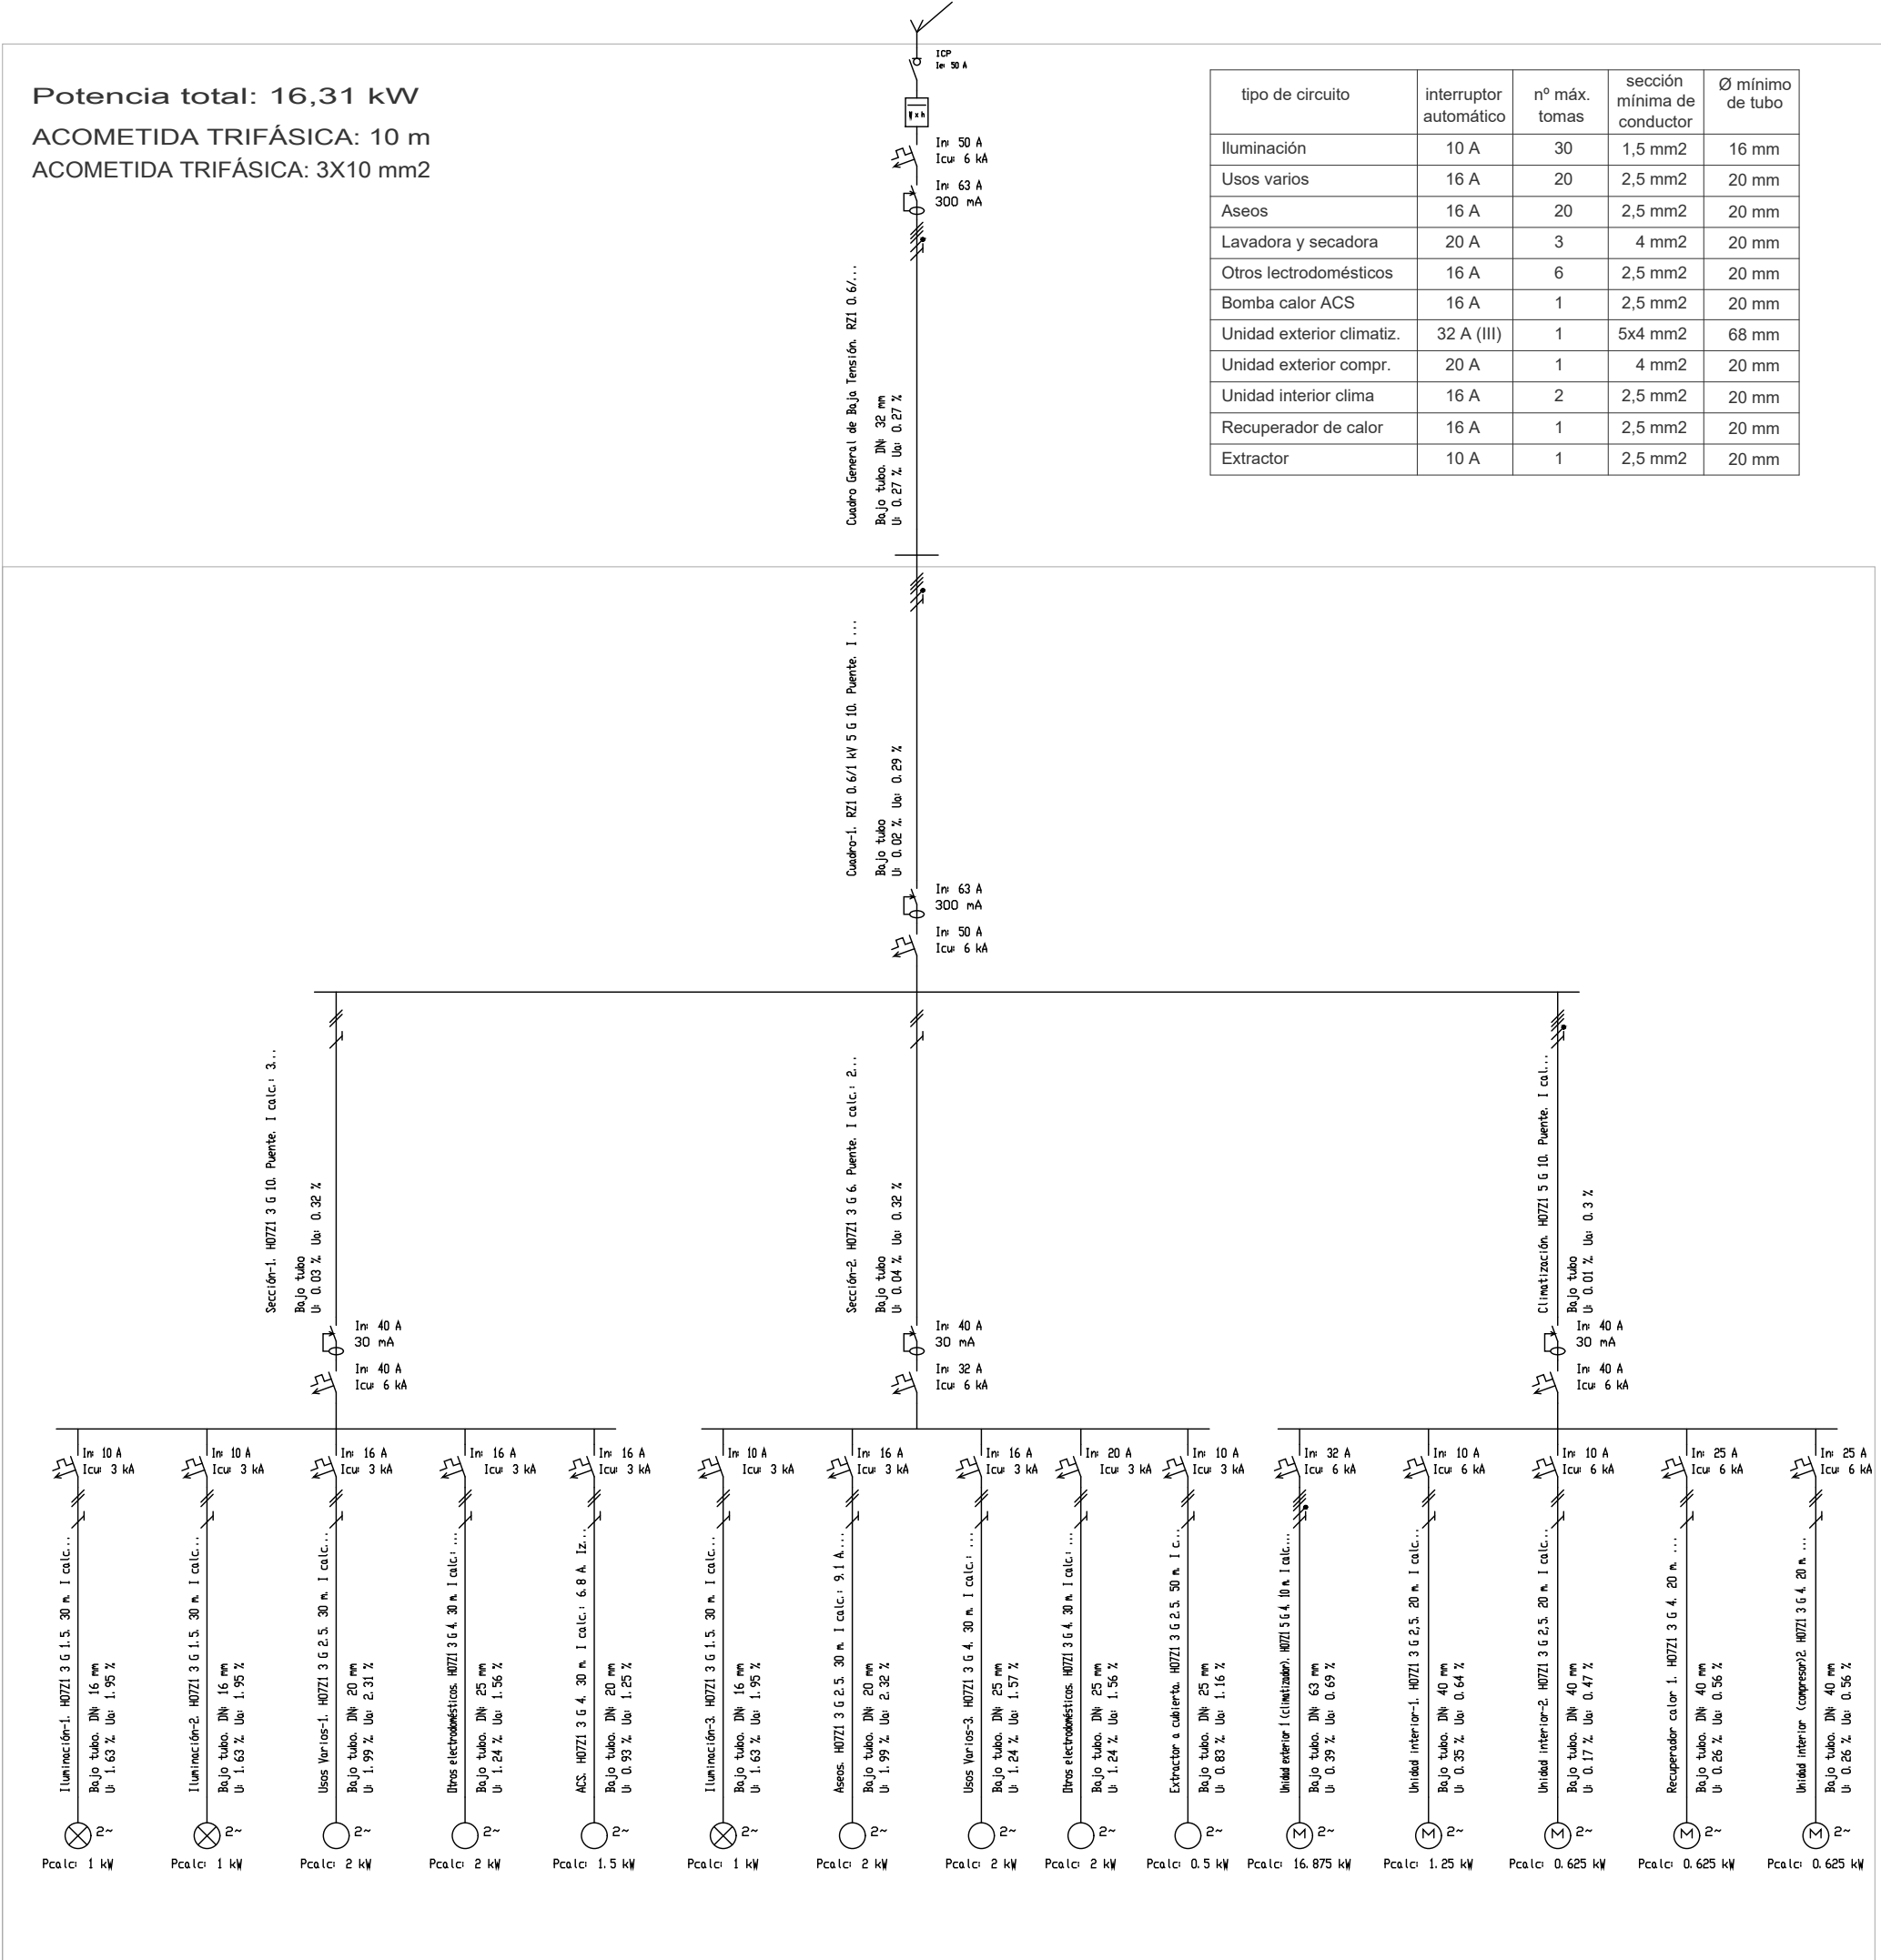


PEGASUS

REFORMA DE LOCAL PARA CENTRO DE REHABILITACIÓN EN AVDA. DE VALDEARGANDA, 2, ARGANDA DEL REY, MADRID (CP: 28500)
Arquitecto: Pablo Mosquera de Arancibia Con el patrocinio de: **edu@trade** fecha: 27/11/2023
colegiado COAM, nº: 11.444

FASE: DIRECCIÓN DE OBRA-CERTIFICADO FINAL DE OBRA

ELECTRICIDAD: ESQUEMA UNIFILAR

1.10

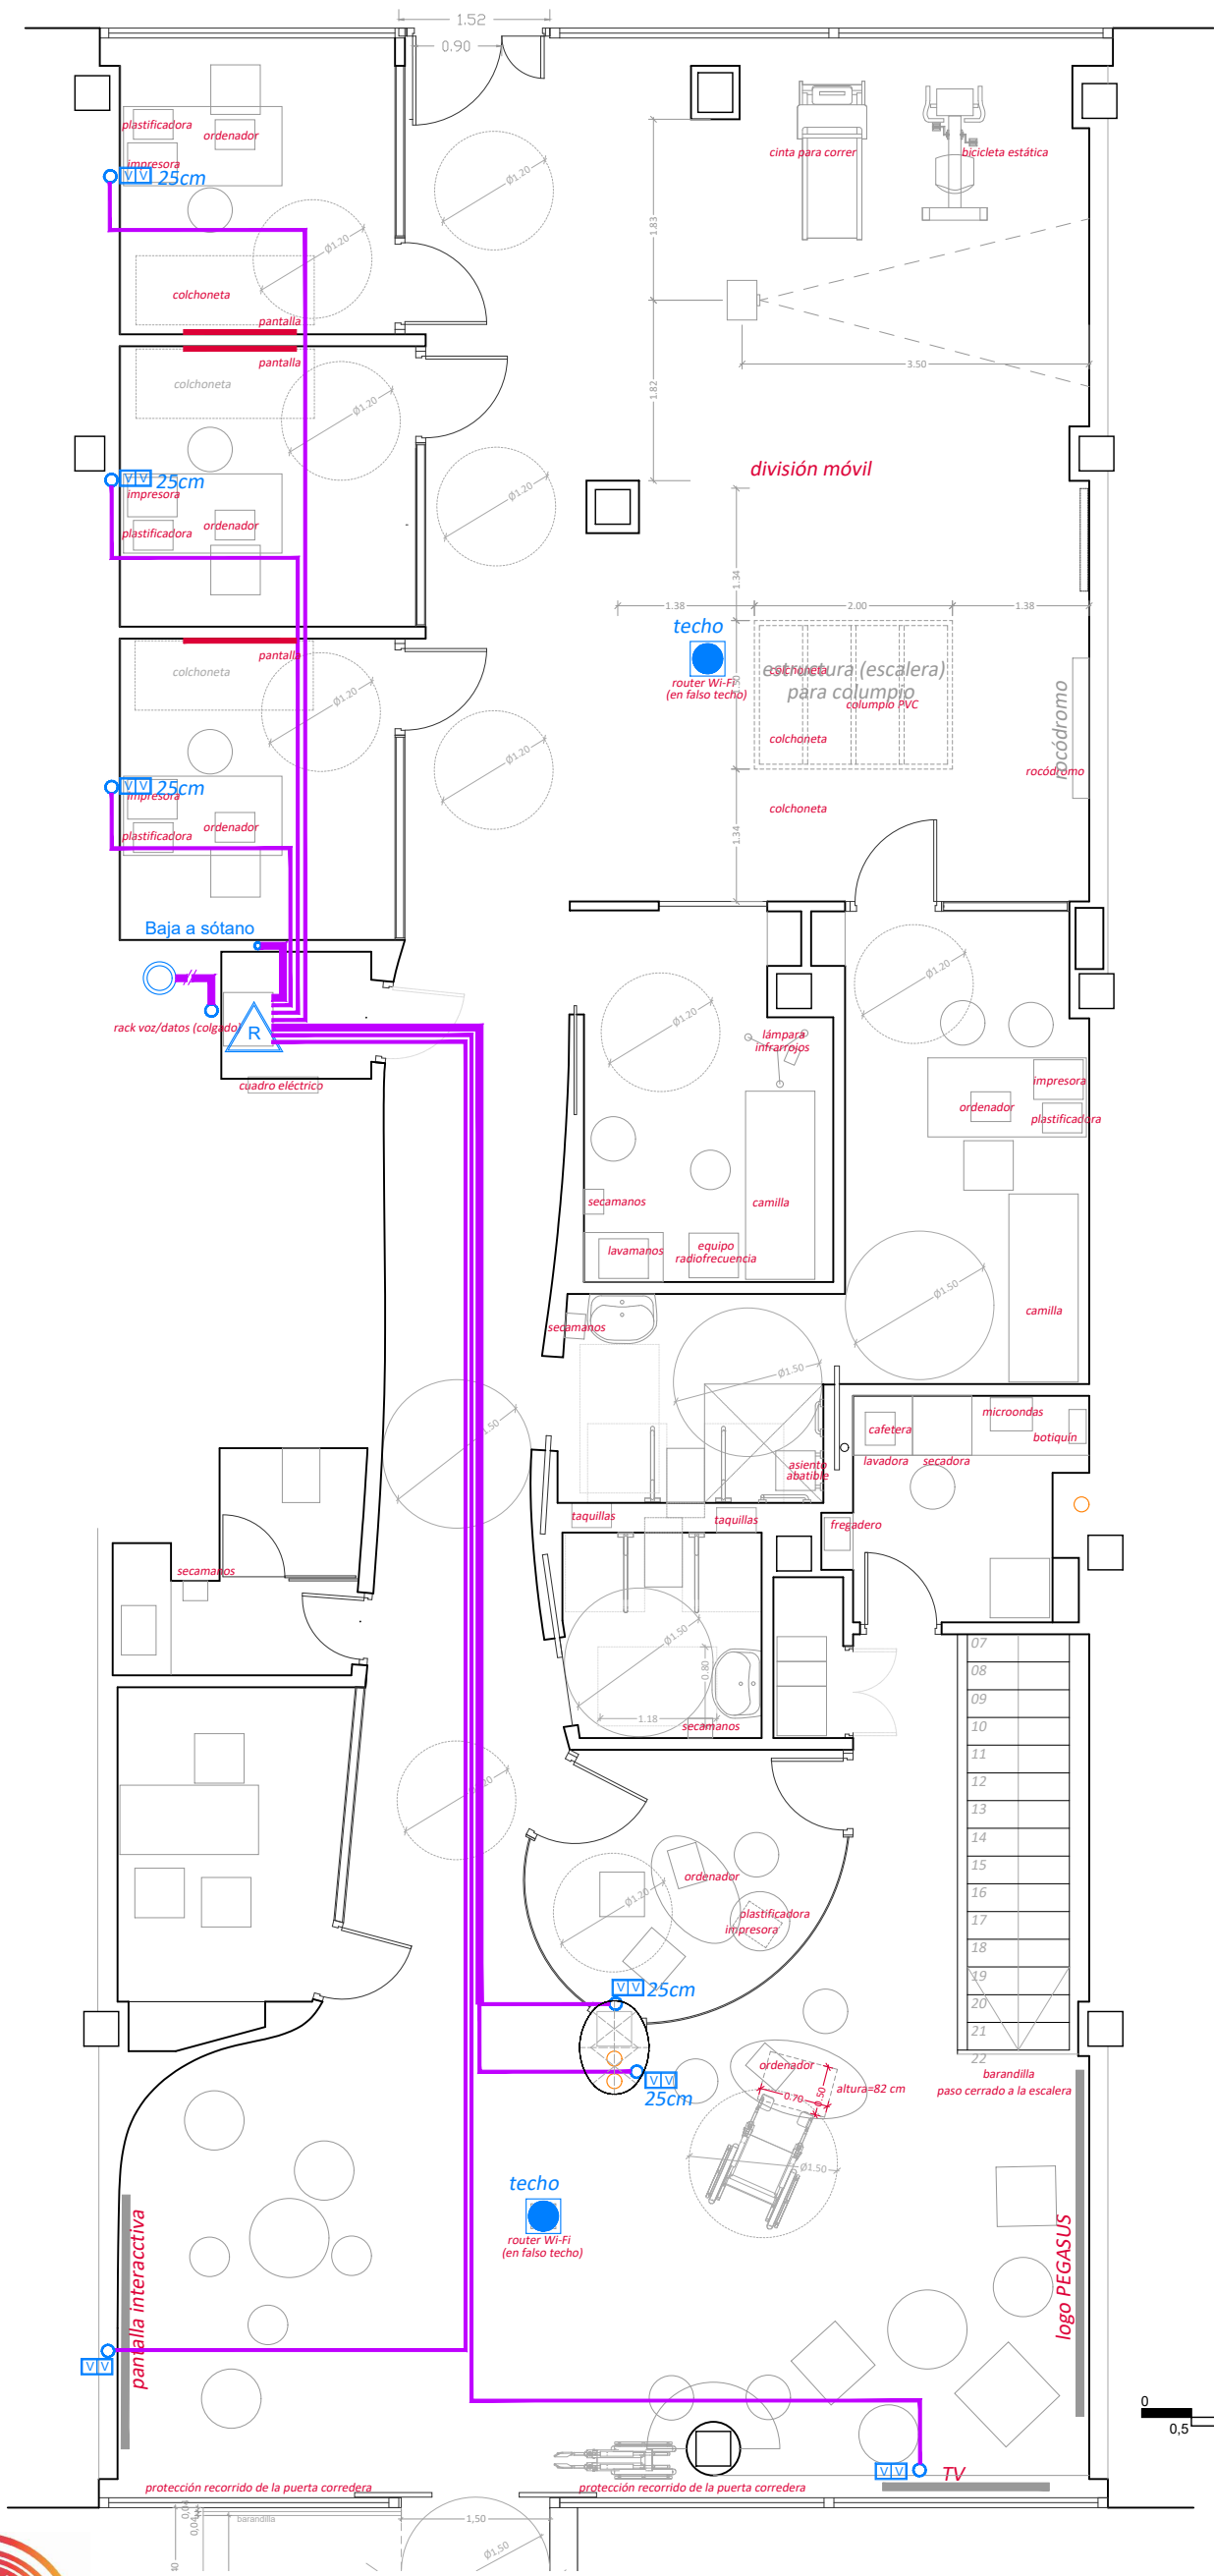

LEYENDA	
	ACOMETIDA
	CANALIZACIÓN VARIOS CIRCUITOS, POR TECHO 1 TUBOS P.V.C. #50mm
	CANALIZACIÓN DE DISTRIBUCIÓN 1 CIRCUITO, POR TECHO 1 TUBO CORRUGADO P.V.C. #25mm
	TOMA DOBLE DE DATOS
	RACK-CENTRALIZACIÓN
	MONTANTE



E: 1/75



PEGASUS

REFORMA DE LOCAL PARA CENTRO DE REHABILITACIÓN EN AVDA. DE VALDEARGANDA, 2, ARGANDA DEL REY, MADRID (CP: 28500)

Arquitecto: Pablo Mosquera de Arancibia Con el patrocinio de:

eduetrade

fecha: 27/11/2023

INSTALACIÓN DE DATOS

FASE: DIRECCIÓN DE OBRA-CERTIFICADO FINAL DE OBRA